



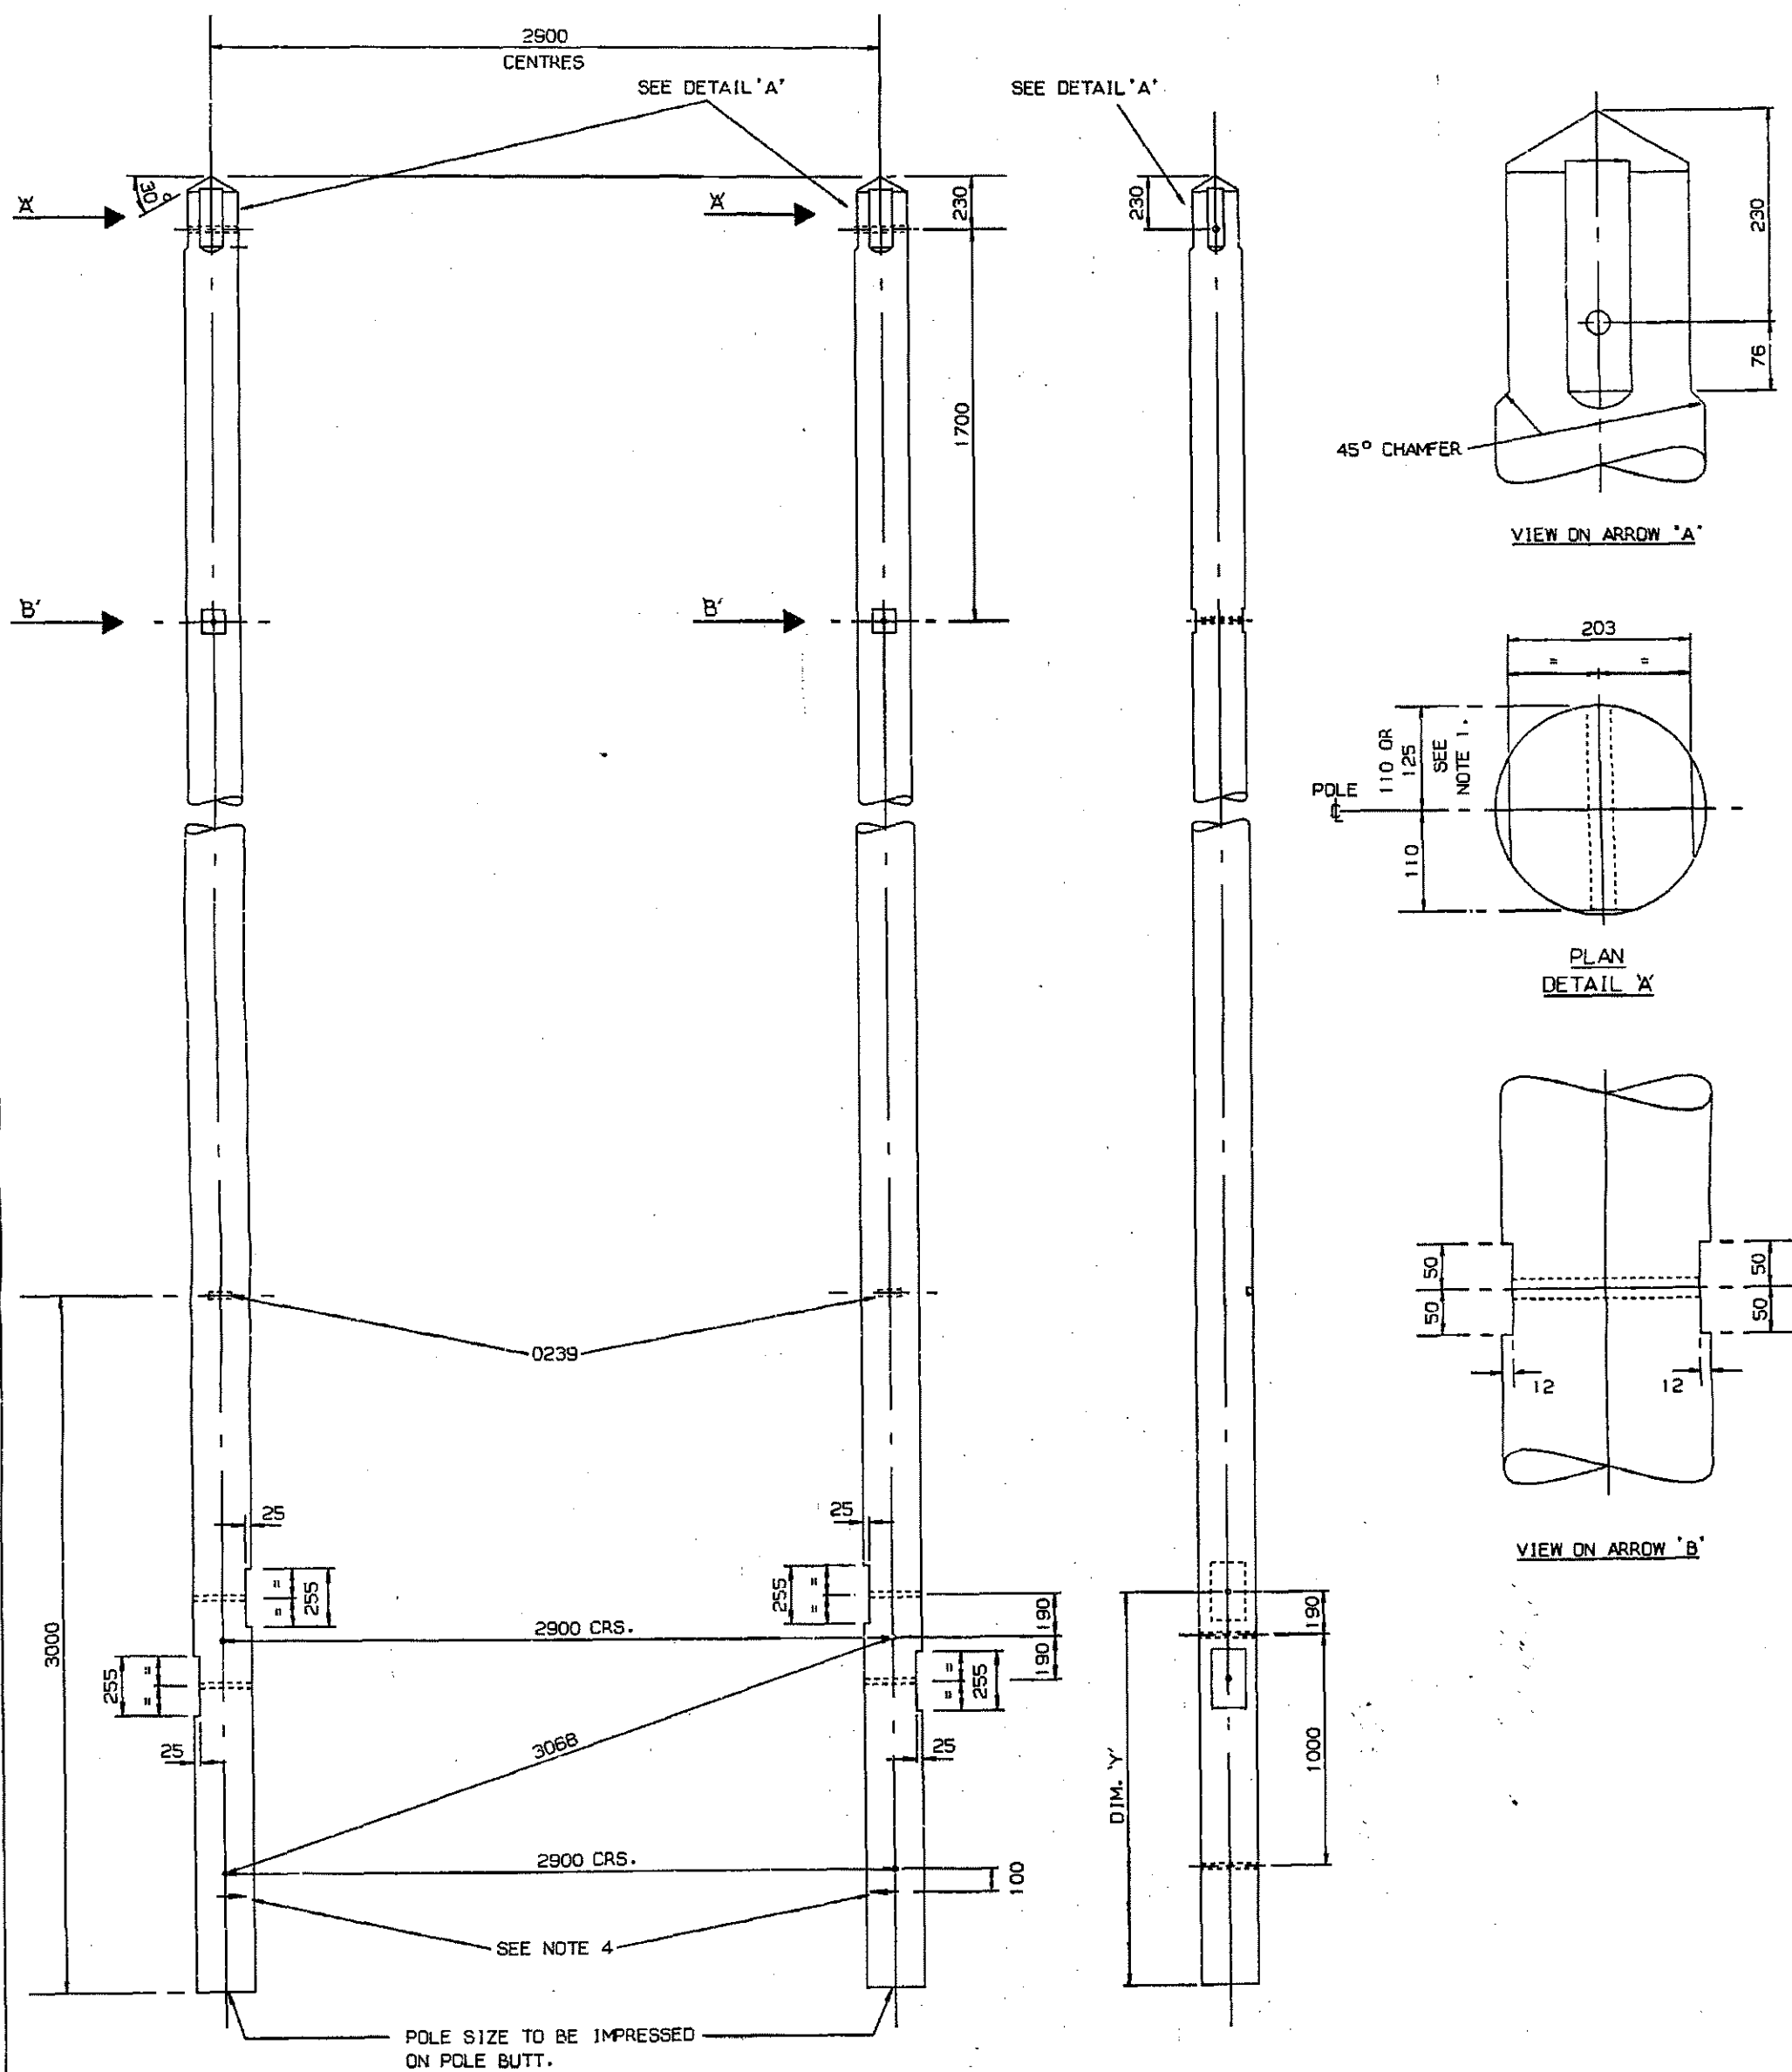

NOTES

1. POLE LEGS TO BE MATCHED. POLE TOP MINIMUM DIAMETER BEFORE FABRICATION 'STOUT' - 220mm OR 250mm AS REQUIRED ON ORDER.
2. HOLES TO BE 22mm DIAMETER DRILLED AT RIGHT ANGLES TO VERTICAL CENTRE LINE OF POLE. ALL DRILLING AND CUTTING TO BE DONE STRICTLY TO TEMPLATE PRIOR TO CREOSOTING.
3. POLE BUTTS CUT AT RIGHT ANGLES TO AXIS OF POLE. POLES TO BE NOTCHED AND DRILLED FOR DUPLICATE 250 X 125 BAULKS.
4. 50 X 6 X 6 DEEP ARROW MARK POINTING TOWARDS OPPOSITE POLE LEG TO BE GOUGED ON POLE FACE.

All dimensions shown are in millimetres unless stated otherwise

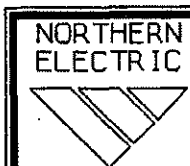

Drawn
J.B.

Traced

Checked
R.M.D.

Date Issued
OCT 90

Operations Director's Dept., Carillon House Newcastle-upon-Tyne NE1 6NE.

33kV DOUBLE CIRCUIT OVERHEAD LINES.
DRILLING, SCARFING AND MARKING FOR
STRAIGHT LINE SECTION AND SECTION ANGLE 'H' POLE.

Drg. No. 1 09 116 1152

Sheet No. 2

No. of Sheets

Scale 1:20 & 1:5.