

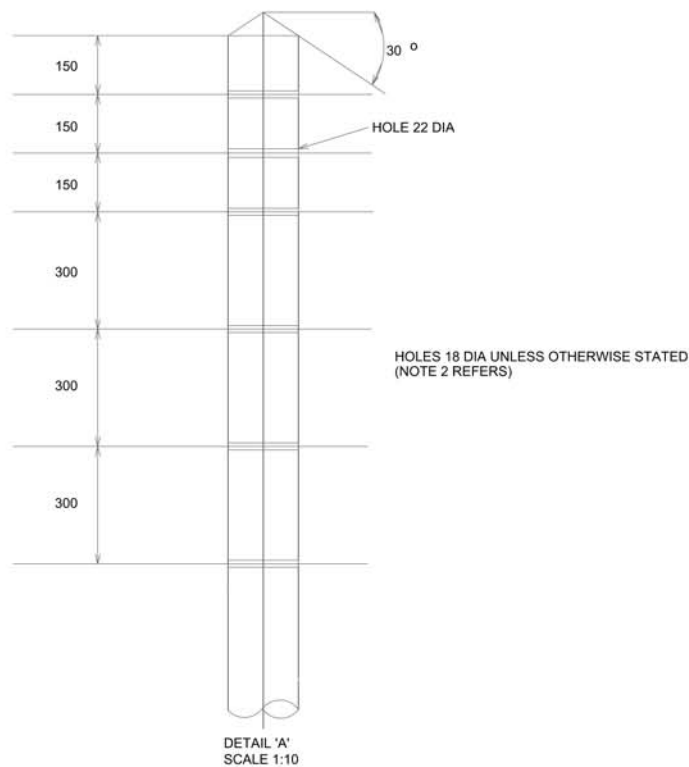


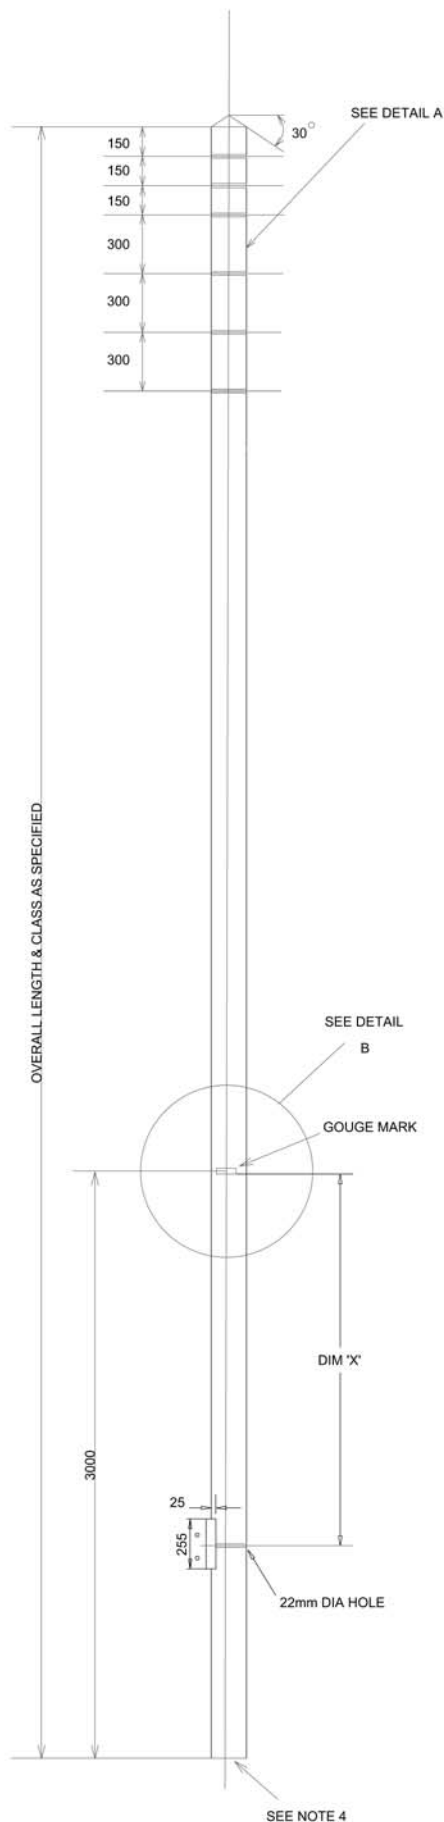

N.B.
CHARACTERS TO BE
50mm HIGH

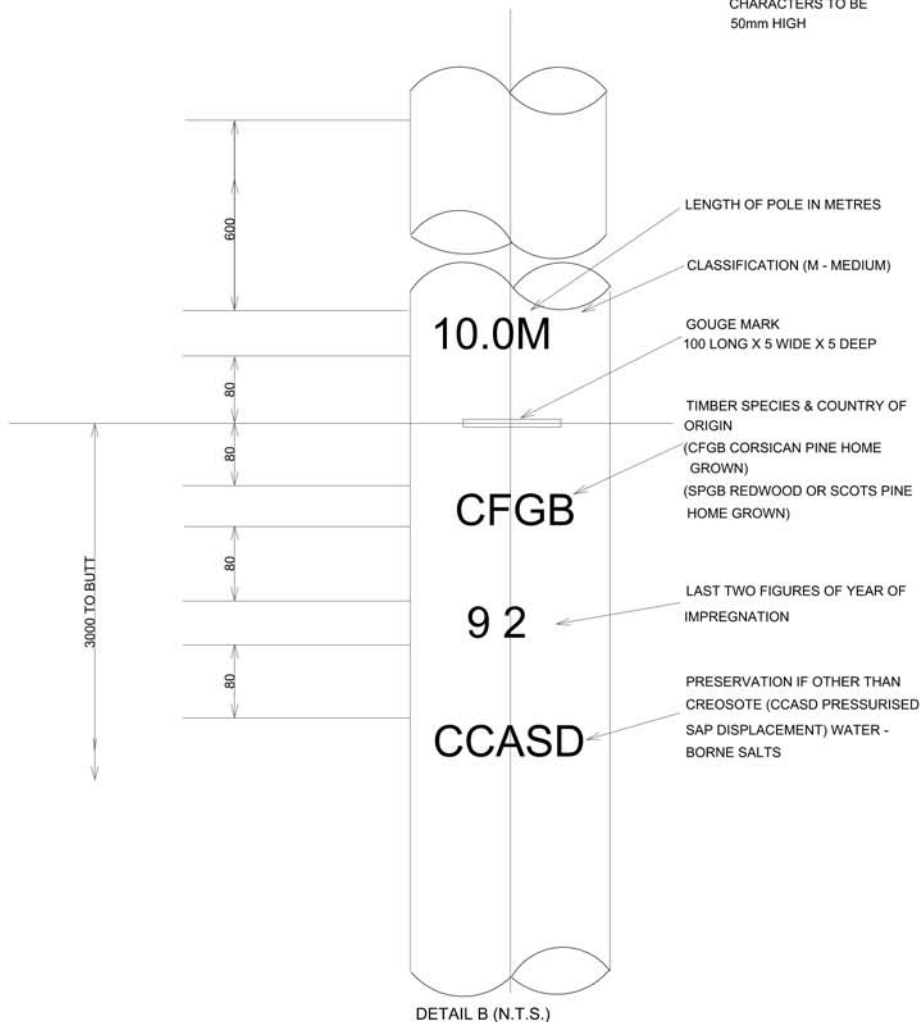

POLE LENGTH	SINKING DEPTH (M)
9.0 - 11 INCL.	1.6

- NOTES
1. POLES TO BE HOME GROWN SOFTWOOD TREATED BY PRESSURISED SAP DISPLACEMENT (SALT TREATMENT)
 2. NUMBER AND SPACING OF HOLES TO BE SPECIFIED
 3. POLE TO BE EVENLY QUARTERED. APEX - 120
 4. POLE LENGTH, CLASSIFICATION AND FABRICATION DRG. No. MARKED ON BUTT USING METAL MARKER TAPE
 5. BASED ON ESI STANDARD 43-88 APPENDIX N AND ESI DRG No 433001
 6. HOLES TO BE 18mm DIA. UNLESS SPECIFIED OTHERWISE

		Lloyds Court, 78 Grey Street, Newcastle Upon Tyne, NE1 6AF	
Manufacturer Details		LV OVERHEAD LINES DRILLING AND MARKING OF WOOD POLES FOR OPEN WIRE AND ABC CONSTRUCTION	
Sheet No. 3	Scale 1:20	Type OVERHEAD LINES	
Prepared By J. G. W. WOOD		Ref No. C101820	
Revised 08/04/08	Grid Reference	Historic Drg. No. 1091193301	
Date Issued 20/01/05	Checked By G. HAMMILL	Revision 1-1 Notes	

ALL DIMENSIONS SHOWN ARE IN MILLIMETRES UNLESS OTHERWISE STATED