
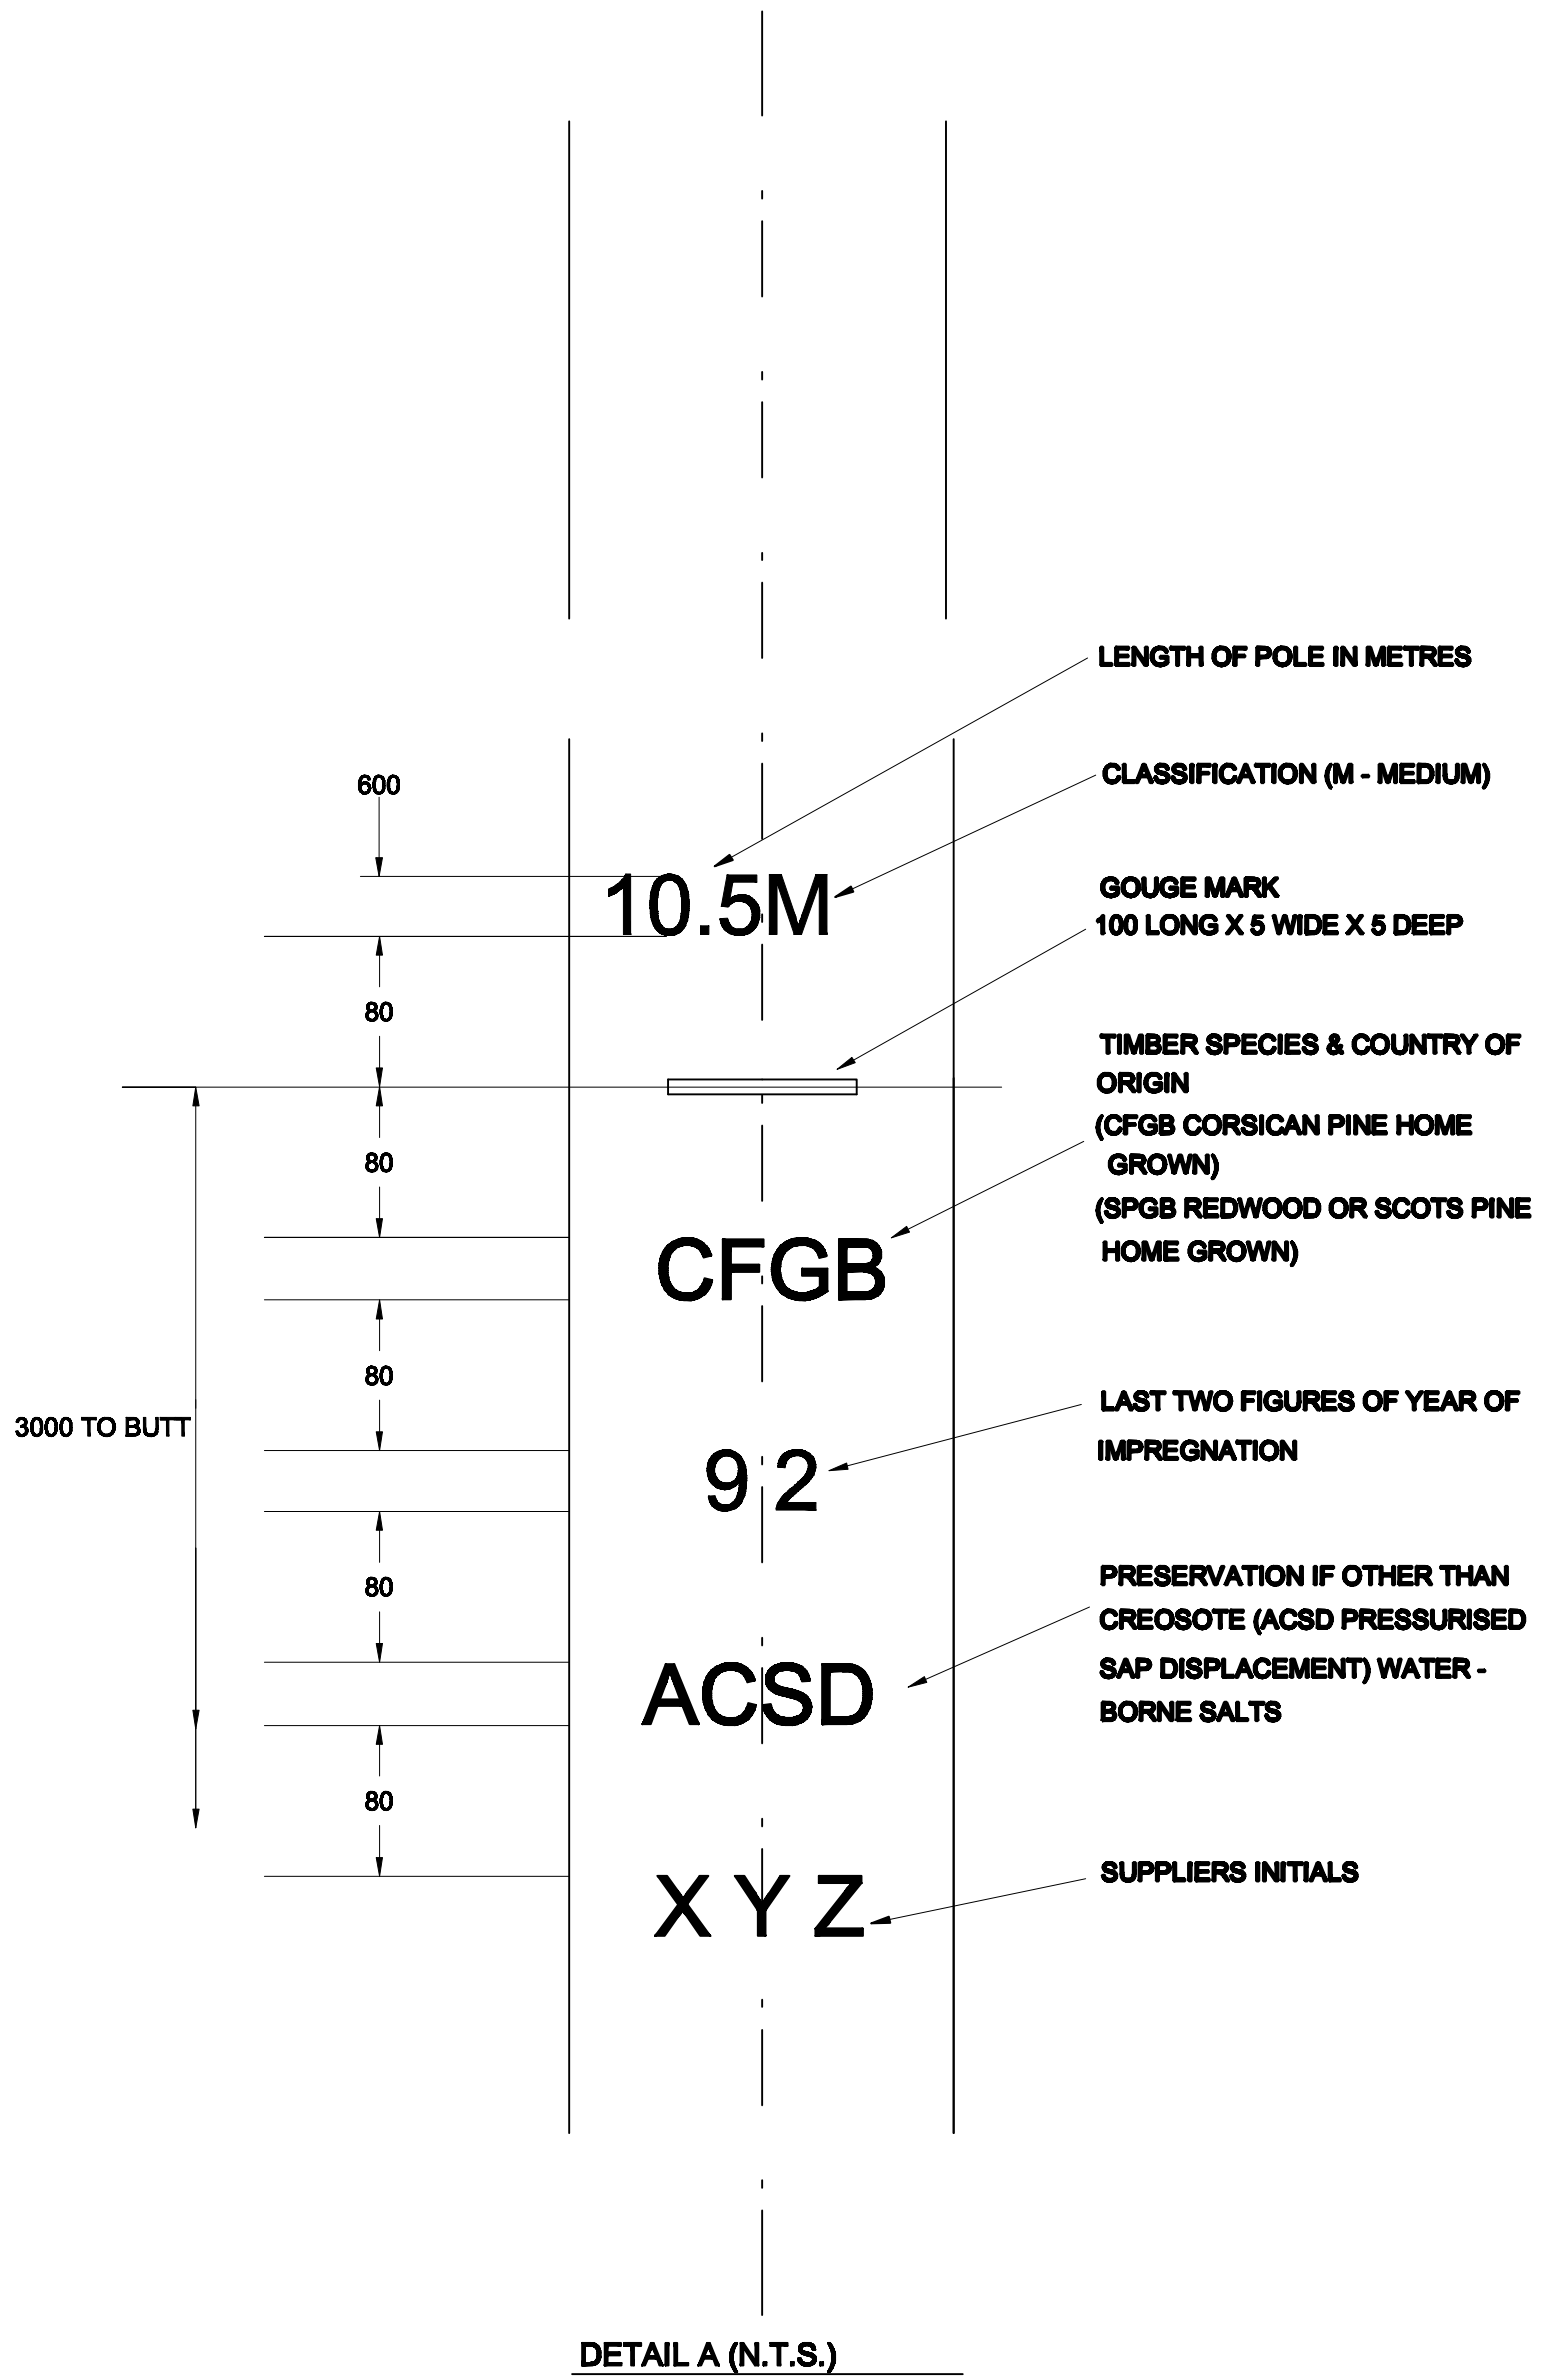


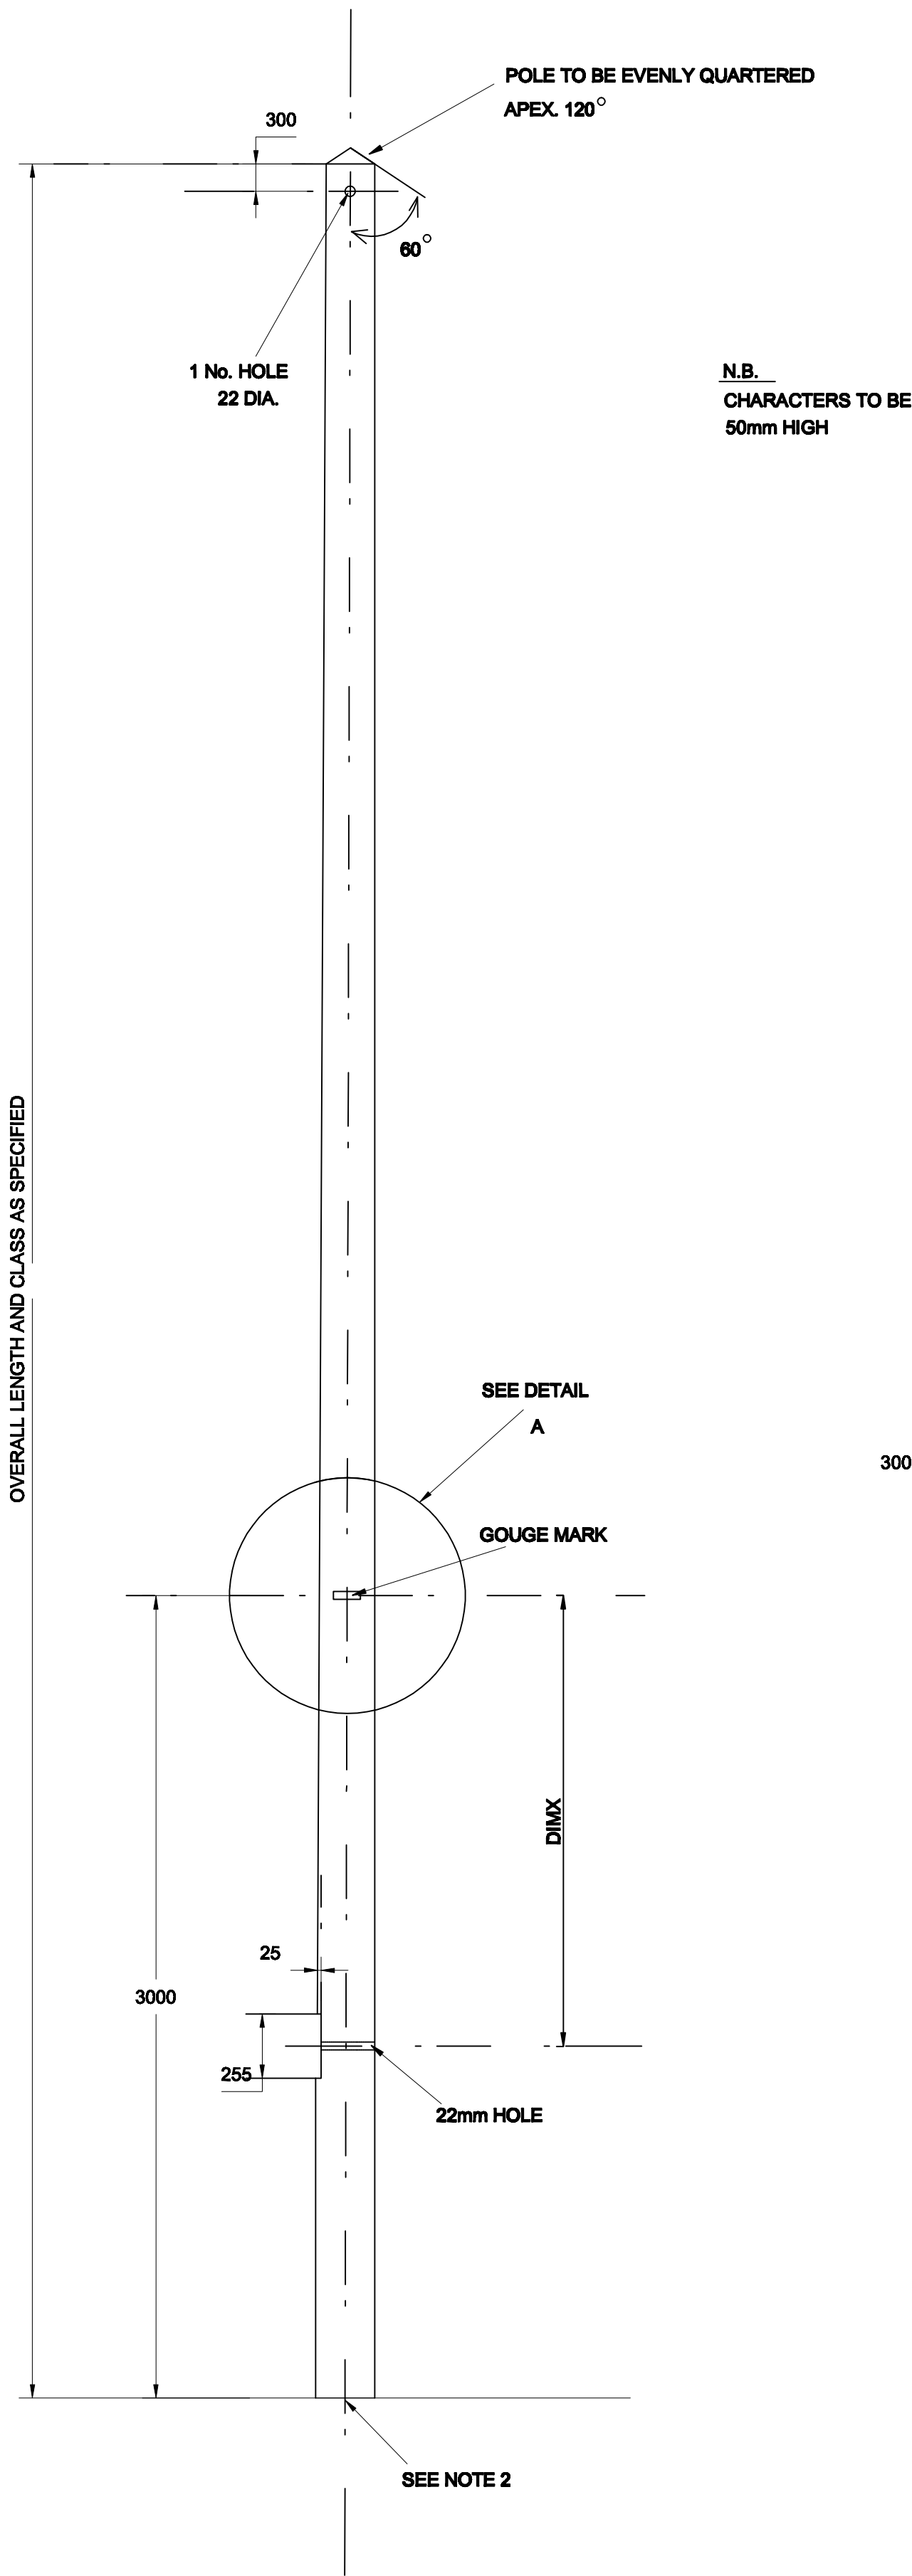

NOTES:

- POLES SHALL BE SOURCED, FABRICATED AND TREATED IN ACCORDANCE WITH ENA TS 43-88 AND NPS/001/001. UNLESS STATED OTHERWISE ON THE PROJECT ORDER POLES SHALL BE TREATED WITH CREOSOTE.
- POLE LENGTH, CLASSIFICATION, DATE OF TREATMENT & SUPPLIERS NAME OR MARK TO BE MARKED ON THE BUTT END GRAIN AND AT THE 3m. GOUGE MARK. THIS MAY BE ACHIEVED BY ENGRAVING THE WOOD OR THE USE OF RECESSED ENGRAVED DISCS. (THE POLE BUTT MAY ALSO EMPLOY THE USE OF METAL MARKER TAPES).

POLE LENGTH (m)	DIMENSION 'X' (mm)	SINKING DEPTH (mm)
9.0 - 10.0	1900	1600
11.0 - 14.0	1700	1800

ALL DIMENSIONS SHOWN ARE IN MILLIMETRES UNLESS OTHERWISE STATED

NORTHERN POWERGRID Manufacturer Details		Lloyds Court, 78 Grey Street, Newcastle Upon Tyne, NE1 6AF	
		LV OVERHEAD LINES DRILLING AND MARKING OF WOOD POLES FOR ABC CONSTRUCTION	
		Type	LINES
Sheet No. 4	Scale 1:20	Ref No.	C101821
Prepared By Joan.Oakley	Grid Reference	Revision	J
Revised 04/11/13	Checked By S SALKELD	Notes	
Date Issued 17/03/05		Historic Drg.No.	1091193301