

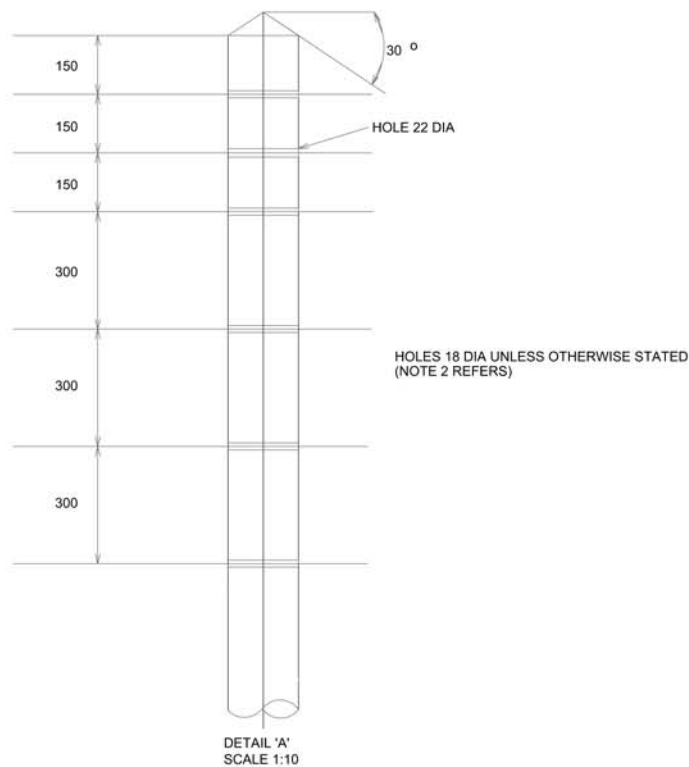


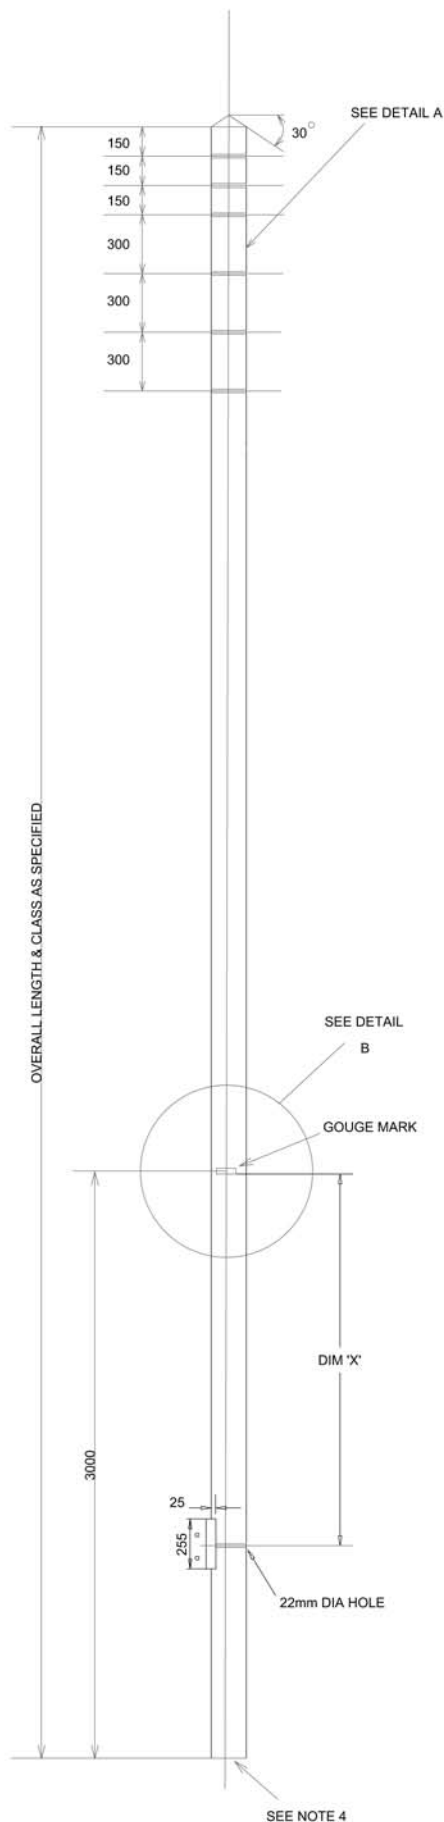

N.B.  
CHARACTERS TO BE  
50mm HIGH

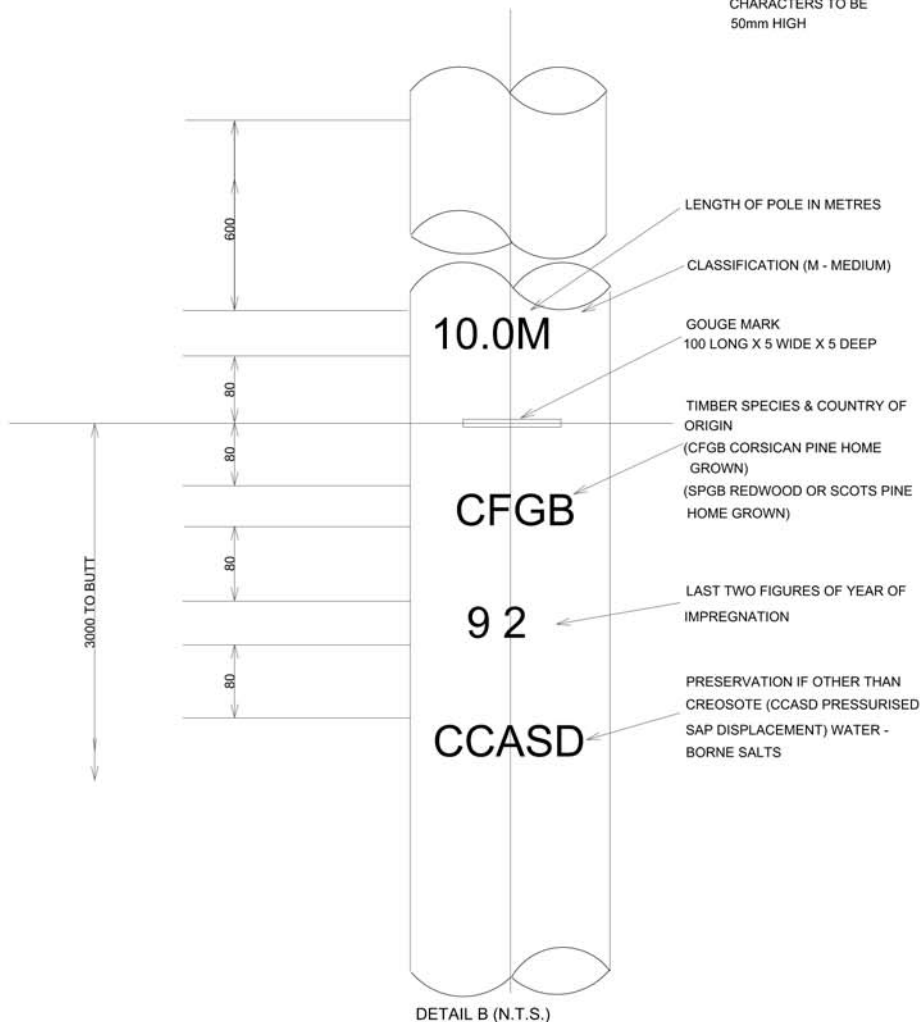

#### NOTES

- POLES TO BE HOME GROWN SOFTWOOD TREATED BY PRESSURISED SAP DISPLACEMENT (SALT TREATMENT)
- NUMBER AND SPACING OF HOLES TO BE SPECIFIED
- POLE TO BE EVENLY QUARTERED. APEX - 120
- POLE LENGTH, CLASSIFICATION AND FABRICATION DRG. No. MARKED ON BUTT USING METAL MARKER TAPE
- BASED ON ESI STANDARD 43-88 APPENDIX N AND ESI DRG No 433001
- HOLES TO BE 18mm DIA. UNLESS SPECIFIED OTHERWISE

| POLE LENGTH (m) | DIMENSION 'X' (mm) | SINKING DEPTH (mm) |
|-----------------|--------------------|--------------------|
| 9.0 - 11.0      | 1900               | 1600               |
| 12.0            | 1700               | 1800               |
| 13.0 - 14.0     | 1400               | 1800               |



|                        |                     |
|------------------------|---------------------|
| Manufacturer Details   |                     |
| Sheet No. 3            | Scale 1:20          |
| Prepared By Janis Webb |                     |
| Revised 11/04/06       | Grid Reference      |
| Date Issued 20/01/05   | Checked By G HAMMEL |

Lloyds Court, 78 Grey Street, Newcastle Upon Tyne, NE1 6AF

|                                                                                               |                              |
|-----------------------------------------------------------------------------------------------|------------------------------|
| LV OVERHEAD LINES<br>DRILLING AND MARKING OF WOOD<br>POLES FOR OPEN WIRE AND ABC CONSTRUCTION |                              |
| Type OVERHEAD                                                                                 | LINES                        |
| Ref No. C101820                                                                               | Historic Drg. No. 1091193301 |
| Revision                                                                                      | Notes                        |