




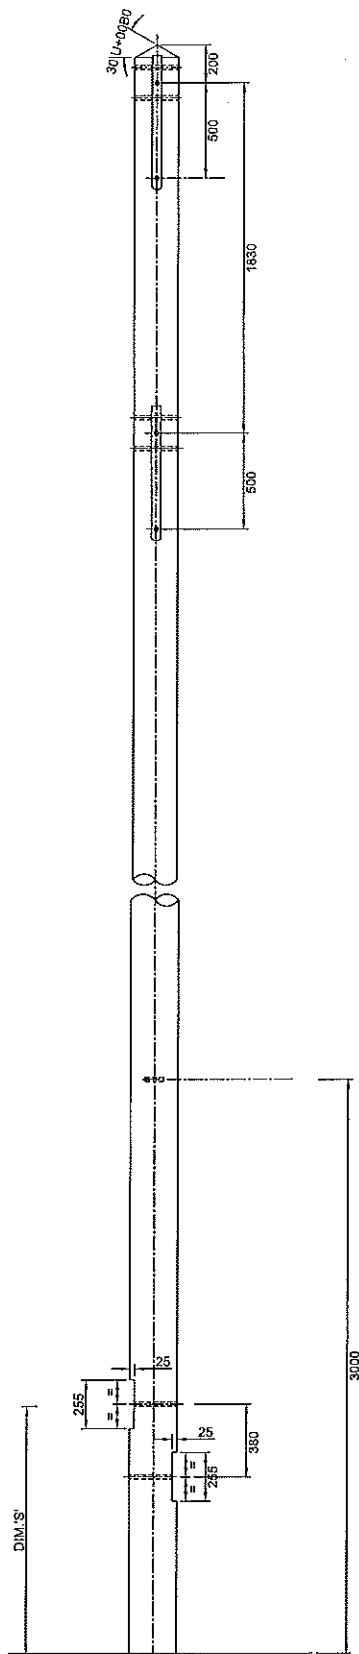

POLE SIZE TO BE IMPRESSED
ON POLE BUTT.

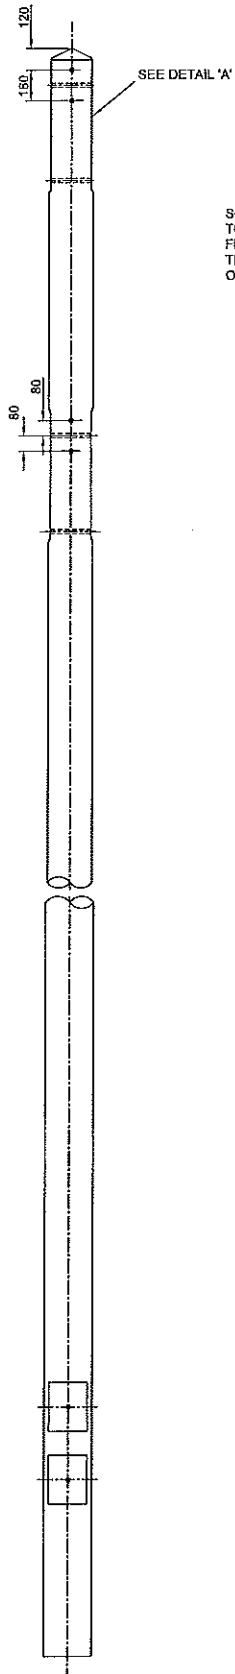

SCARFING TO BE CUT
TO GIVE A 50mm WIDE
FLAT ON BOTH SURFACES
THE ENDS CHAMFERED
OFF AS SHOWN.

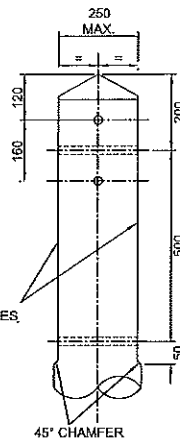

DETAIL 'A'

SCALE 1:10

NOTES:-

1. CLASS OF POLE TO BE EXTRA STOUT.
MIN. POLE HEIGHT 13m.
2. ALL HOLES TO BE 22mm DIA. DRILLED AT
RIGHT ANGLES TO VERTICAL CENTRE LINE
AND CUTTING TO BE DONE STRICTLEY TO
TEMPLATE PRIOR TO PRESERVATION
TREATMENT.
3. POLE BUTT TO BE CUT AT RIGHT ANGLES
TO AXIS OF POLE.
4. POLE TO BE NOTCHED AND DRILLED FOR
DUPLICATE 250 x 125 BAULKS.

POLE LENGTH (m)	DIM. 'S' (mm)
13 - 15 INCLUSIVE	2100
16 - 18 INCLUSIVE	2100
20	2500

**NORTHERN
POWERGRID**

Manufacturer Details

Sheet No.

Scale

Prepared By

1:20

Revised

Grid Reference

Date Issued

Checked By

Lloyds Court, 78 Grey Street, Newcastle Upon Tyne, NE1 6A

**HV OVERHEAD LINES
SINGLE POLE FABRICATION FOR
ARRANGEMENTS 1091231160 SHT5**

Type

POLES

Ref No.

C1008541

Historic

Drng.No.

1091231160

Redline

Mo/No