



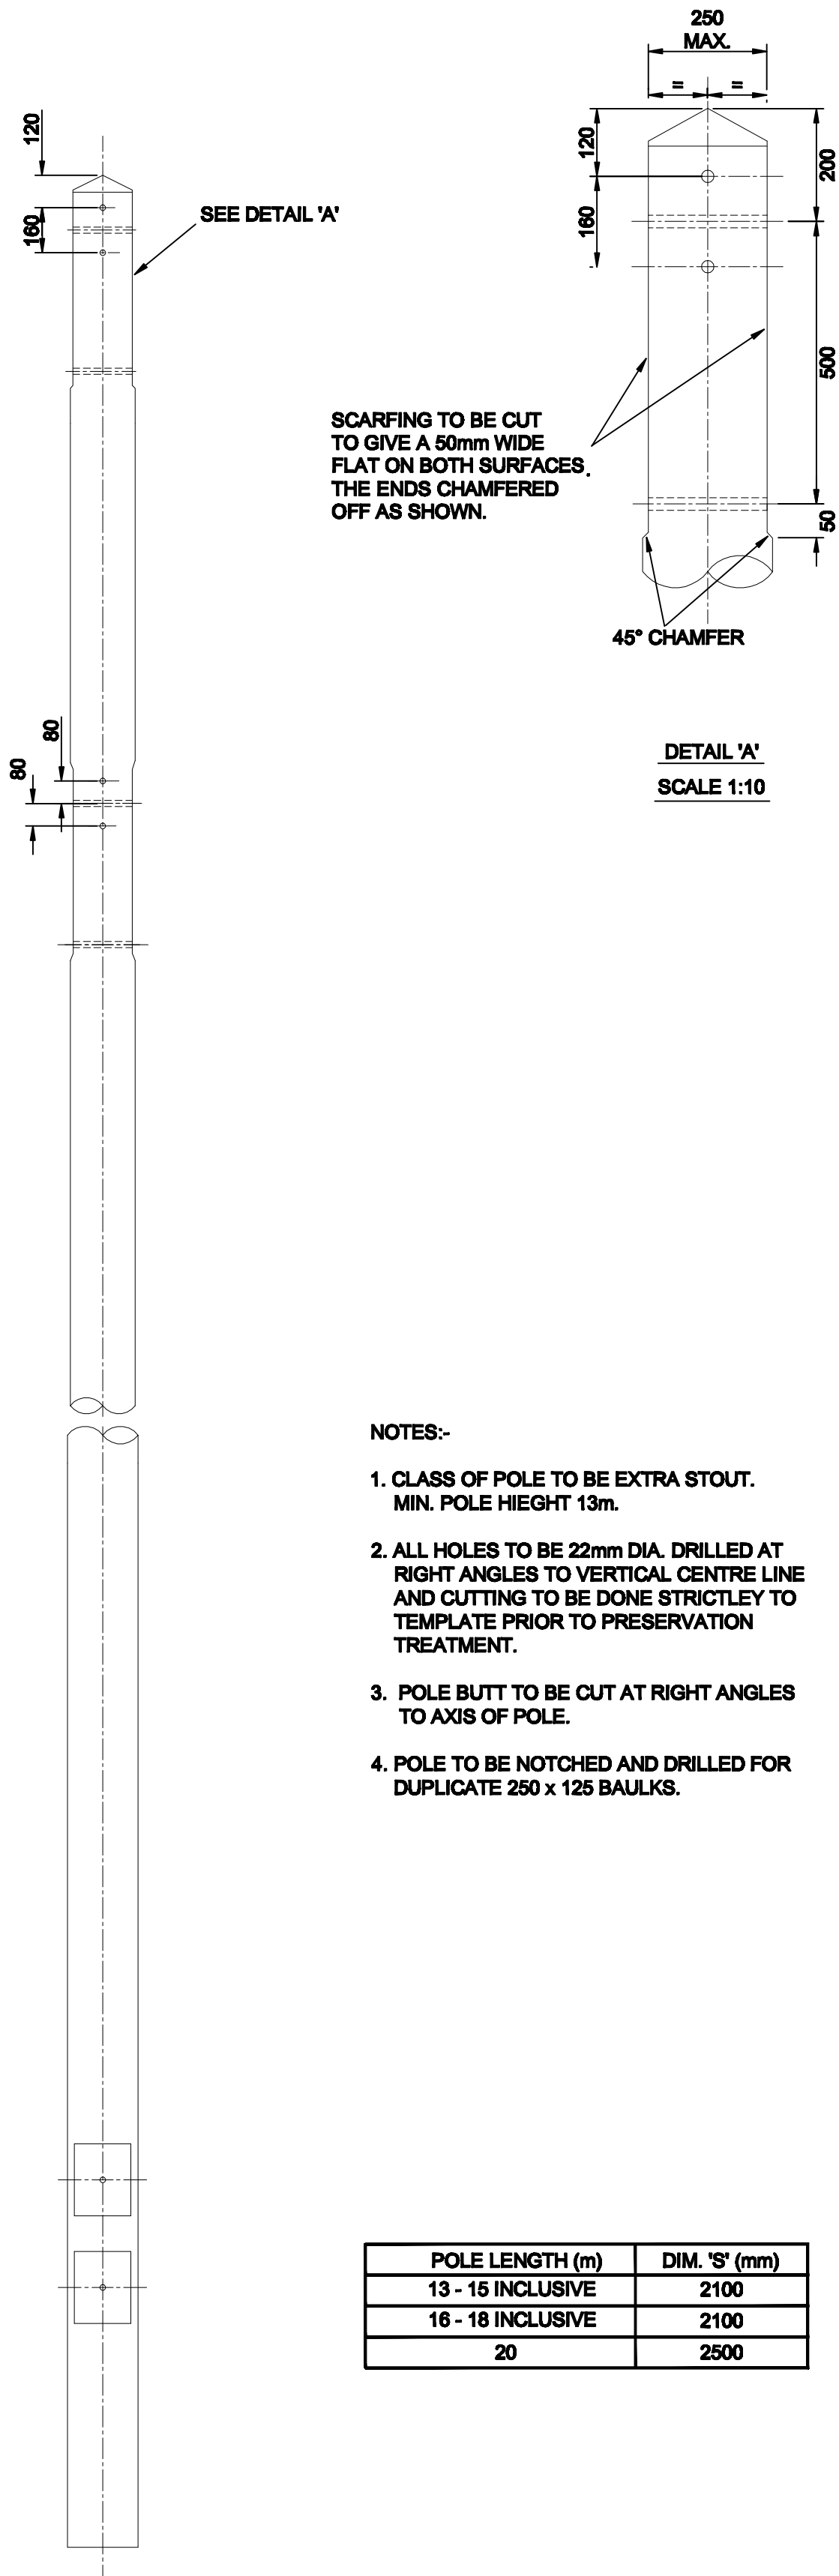

NOTES:-

1. CLASS OF POLE TO BE EXTRA STOUT.
MIN. POLE HIEGHT 13m.
2. ALL HOLES TO BE 22mm DIA. DRILLED AT RIGHT ANGLES TO VERTICAL CENTRE LINE AND CUTTING TO BE DONE STRICTLEY TO TEMPLATE PRIOR TO PRESERVATION TREATMENT.
3. POLE BUTT TO BE CUT AT RIGHT ANGLES TO AXIS OF POLE.
4. POLE TO BE NOTCHED AND DRILLED FOR DUPLICATE 250 x 125 BAULKS.

POLE LENGTH (m)	DIM. 'S' (mm)
13 - 15 INCLUSIVE	2100
16 - 18 INCLUSIVE	2100
20	2500

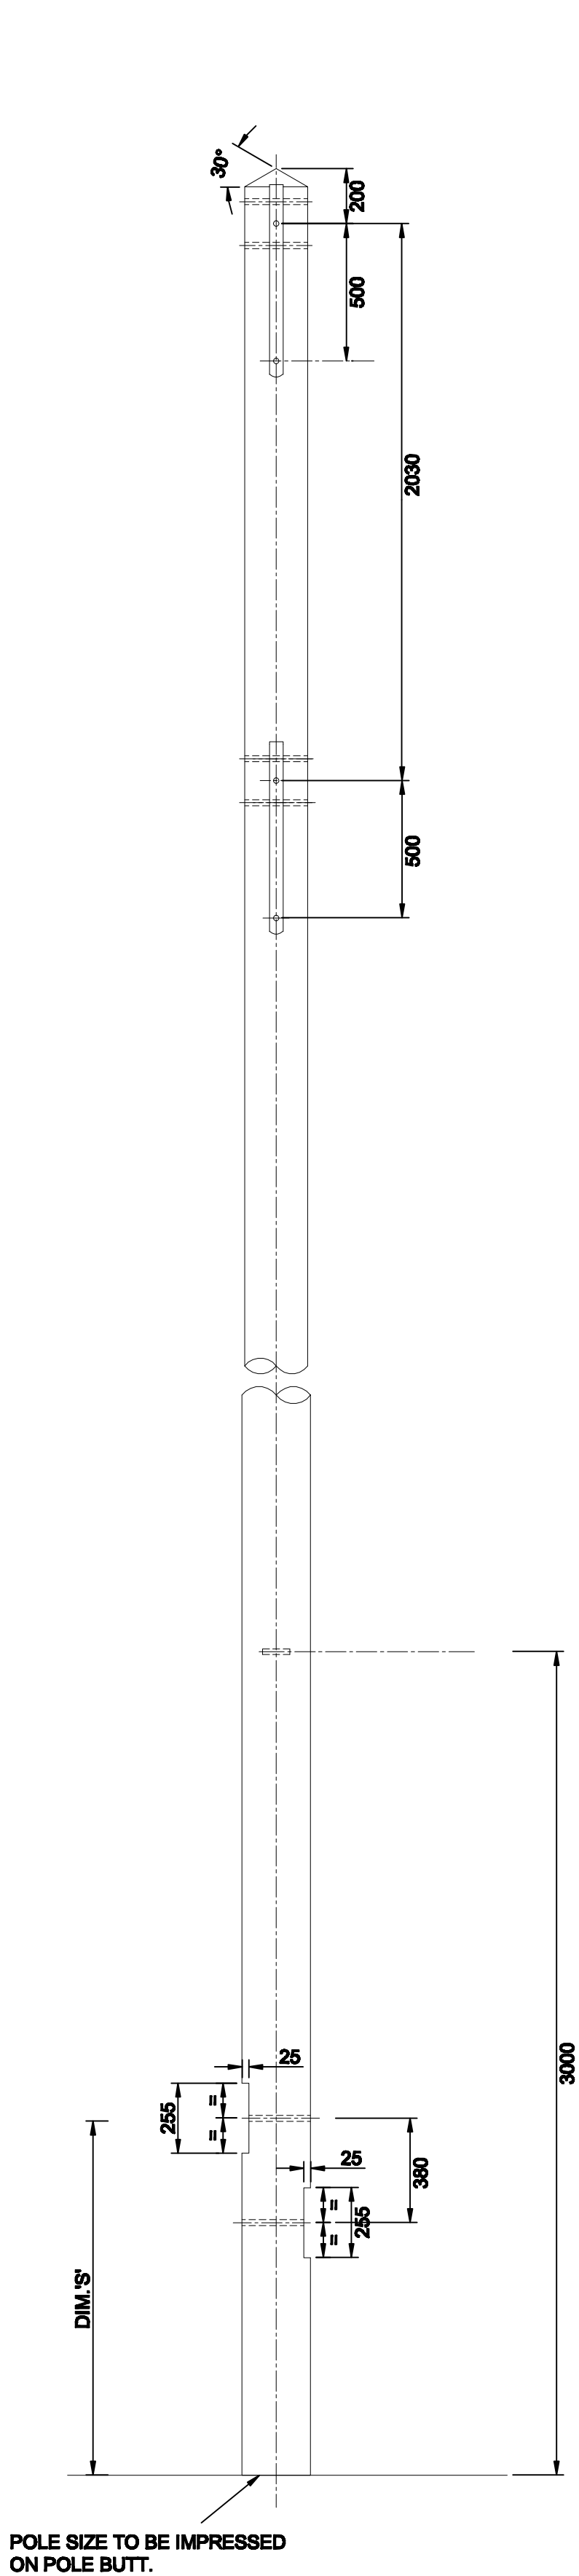

**NORTHERN
POWERGRID**

Manufacturer Details

Sheet No.
6

Scale
1:20

Prepared By
Barbara Gordon

Revised
23/08/16

Date Issued
19/04/12

Grid Reference

Checked By
G HAMMEL

Lloyds Court, 78 Grey Street, Newcastle Upon Tyne, NE1 6AF

**HV OVERHEAD LINES
SINGLE POLE FABRICATION FOR
ARRANGEMENTS 1091231160 SHT5**

Type
OVERHEAD

POLES

Ref No. C1008541

Historic
Drg.No.

1091231160

Revision B Notes