


Bird's eye view

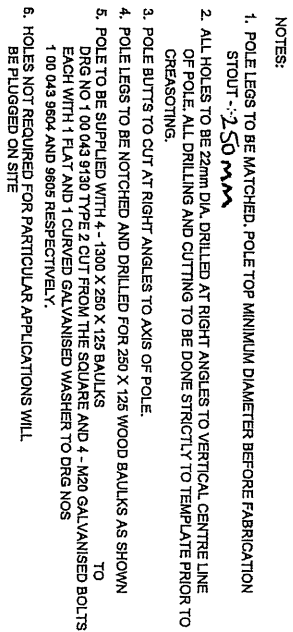

		Lloyd's Court, 78 Grey Street, Newcastle Upon Tyne, NE1 6AF 1173 1173	
Manufacturer Details Sheet No. 10 Scale 1:20 Drawn By Barbara Gordon		DRILLING SCARFING AND MARKING FOR TERMINAL SUPPORT WITH SURGE ARRESTORS AND HEAT SHRINK TERMINATION AS SHOWN ON 1.09.123.1173 SHEET 9	
Gdn Reference 0107019 Date Issued By S SALYELD 24/06/03		Ref No. C967718 Revision Notes	
Type OVERHEAD		Historic Dwg. No. 109123.1173	

ALL DIMENSIONS SHOWN ARE IN MILLIMETRES UNLESS OTHERWISE STATED

MODIFIED 1-09-123-1173 CRUCIFY
BY ABAM DESMOND 11-07-23