
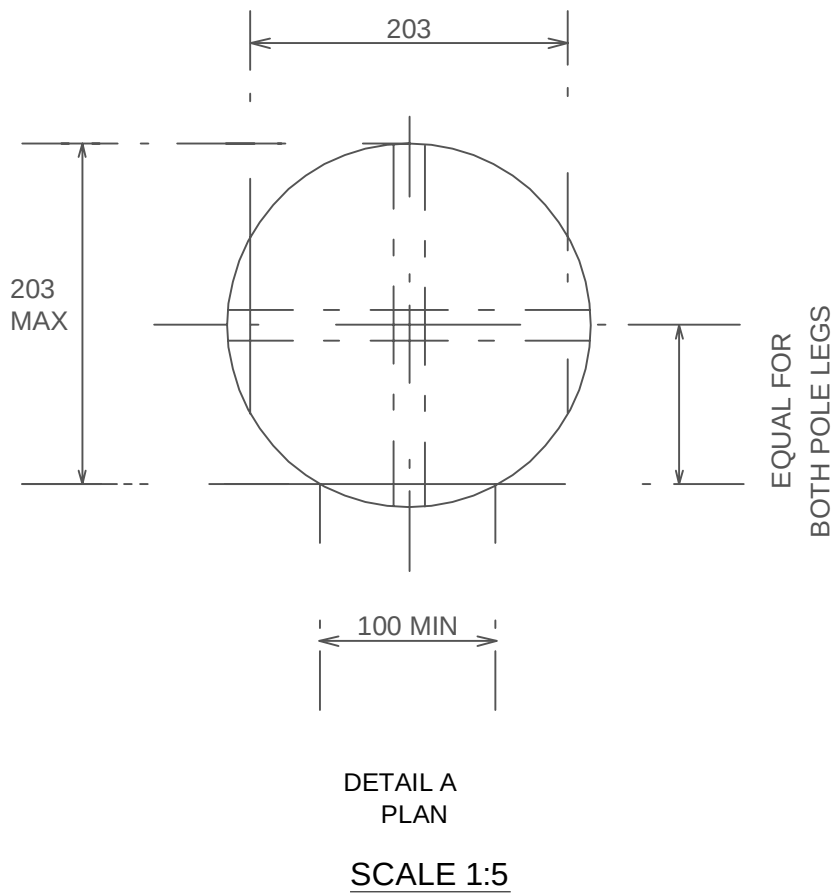
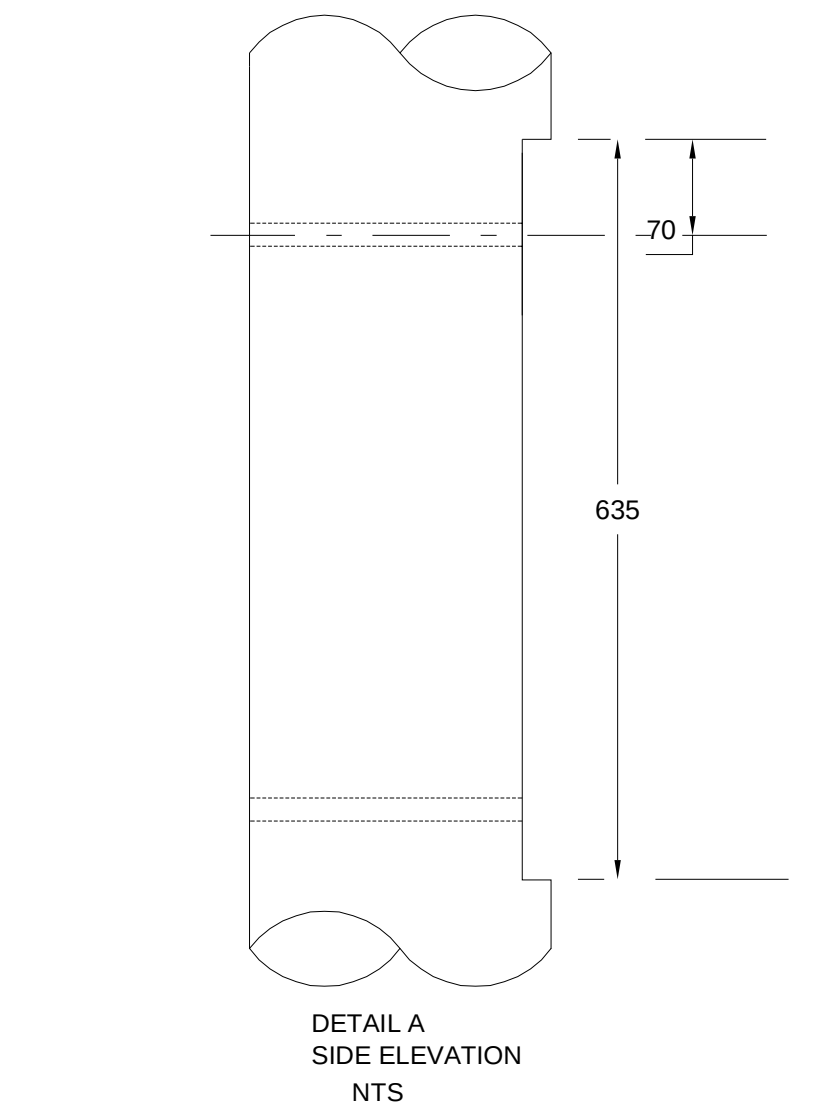
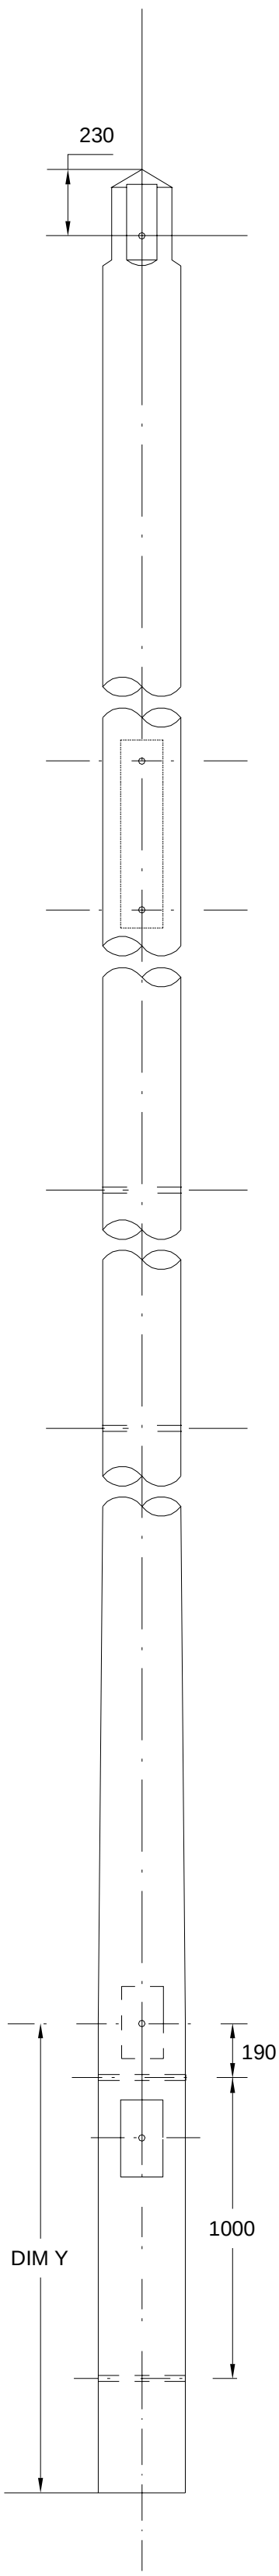


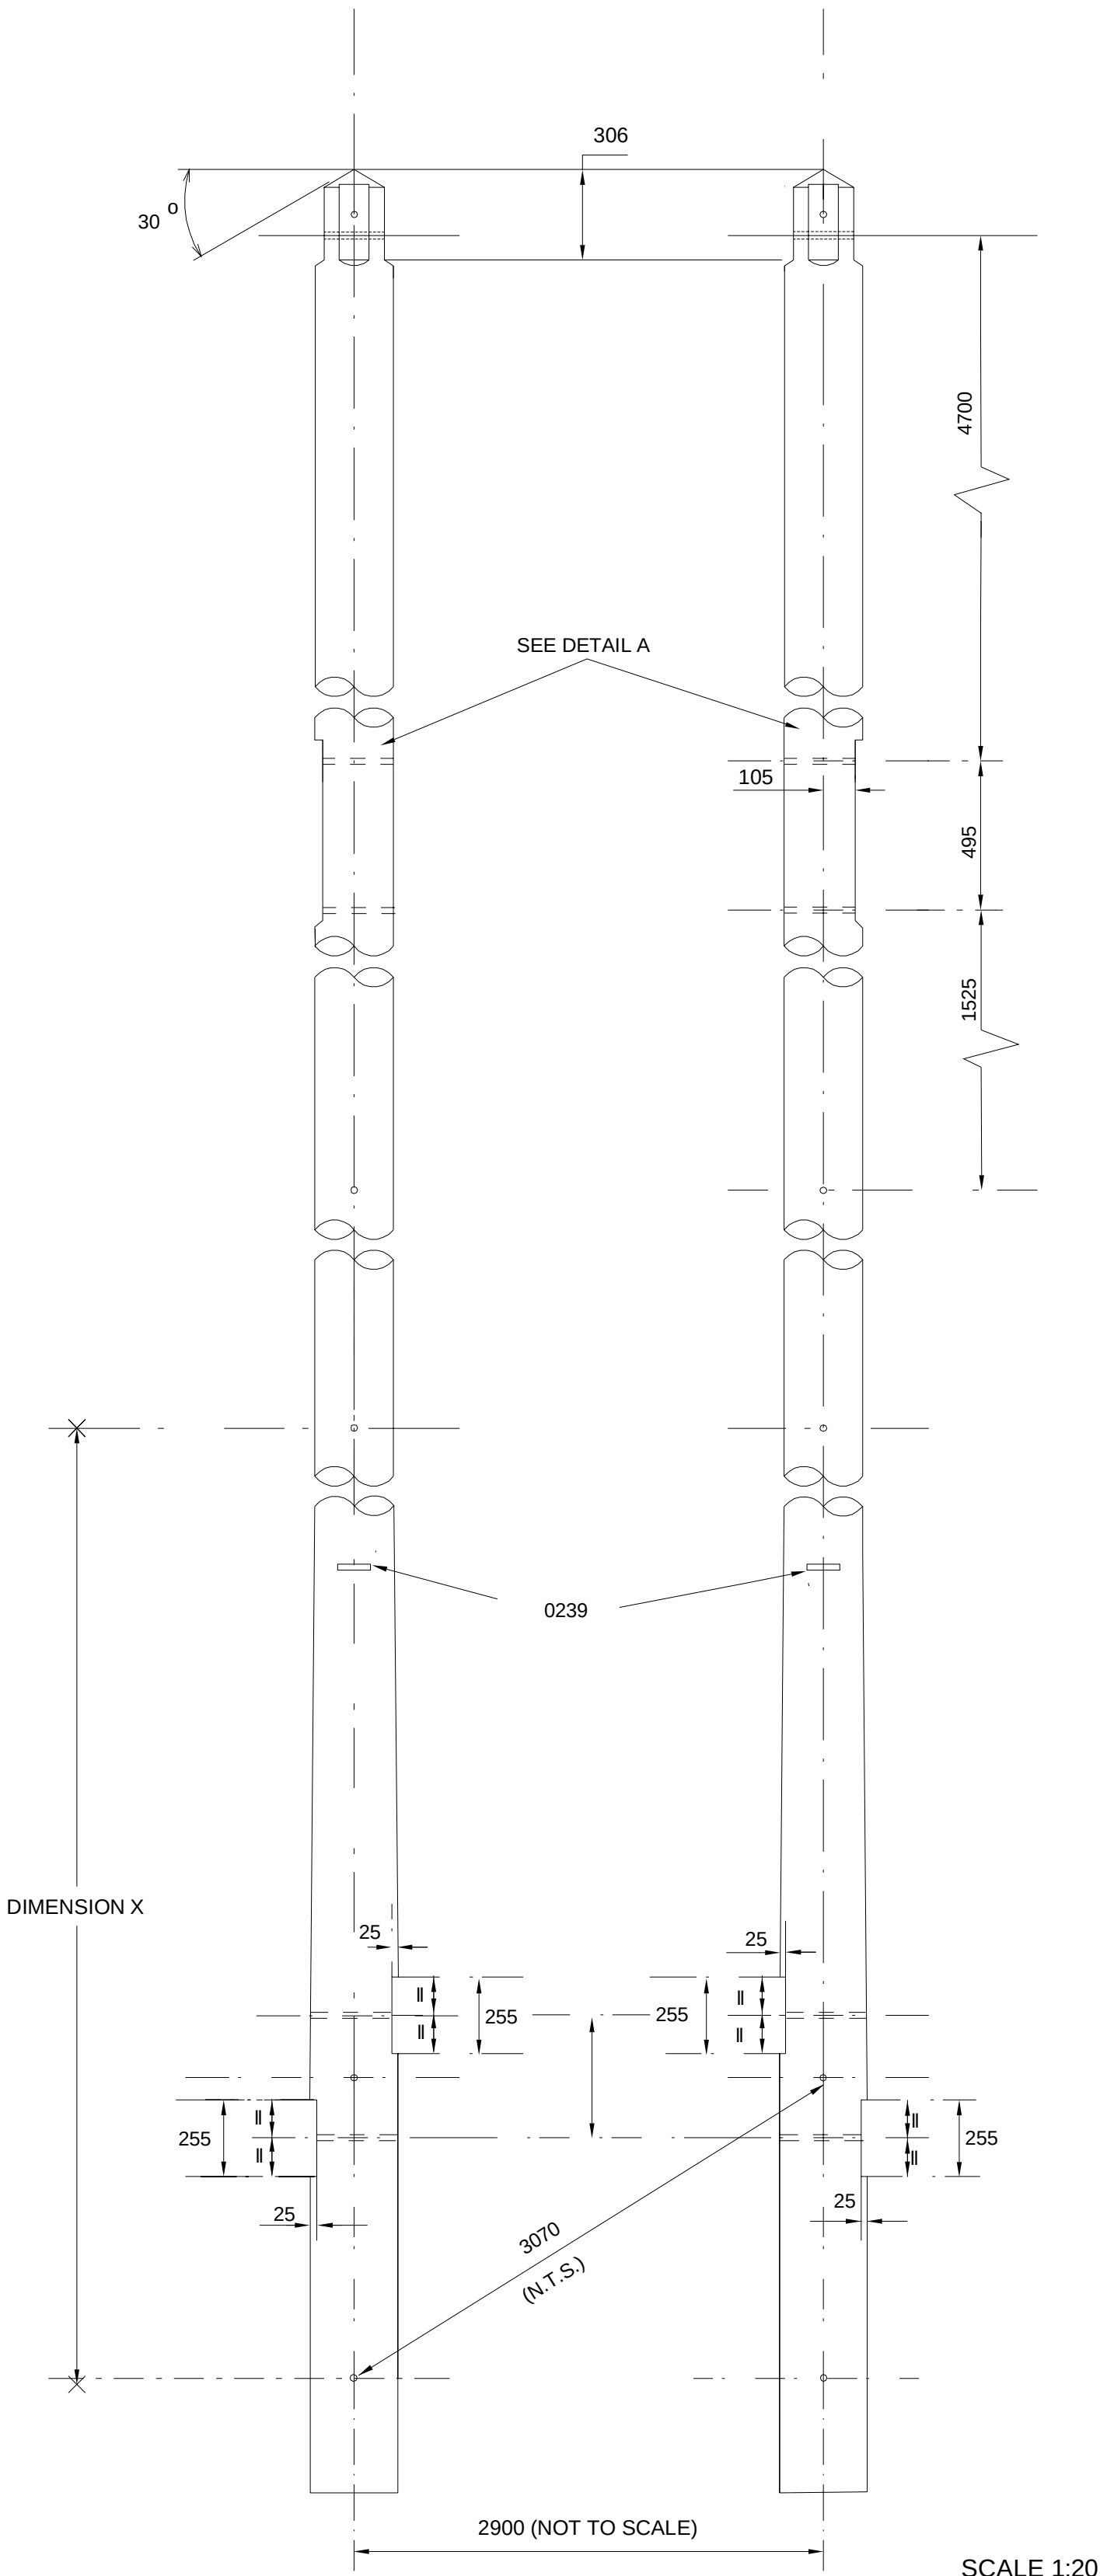

- NOTES:
- POLE LEGS TO BE MATCHED. POLE TOP MINIMUM DIAMETER BEFORE FABRICATION STOUT - 230mm
 - ALL HOLES TO BE 22mm DIA. DRILLED AT RIGHT ANGLES TO VERTICAL CENTRE LINE OF POLE. ALL DRILLING AND CUTTING TO BE DONE STRICTLY TO TEMPLATE PRIOR TO CREASOTING.
 - POLE BUTTS TO CUT AT RIGHT ANGLES TO AXIS OF POLE.
 - POLE LEGS TO BE NOTCHED AND DRILLED FOR 250 X 125 WOOD BAULKS AS SHOWN
 - POLE TO BE SUPPLIED WITH 4 - 1300 X 250 X 125 BAULKS TO DRG NO 1 00 043 9130 TYPE 2 CUT FROM THE SQUARE AND 4 - M20 GALVANISED BOLTS EACH WITH 1 FLAT AND 1 CURVED GALVANISED WASHER TO DRG NOS 1 00 043 9604 AND 9605 RESPECTIVELY.
 - HOLES NOT REQUIRED FOR PARTICULAR APPLICATIONS WILL BE PLUGGED ON SITE

ALL DIMENSIONS SHOWN ARE IN MILLIMETRES UNLESS OTHERWISE STATED

POLE LENGTH	DIM X	DIM Y
14.0m	7655	1700
15.0m	8655	1700
16.0m	9655	1900

		Lloyds Court, 78 Grey Street, Newcastle Upon Tyne, NE1 6Af			
Manufacturer Details		66KV SINGLE CIRCUIT OVERHEAD LINE DRILLING AND SCARFING FOR INTERMEDIATE SUPPORT WITH CABLE TEE FOR DRAWING NUMBER 1091231173 SHEET 1:			
Sheet No. 14	Scale AS SHOWN				
Prepared By Barbara Gordon		Type OVERHEAD		LINES	
Revised 31/03/10	Grid Reference	Ref No.	C985731	Historic Drg.No.	1091231173
Date Issued	Checked By	A			