
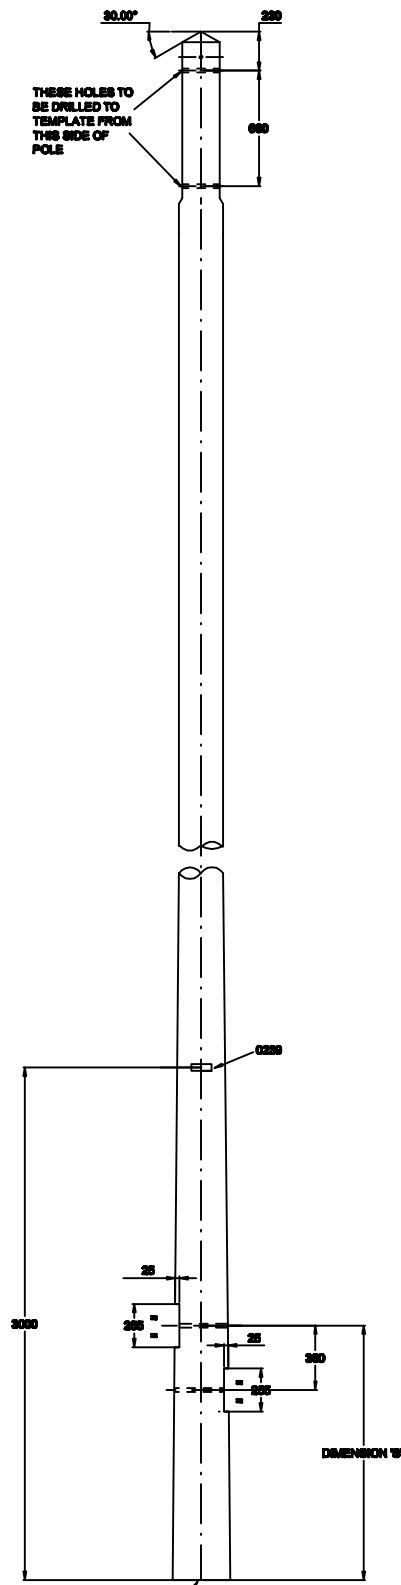


SCARFING TO BE CUT TO GIVE A 70mm WIDE FLAT ON TWO FACES THE ENDS CHAMFERED OFF AS SHOWN. BACK TO BACK BETWEEN FLAT FACES 220mm

45° CHAMFER

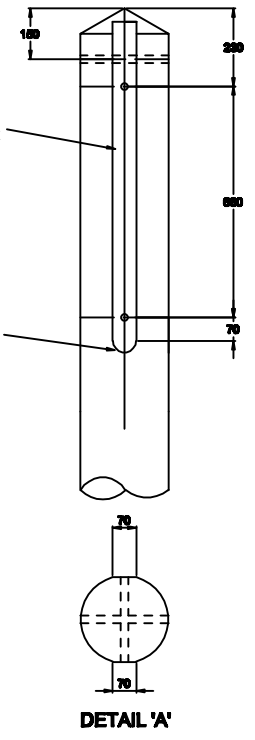

NOTES

1. CLASS OF POLE TO BE 'STOUT' OR EXTRA STOUT IN ACCORDANCE WITH 1.08.101.0288
2. POLE TO BE CUT AT RIGHT ANGLES TO AXIS OF POLE
3. ALL HOLES TO BE 22mm DIA. DRILLED AT RIGHT ANGLES TO VERTICAL CENTRE LINE OF POLE. ALL DRILLING AND CUTTING TO BE DONE STRICTLY TO TEMPLATE PRIOR TO CREOSOTING
4. POLE TO BE NOTCHED AND DRILLED FOR 1 x 250 x 125 x 2500 AND 1 x 250 x 125 x 1300 LONG BALLS

POLE LENGTH	DM 'W'
8.8m - 12.0m INCLUSIVE	1.5
12.0m - 15.0m INCLUSIVE	1.7
15.0m - 18.0m INCLUSIVE	1.9
20.0m - 24.0m INCLUSIVE	2.5

ALL DIMENSIONS SHOWN ARE IN MILLIMETRES

		NEDL, Manor House, Station Road, Houghton le Spring, DH4 7LA.	
132kV SINGLE CIRCUIT OVERHEAD LINES DRILLING, SCARFING AND MARKINGS FOR SINGLE POLE SECTION / SECTION ANGLE ARRANGMENT			
Prepared by J.L.V. Checked N.M.	Date 1 AUG 99	Dwg No. 1 09 138 0005	Sheet No. 2
Made 1		Scale 1:20,10	