


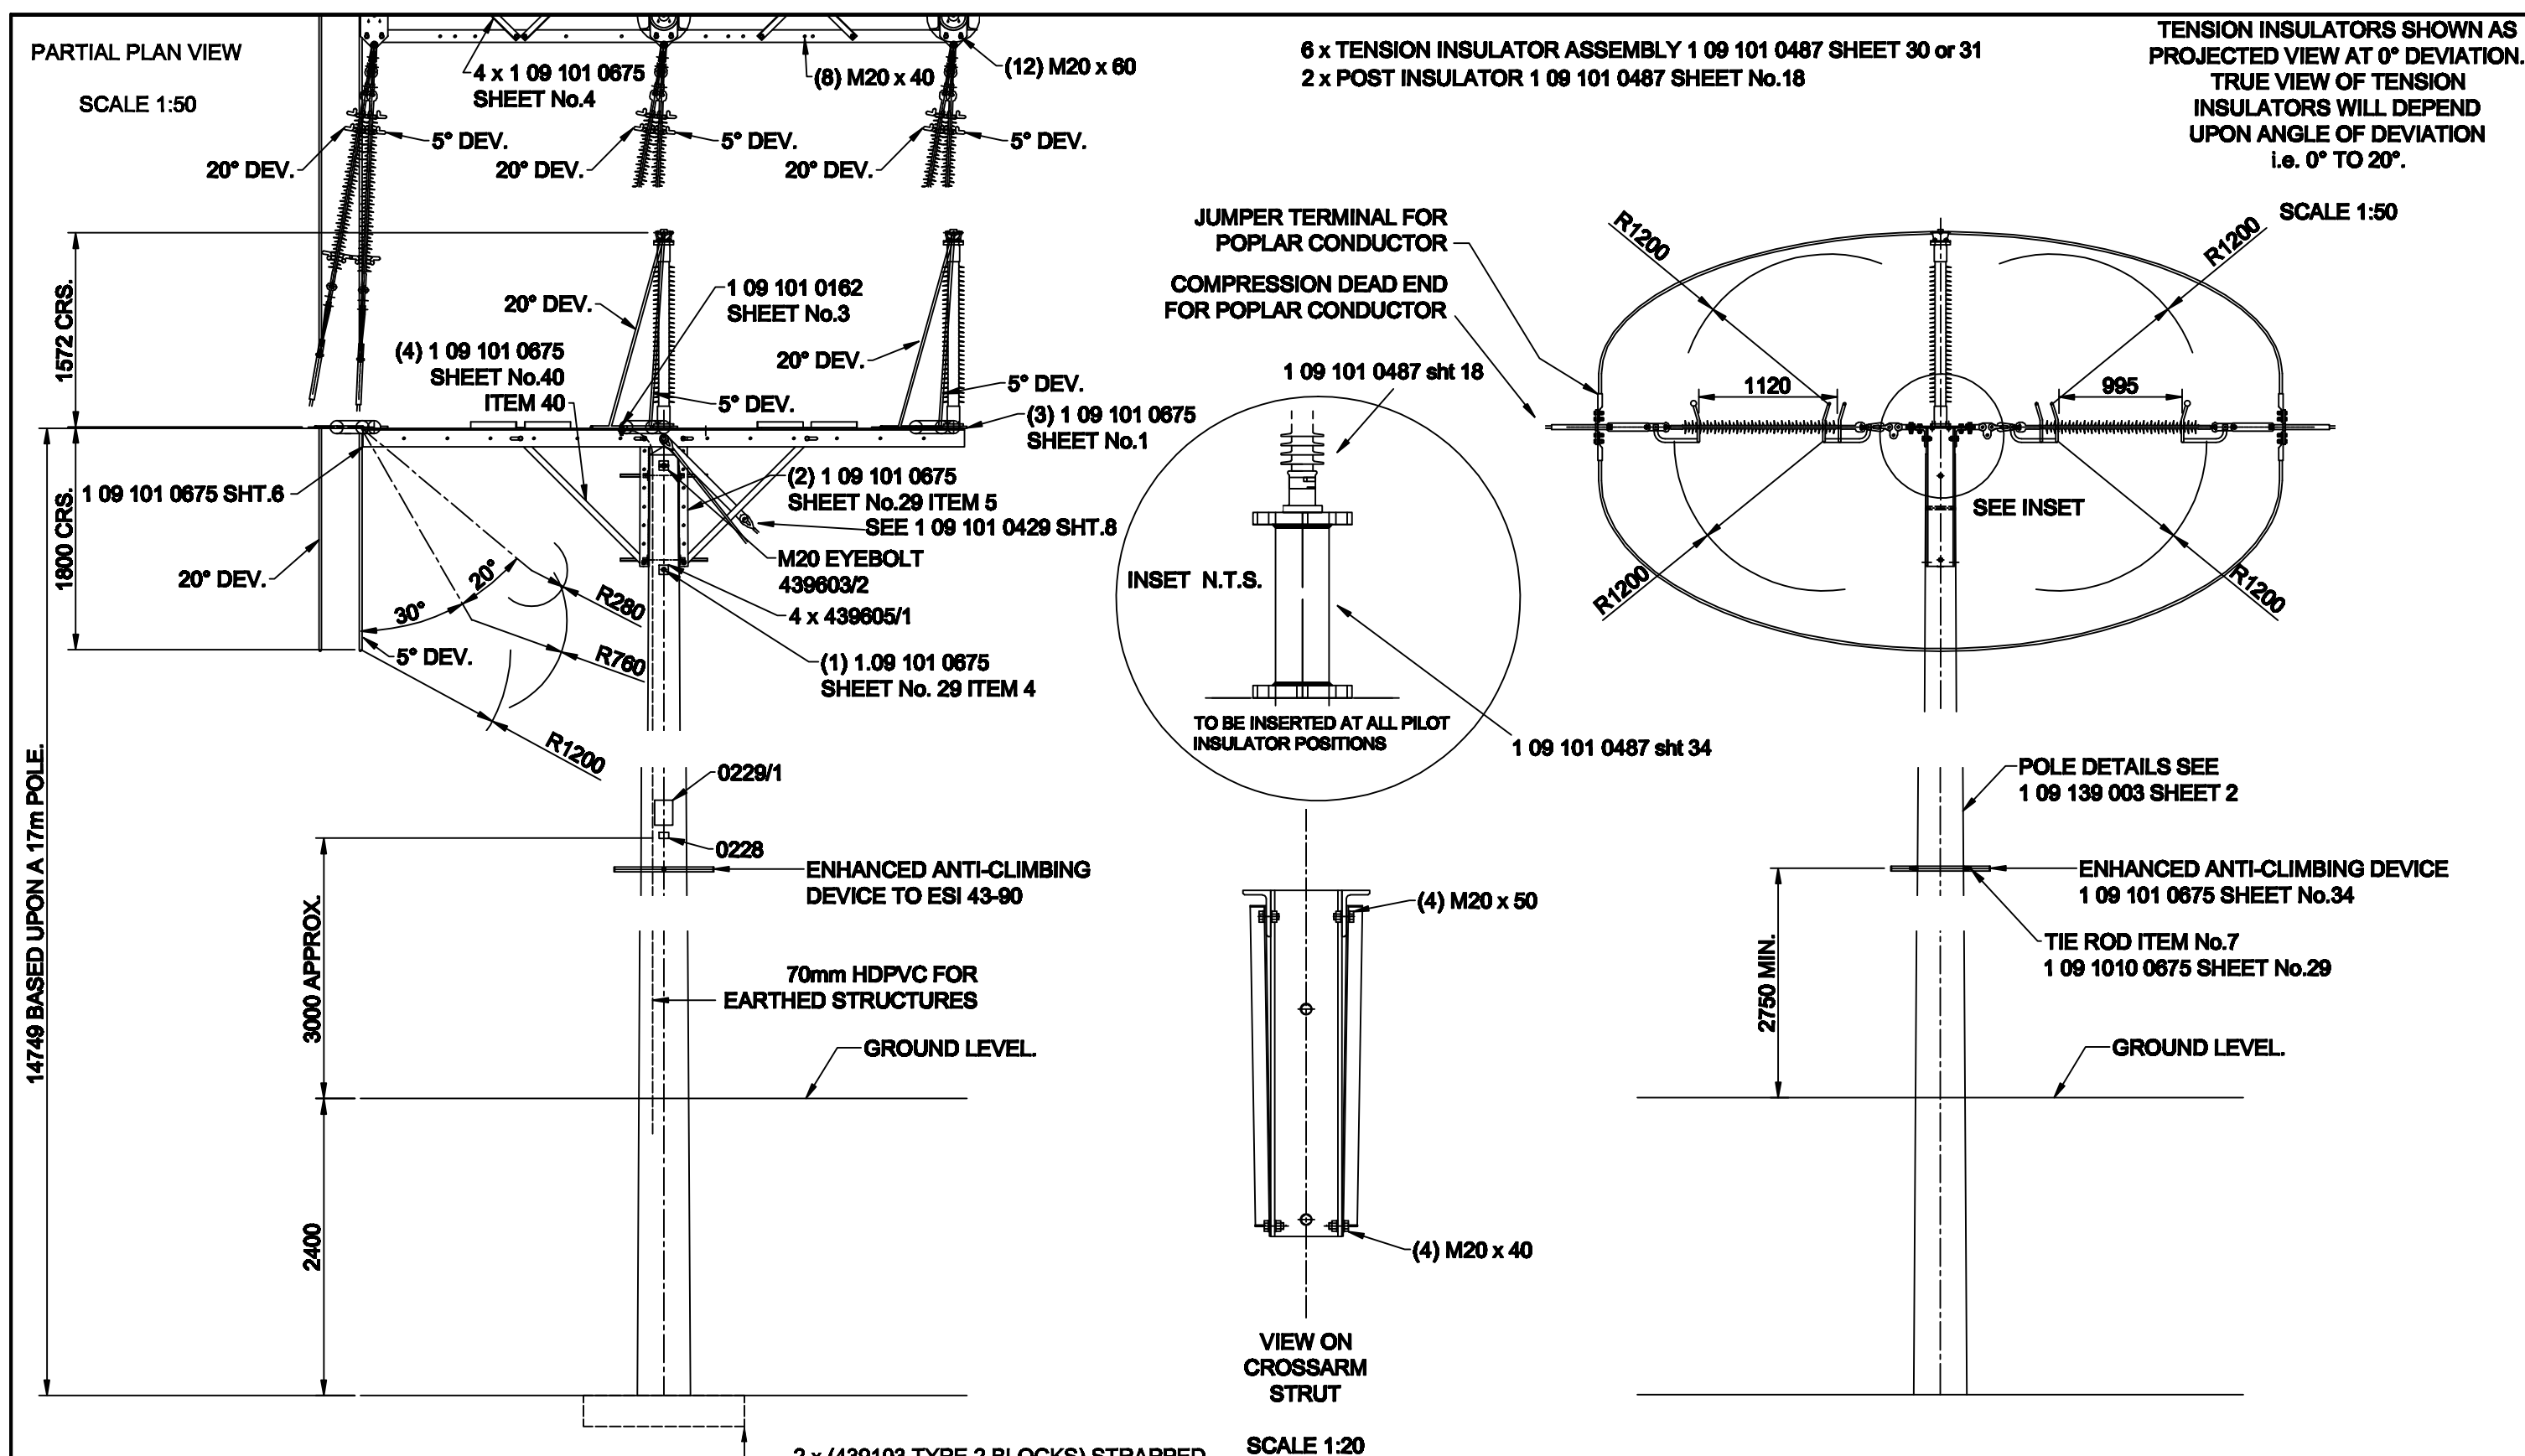

NOTES:

- ALL STEELWORK FIXINGS BOLTS TO BE COMPLETE WITH 1 ROUND WASHER UNDER BOLT HEAD & 1 ROUND WASHER UNDER NUT, UNLESS STATED OTHERWISE. WHERE A CHANNEL IS USED A 5° TAPER WASHER SHOULD BE FITTED TO LEGS ONLY.
- FOR DETAIL DRAWINGS PREFIXED 43 REFER TO E.S.I. DRAWINGS FOR OTHER DETAIL DRAWINGS REFER TO 1.09.101.0675 SERIES.
- ARCING HORN GAPS TO BE SET 995 FOR APPROACH & 1120 FOR NORMAL CONDITIONS ie 132kV.

CE Electric UK

Manufacturer Details

Sheet No.
1

Scale
1:50

Prepared By
Barbara Simpson

Revised
14/08/07

Date Issued
02/07/07

Grid Reference

Checked By
G HAMMEL

Lloyds Court, 78 Grey Street, Newcastle Upon Tyne, NE1 6AF

**132KV OVERHEAD LINES
ASSEMBLY OF SINGLE POLE
DEVIATION 2 DEGREES - 20 DEGREES
USING COMPRESSION TERMINALS**

Type
OVERHEAD

DOCUMENT SUB CLASS

Ref No. C949727

Historic
Drg.No.

1091390013

Revision B Notes