


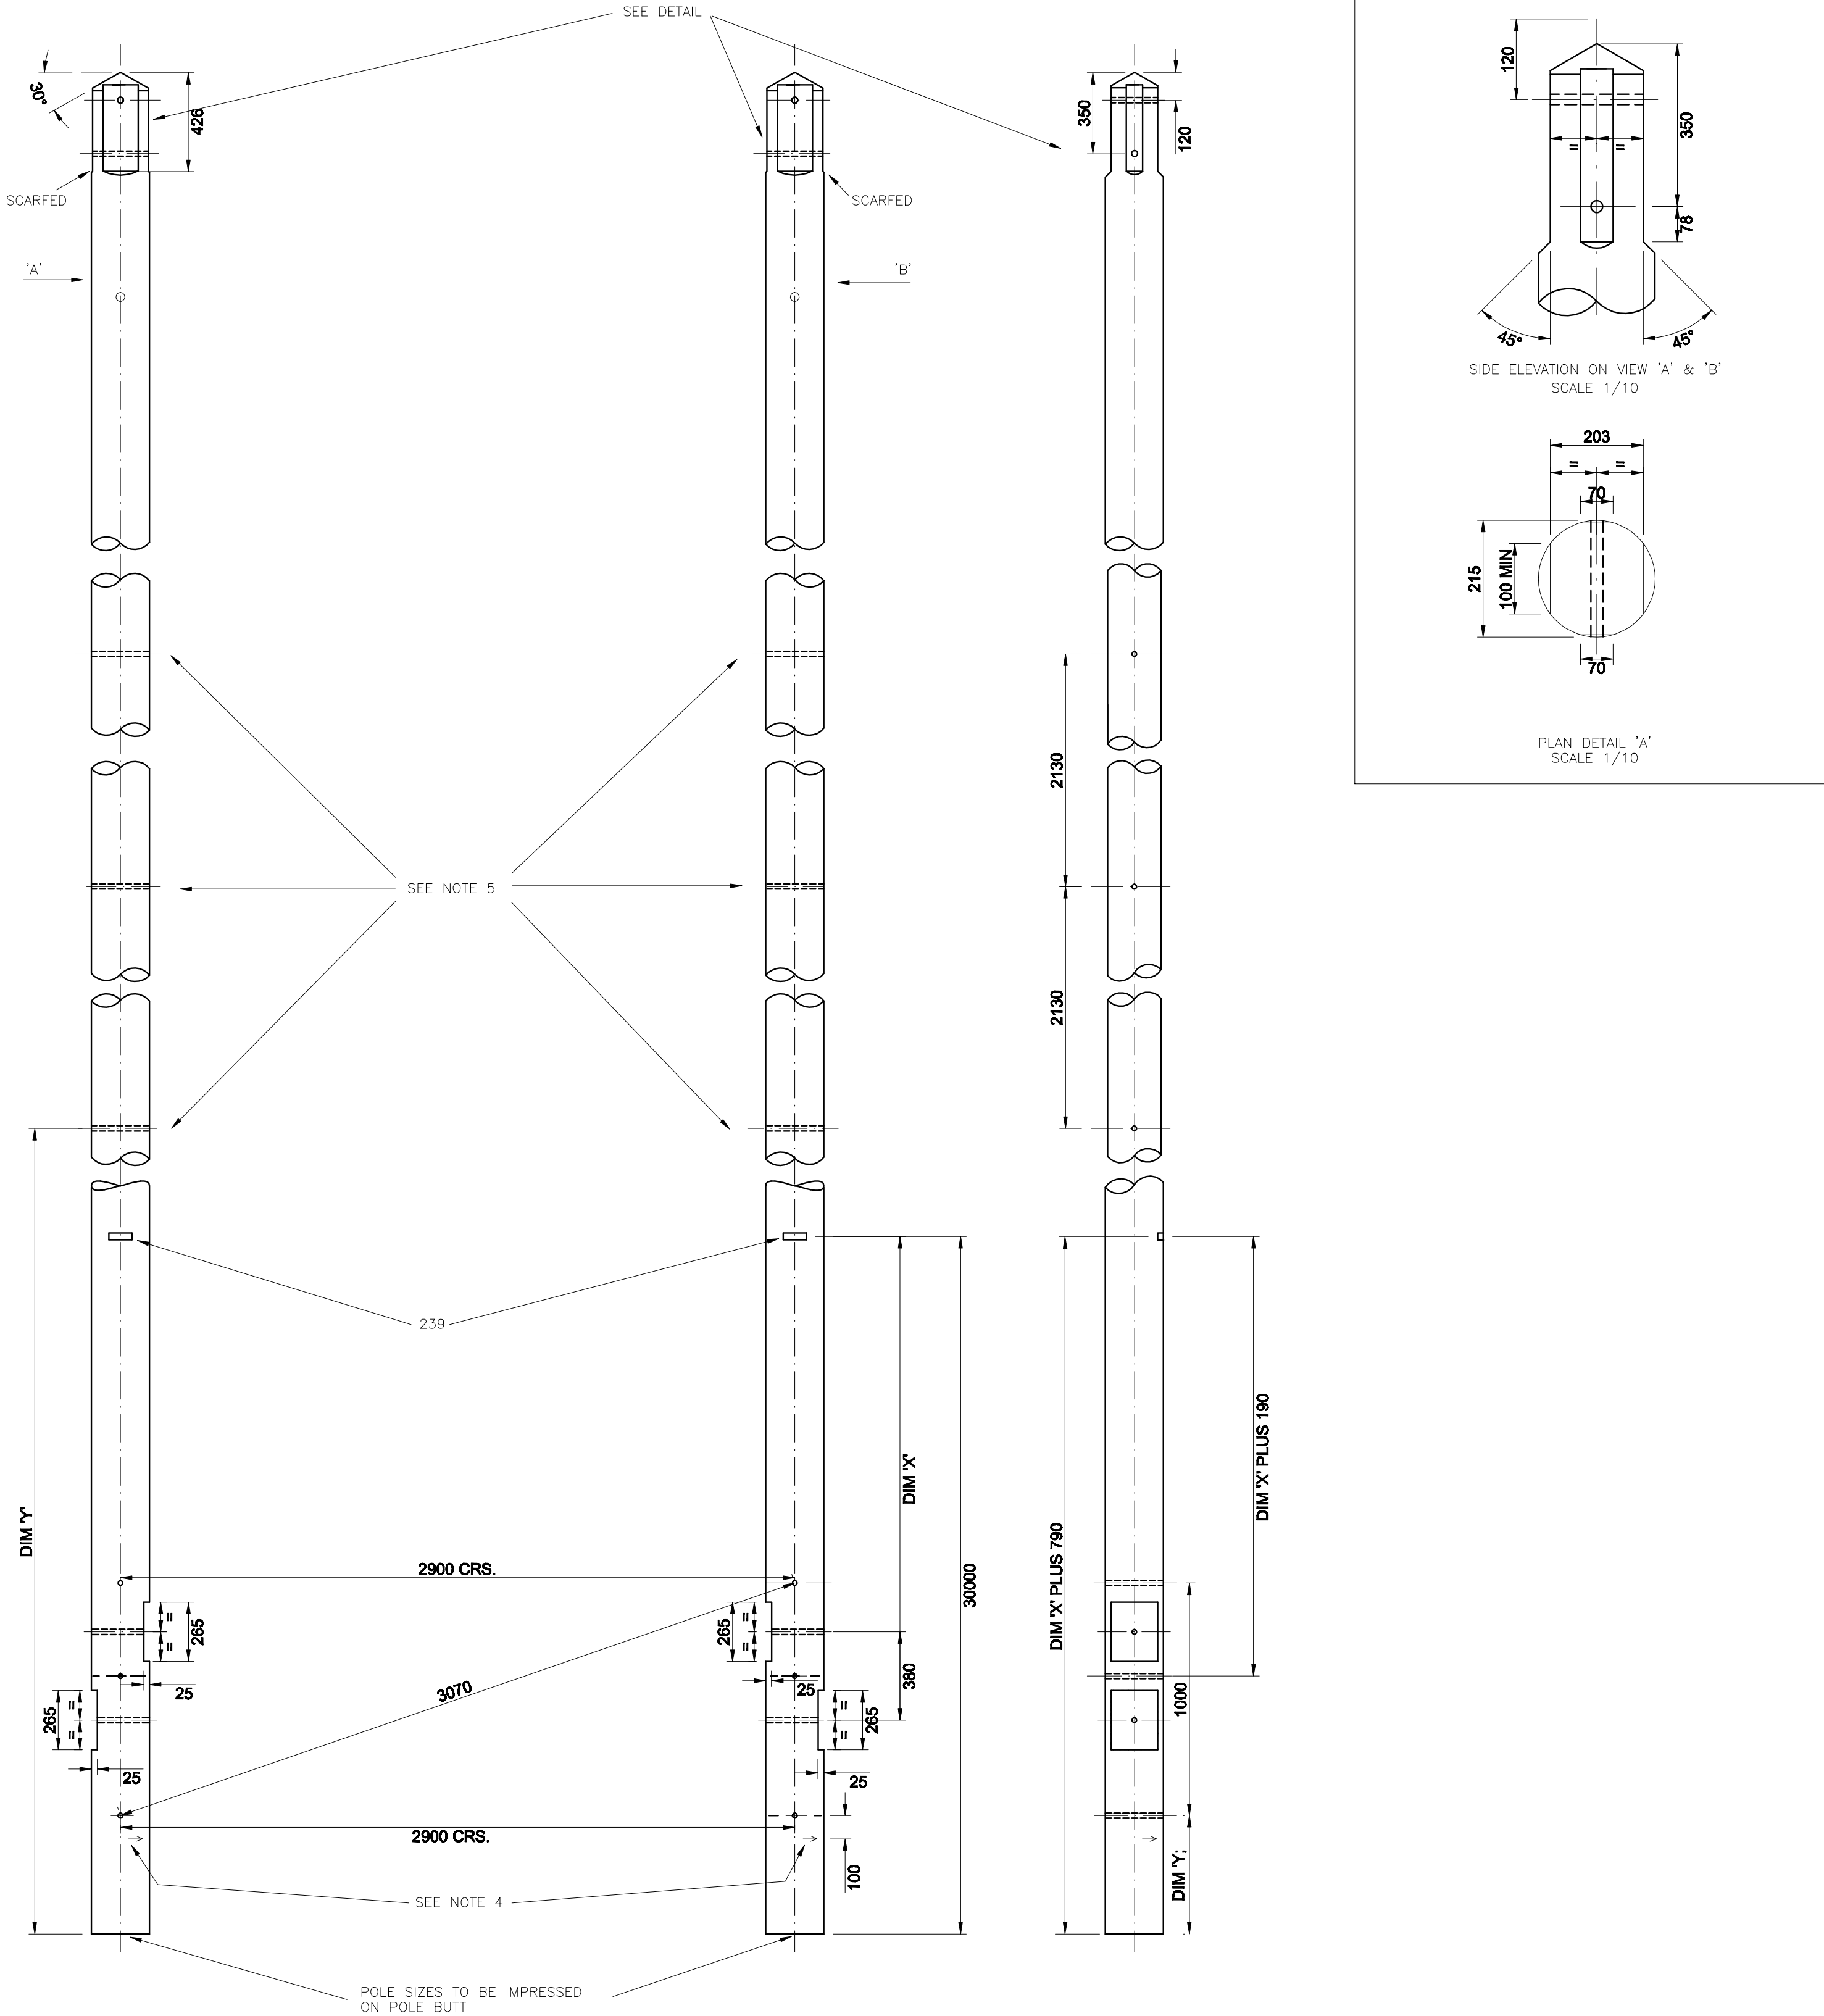

NOTES

- POLE LEGS TO BE MATCHED. POLE TOP MINIMUM DIAMETER BEFORE FABRICATION E/STOUT – 226mm.
- HOLES TO BE 22mm DIA. DRILLED AT RIGHT ANGLES TO VERTICAL CENTRE–LINE OF POLE. ALL DRILLING AND CUTTING TO BE DONE STRICTLY TO TEMPLATE PRIOR TO CREOSOTING.
- POLE BUTTS CUT AT RIGHT ANGLES TO AXIS OF POLE.
- 50x6x6 DEEP ARROW MARK POINTING TOWARDS OPPOSITE POLE LEG TO BE GOUGED ON BRACE BLOCK NOTCHING.
- 'H' POLES 18.0m AND OVER TO BE SUPPLIED COMPLETE WITH A DOUBLE PANEL OF CROSSBRACING TO DRG.No. 1.09.101.0129.

All dimensions shown are in millimetres unless stated otherwise

POLE LENGTH. (m)	DIM. 'X' (mm)	DIM. 'Y' (mm)
9.0 - 11 INCLUSIVE.	1900	-
12.0	1700	-
13 - 15 INCLUSIVE.	1400	-
16 - 18 INCLUSIVE.	1100	7955
20	500	

NORTHERN POWERGRID Manufacturer Details Sheet No. 2 Scale 1:20 Prepared By Joan.Oakley Revised 19/06/13 Date Issued 19/06/13 Checked By G HAMMEL		Lloyds Court, 78 Grey Street, Newcastle Upon Tyne, NE1 6AF	
		132KV SINGLE CIRCUIT OVERHEAD LINES DRILLING, SCARFING & MARKING FOR LARGE ANGLE 'H' POLE STRUCTURE	
		Type OVERHEAD	STANDARDS
Ref No. C1023988		Historic Drg.No.	1091390018
Revision F		Notes	