
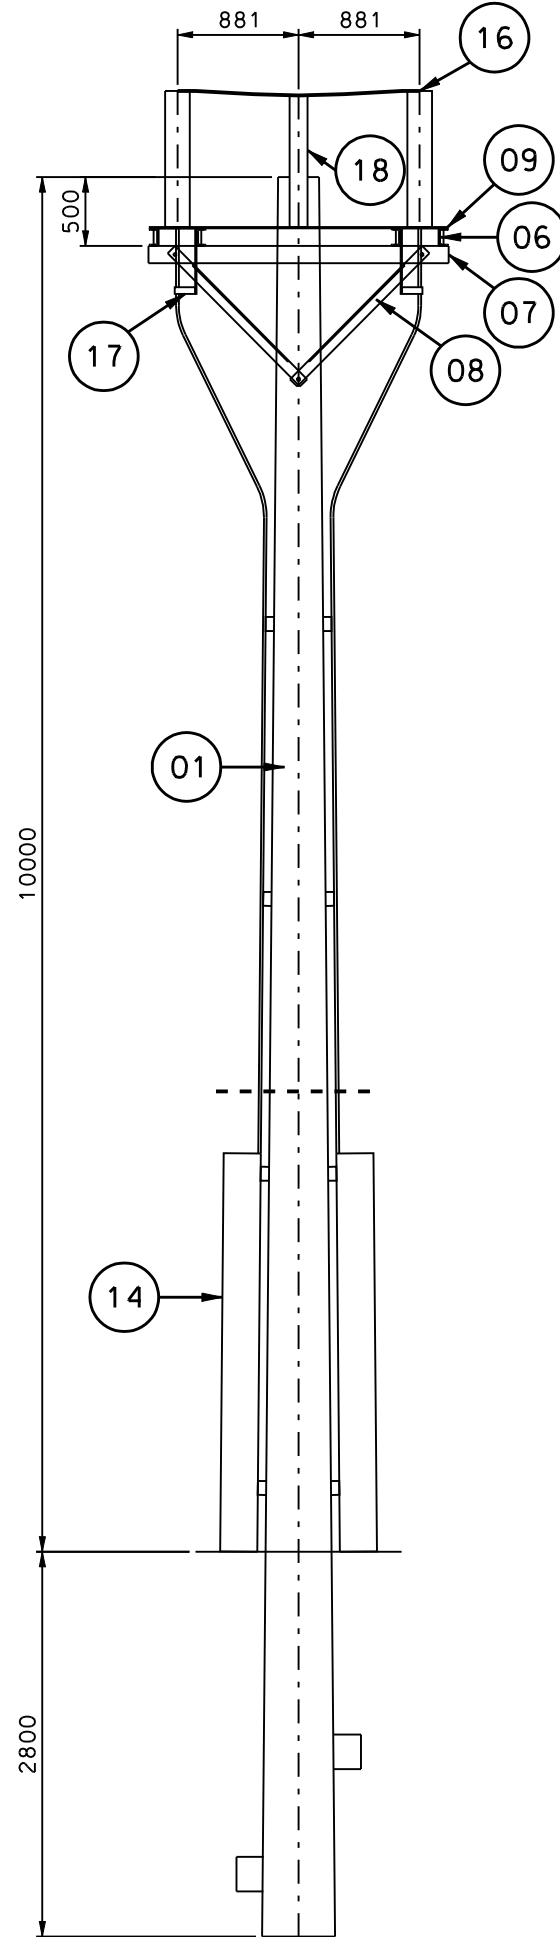


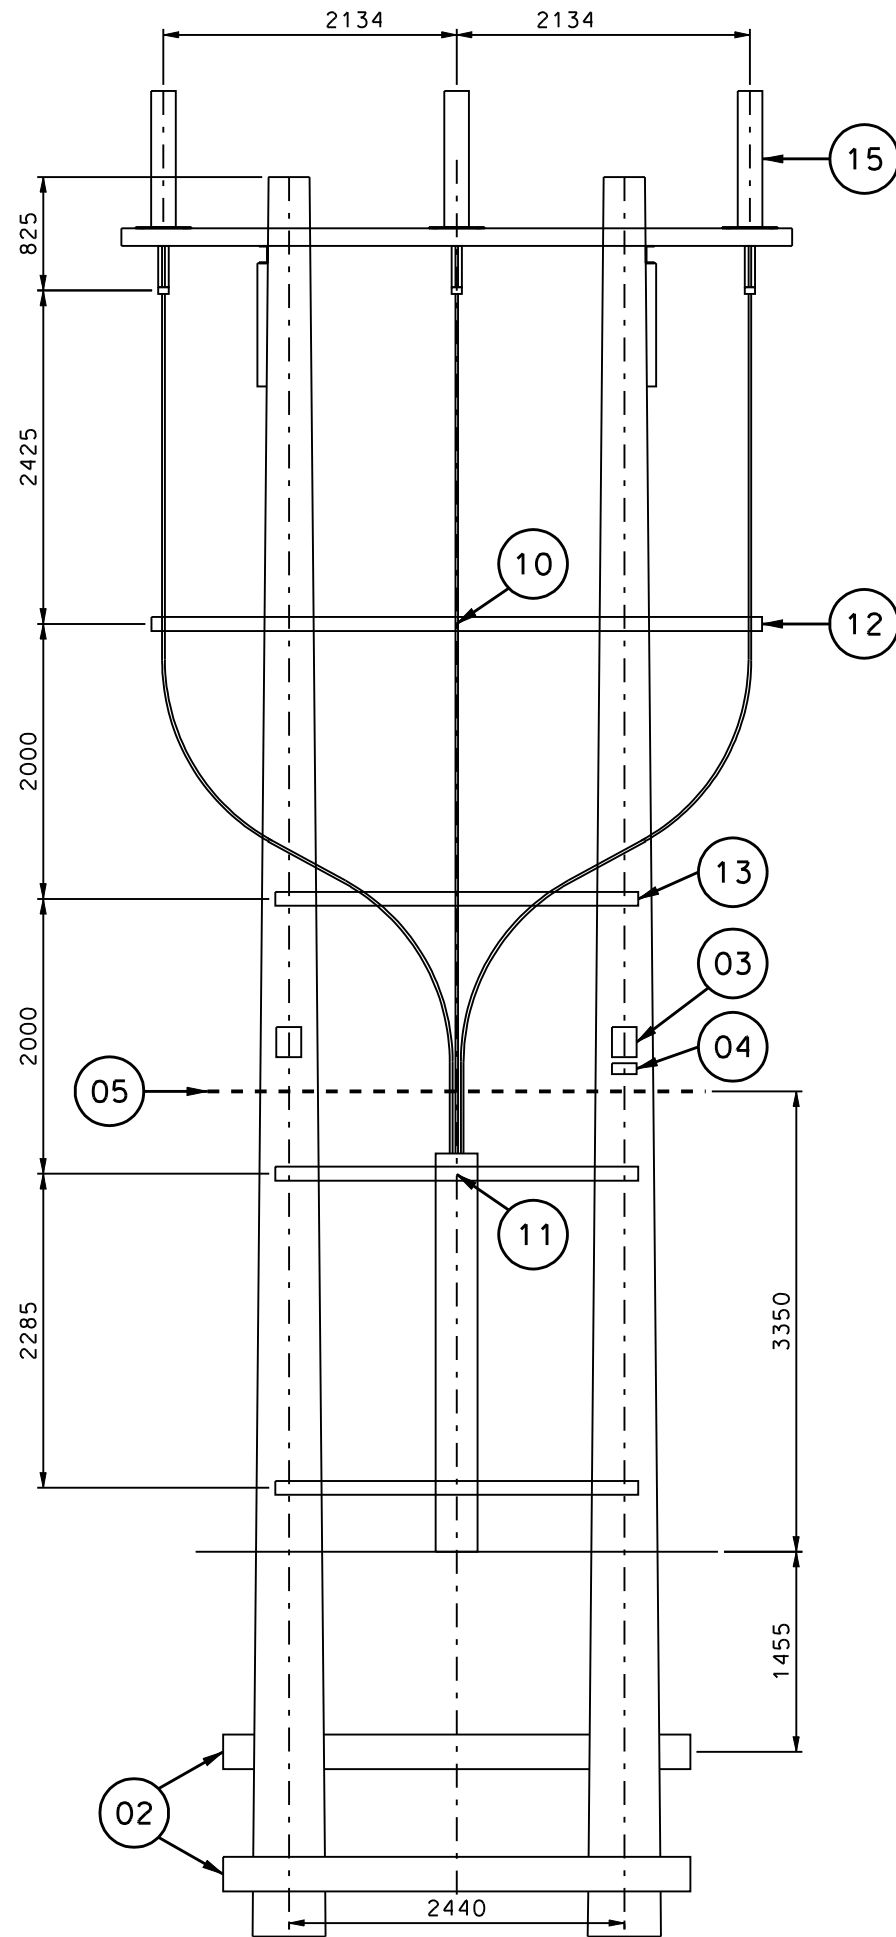

MATERIAL LIST

ITEM	No. OFF	DESCRIPTION	DRAWING No./REF	ITEM	No. OFF	DESCRIPTION	DRAWING No./REF
01	2	WOOD POLE	10412-MWF-006	10	9	SINGLE CLEAT	Y204L0915
02	2	BRACE BLOCK	Y204L0301	11	3	TREFOIL CLEAT	Y204L0915
03	4	SAFETY SIGN	Y201L1002	12	2	CABLE SUPPORT - LONG	Y204L0917/2
04	2	OPERATIONAL PLATES	Y201L1001/7	13	6	CABLE SUPPORT - SHORT	Y204L0917/3
05	1	ANTI-CLIMBING GUARD	Y201L1102	14	2	CABLE GUARD	Y204L0911
06	4	SEALING END PLATFORM - CROSSARM	Y204L0918/1	15	6	SEALING END	TBA
07	2	SEALING END PLATFORM - SUPPORT	10412-MWF-004/1	16	6	BI-METAL CONNECTOR & JUMPER PALM	TBA
08	4	SEALING END PLATFORM - STRUTT	Y204L0918/3	17	6	HANGING CABLE SUPPORT	10412-MWF-004/3
09	3	SEALING END PLATE	10412-MWF-004/2	18	3	SURGE ARRESTOR	TBA

THIS DRAWING WAS PRODUCED USING MICROSTATION AND SHOULD ON NO ACCOUNT BE AMENDED BY HAND				
REV 01	DATE 23/08/12	BY SS	CHKD MS	APPD SS
DESCRIPTION MATERIAL LIST DETAILS ADDED				
REV 02	DATE 18/09/12	BY SS	CHKD MS	APPD SS
DESCRIPTION AMENDED INLINE WITH CLIENTS COMMENTS				
REV 03	DATE 01/10/12	BY SS	CHKD MS	APPD SS
DESCRIPTION CROSSARM LEVEL RAISED				
REV 04	DATE 08/10/12	BY SS	CHKD MS	APPD SS
DESCRIPTION WOOD POLE DRAWING No. AMENDED				
THIS DRAWING IS THE PROPERTY OF INTERSERVE INDUSTRIAL SERVICES LTD (THE COMPANY) AND MUST NOT BE COPIED OR REPRODUCED WITHOUT THE COMPANY'S WRITTEN CONSENT. THE DRAWING IS TO BE USED ONLY FOR THE PURPOSE FOR WHICH IT IS SUPPLIED AND MUST BE TREATED AS STRICTLY CONFIDENTIAL AND MUST NOT BE DISCLOSED TO ANY THIRD PARTY WITHOUT THE COMPANY'S WRITTEN CONSENT.				
CLIENT NORTHERN POWER GRID				
PROJECT MIDDLEMOOR WINDFARM				
TITLE GENERAL ARRANGEMENT ISOLATION POLE				
SCALE NTS		ORIGINAL SIZE A3		
DATE 19/07/12		CHECKED SS		
DRAWN SA		APPROVED SS		
 INTERSERVE INDUSTRIAL SERVICES LTD. POWER DIVISION CRABTREE MANORWAY SOUTH BELVEDERE, KENT DA17 6BH TEL: 02083 209560 FAX: 02083 102016 Interserve				
DRAWING NUMBER 10412-MWF-003				REV 04