


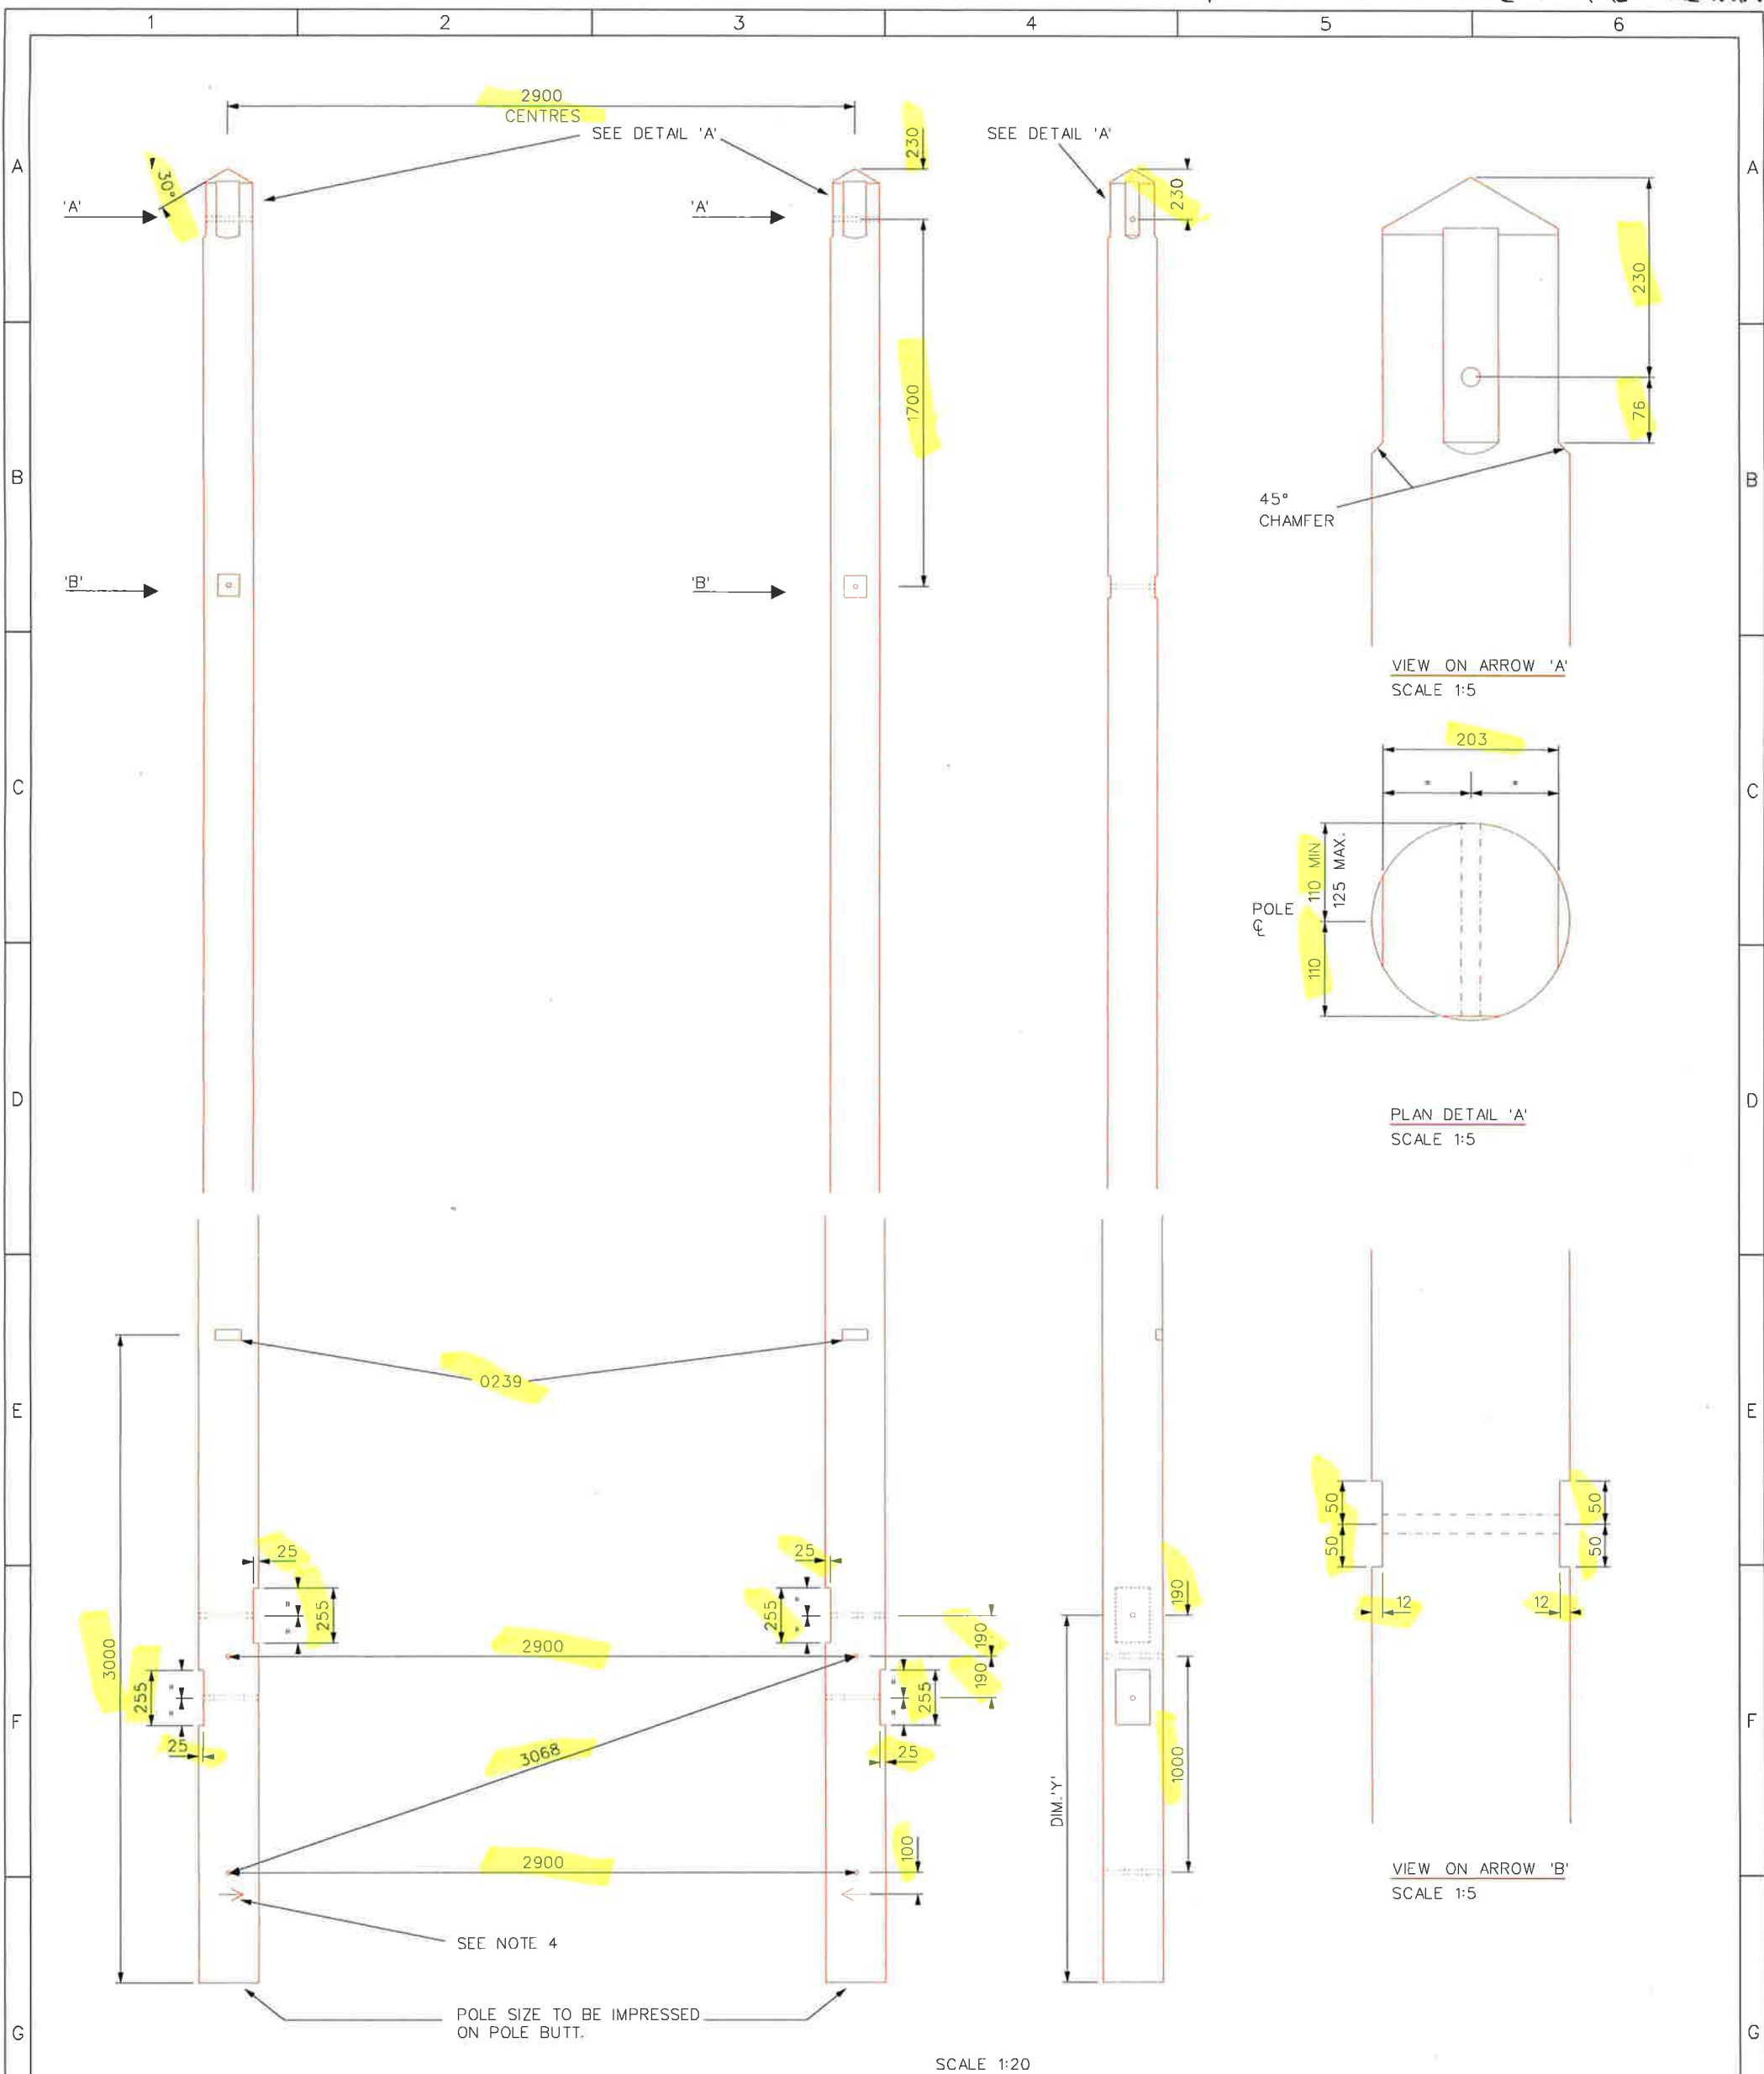

NOTES:

- POLE LEGS TO BE MATCHED. POLE TOP MINIMUM DIAMETER BEFORE FABRICATION 'STOUT' - 220mm. **OR 250mm AS ORDERED**
- ALL HOLES TO BE 22mm DIA. DRILLED AT RIGHT ANGLES TO VERTICAL CENTRE LINE OF POLE. ALL DRILLING AND CUTTING TO BE DONE STRICTLY TO TEMPLATE PRIOR TO PRESERVATION TREATMENT.
- POLE BUTTS TO BE CUT AT RIGHT ANGLES TO AXIS OF POLE. POLES TO BE NOTCHED AND DRILLED FOR DUPLICATE 250 X 125 BAULKS.
- 50 X 6 X 6 DEEP ARROW MARK POINTING TOWARDS OPPOSITE POLE LEG TO BE GOUGED ON POLE FACE.

ALL DIMENSIONS SHOWN ARE IN MILLIMETRES UNLESS OTHERWISE STATED.

* UP TO AND INCLUDING 12.0m 1500

POLE LENGTH (m)	DIM 'Y' (mm)
13 - 15 INCLUSIVE.	1700
16 - 18 INCLUSIVE.	1900
20	2500

NORTHERN POWERGRID		Lloyds Court, 78 Grey Street, Newcastle Upon Tyne, NE1 6AF	
Manufacturer Details		33KV OVERHEAD LINES STRAIGHT LINE DC WOOD H POLE DRILLING, SCARFING AND MARKING 2900 CENTRES POLE FABRICATION	
Sheet No. 2	Scale AS SHOWN	Document Details	
Prepared By W7Brian.James		LEGACY OTHER	
Modified 22/03/2023	Grid Reference	Drawing No. C115998	Historic Drawing No. 1091161151
Created	Checked By G HAMMEL	Revision	Notes