


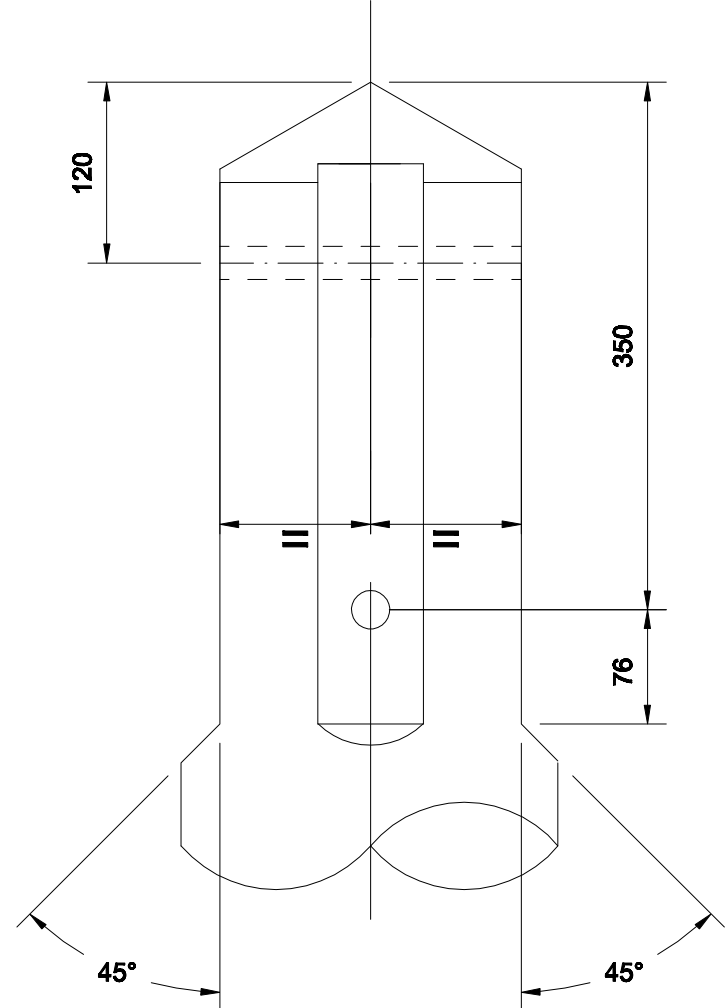
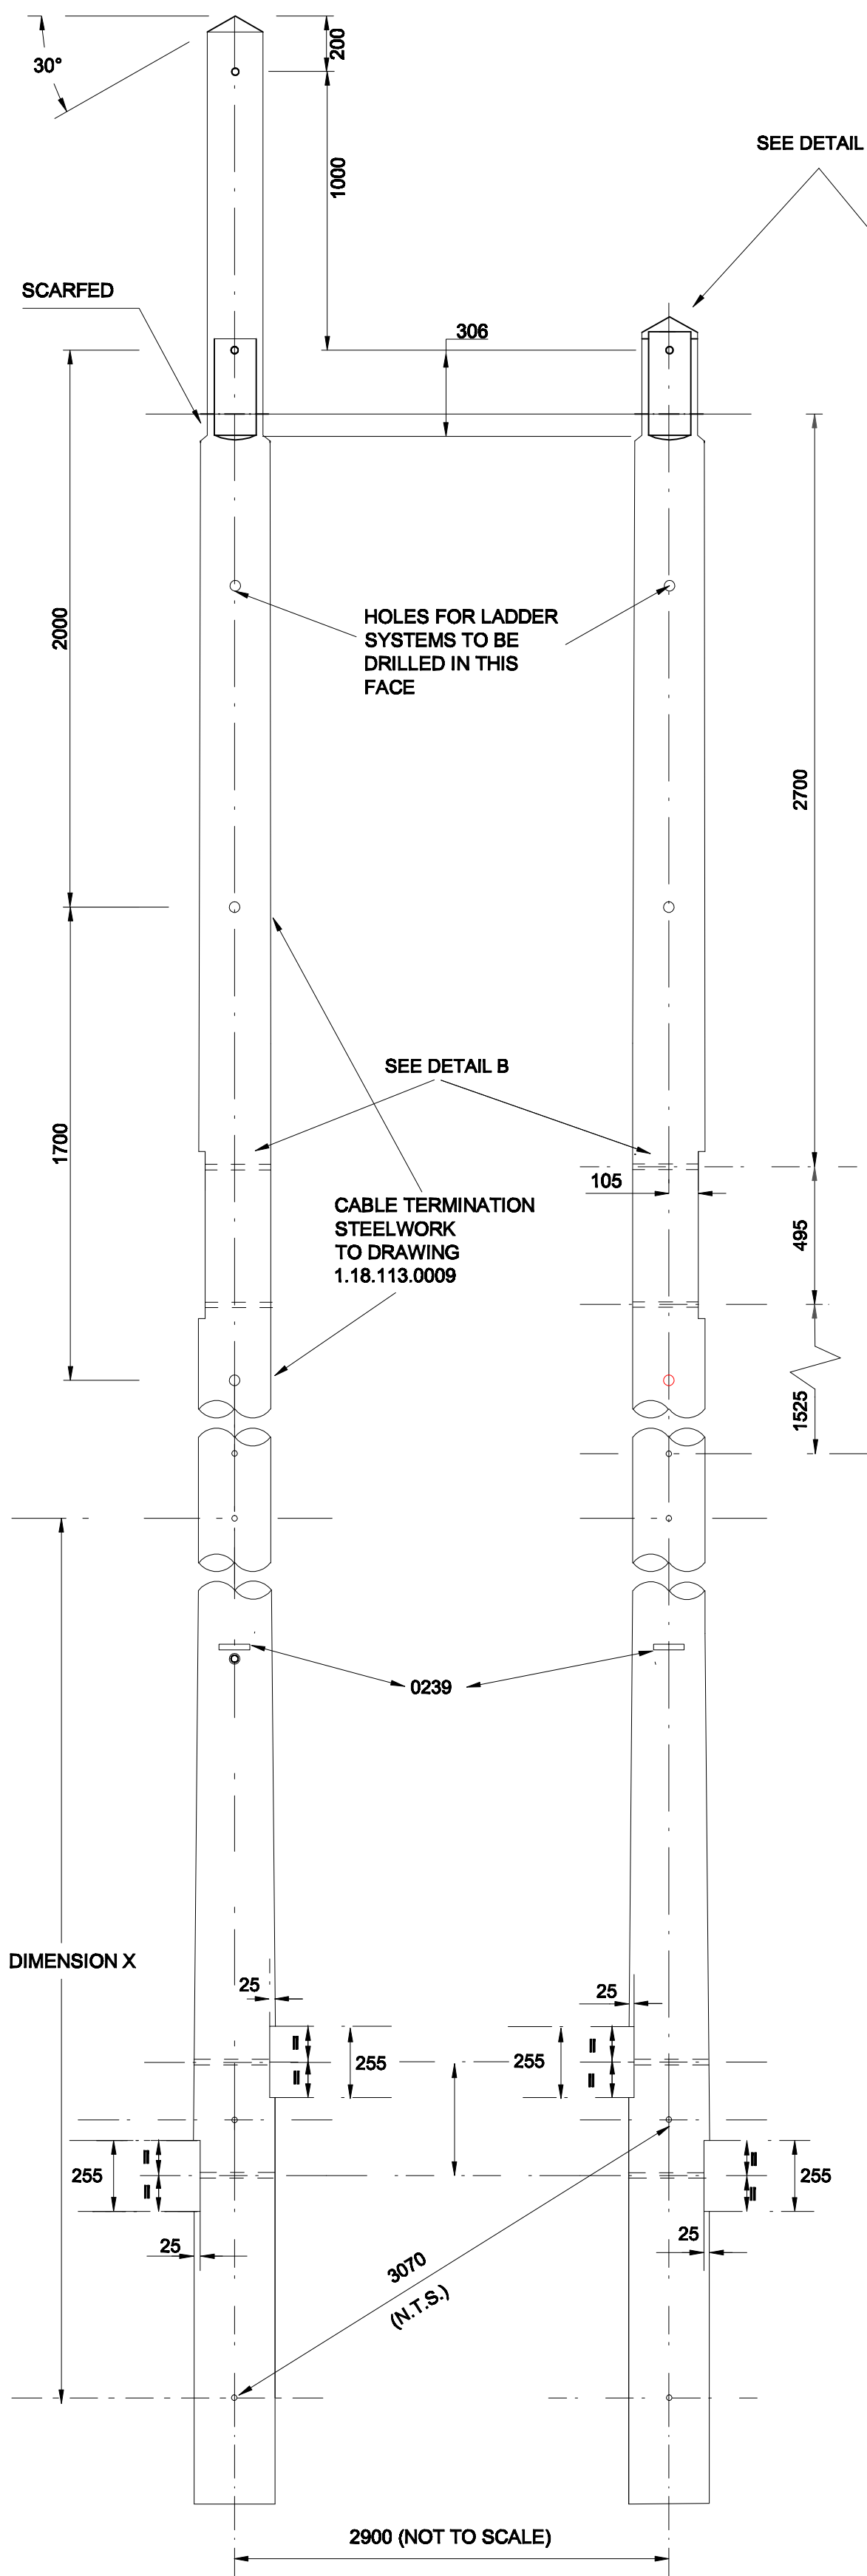


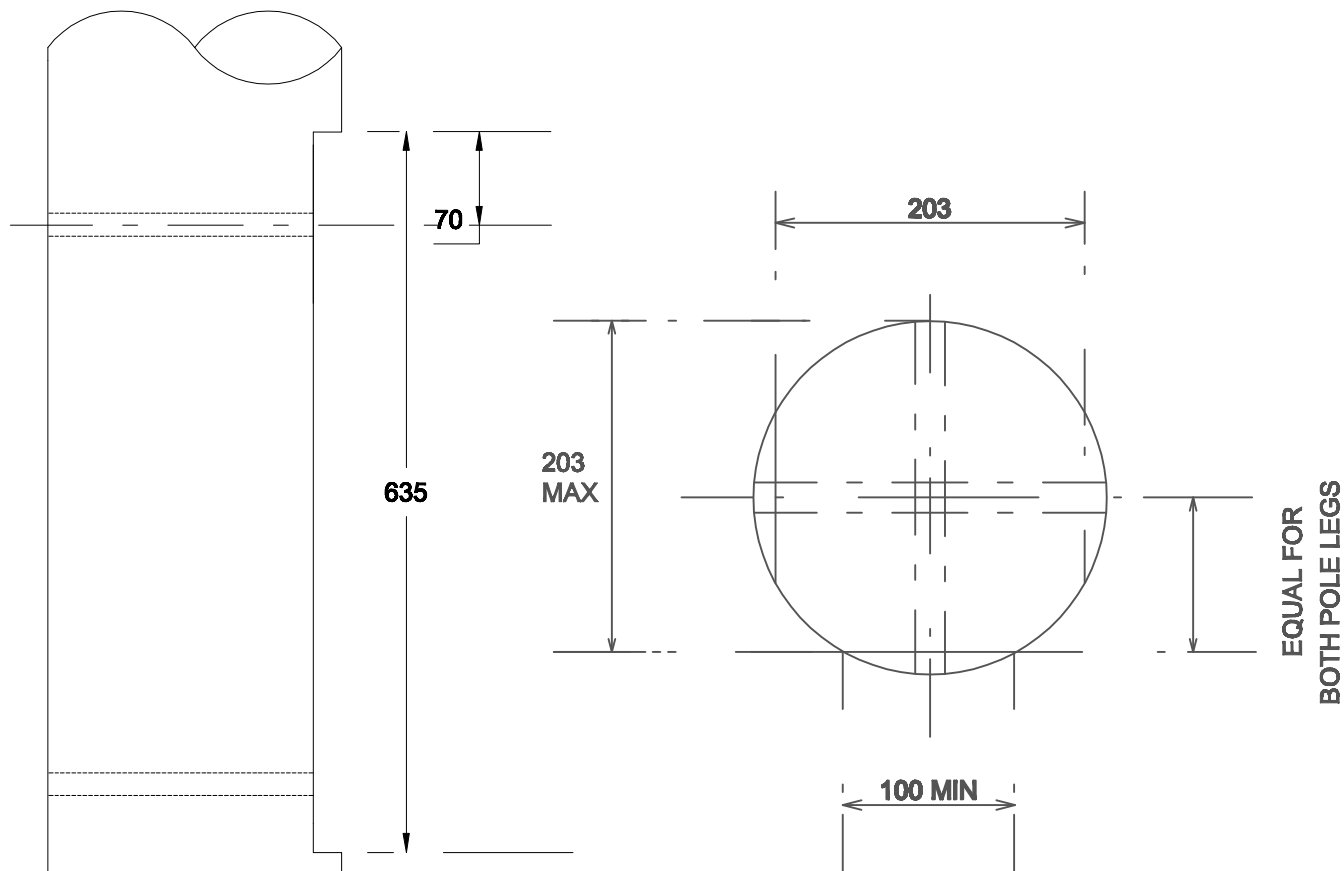

SIDE ELEVATION

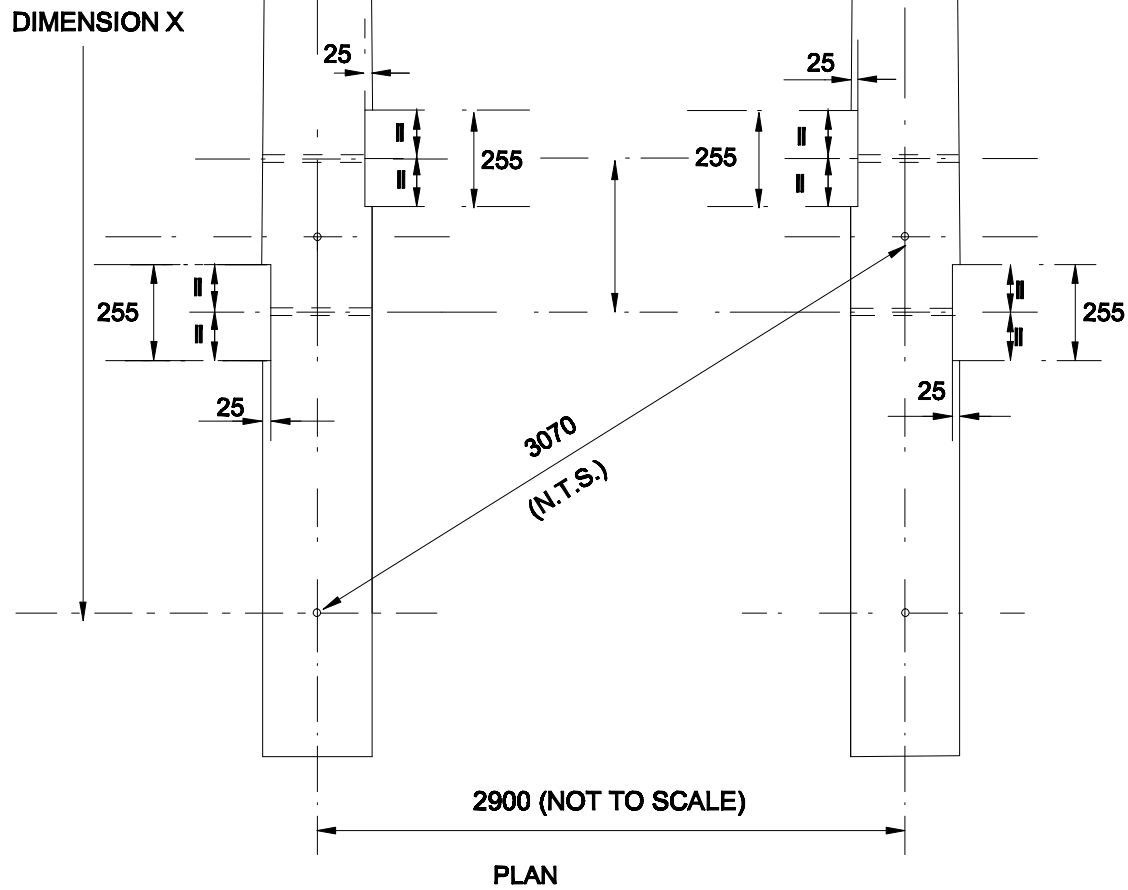

PLAN
DETAIL 'A'
SCALE 1:5

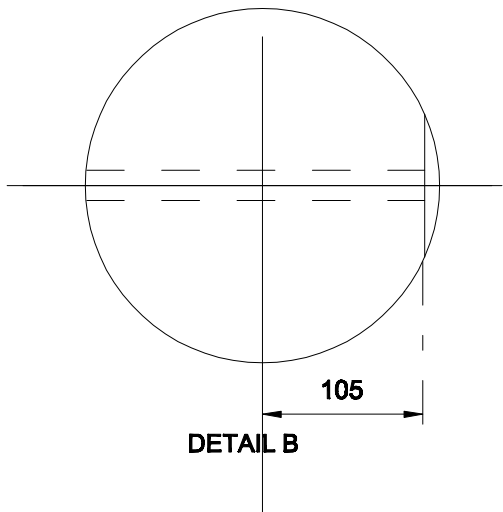

POLE LENGTH	DIM X	DIM Y
12.0m	5655	1700
13.0m	6655	1700
14.0m	7655	1700
15.0m	8655	1700
16.0m	9655	1900

NOTES:

- POLE LEGS TO BE MATCHED. POLE TOP MINIMUM DIAMETER BEFORE FABRICATION STOUT - 230mm
- ALL HOLES TO BE 22mm DIA. DRILLED AT RIGHT ANGLES TO VERTICAL CENTRE LINE OF POLE. ALL DRILLING AND CUTTING TO BE DONE STRICTLY TO TEMPLATE PRIOR TO CREASOTING.
- POLE BUTTS TO CUT AT RIGHT ANGLES TO AXIS OF POLE.
- POLE LEGS TO BE NOTCHED AND DRILLED FOR 250 X 125 WOOD BALKS AS SHOWN
- POLE TO BE SUPPLIED WITH 4 - 1300 X 250 X 125 BALKS TO DRG NO 1 00 043 9130 TYPE 2 CUT FROM THE SQUARE AND 4 - M20 GALVANISED BOLTS EACH WITH 1 FLAT AND 1 CURVED GALVANISED WASHER TO DRG NOS 1 00 043 9804 AND 9805 RESPECTIVELY.
- HOLES NOT REQUIRED FOR PARTICULAR APPLICATIONS WILL BE PLUGGED ON SITE
- 1 LEG ONLY EXTENDED TO ACCOMMODATE EARTH WIRE ATTACHMENT ON WOODHOUSE MAST DESIGNS.

ALL DIMENSIONS SHOWN ARE IN MILLIMETRES UNLESS OTHERWISE STATED



Manufacturer Details

Sheet No.
19

Scale
1:20

Prepared By
Barbara Gordon

Revised
03/11/14

Date Issued
08/10/14

Grid Reference

Checked By
M WILSON

Lloyds Court, 78 Grey Street, Newcastle Upon Tyne, NE1 6AF

33KV SINGLE CIRCUIT LINES
DRILLING AND SCARFING FOR TERMINAL SUPPORT
WITH SURGE ARRESTERS - 1173 SHEET 18 & 20

Type

OVERHEAD

POLES

Ref No.

C1040897

Historic
Drg.No.

1091231173

Revision A

Notes