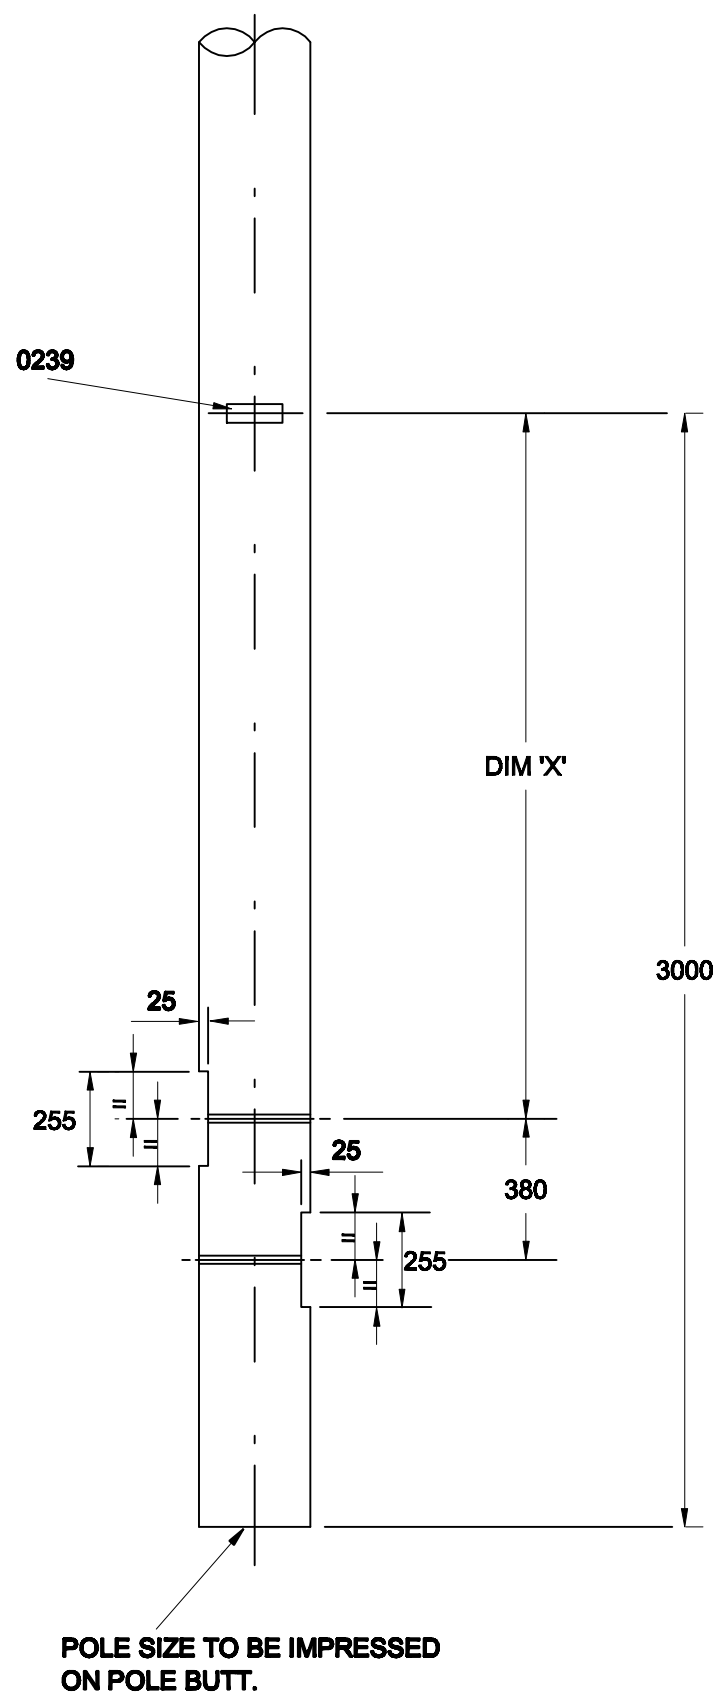
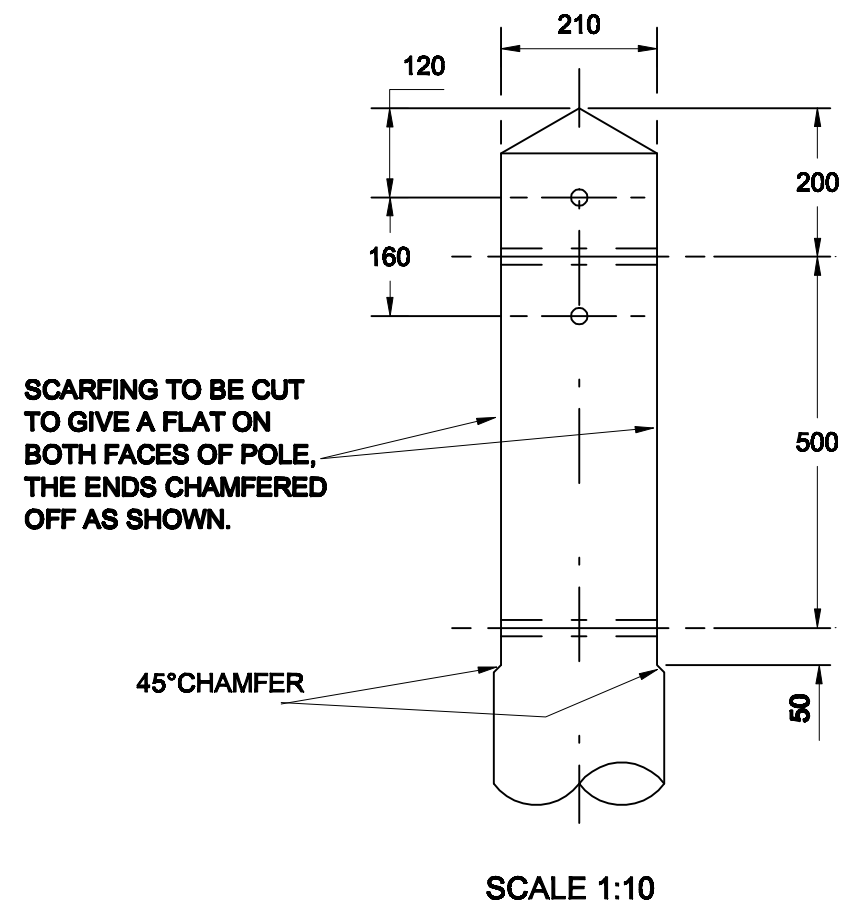
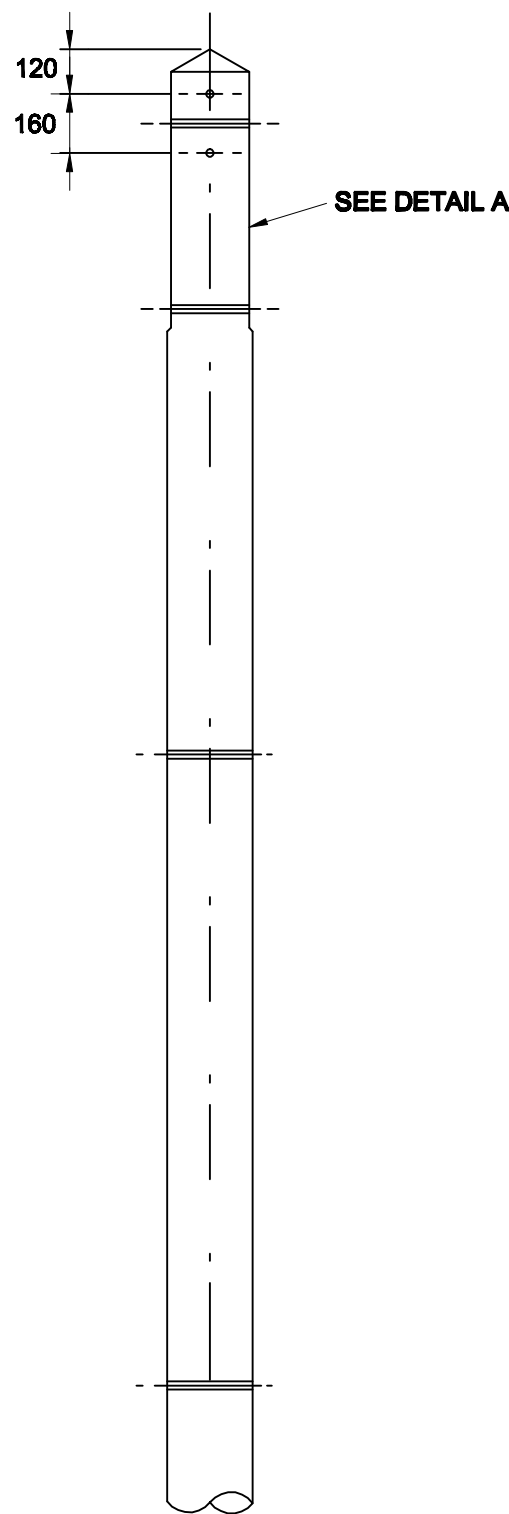
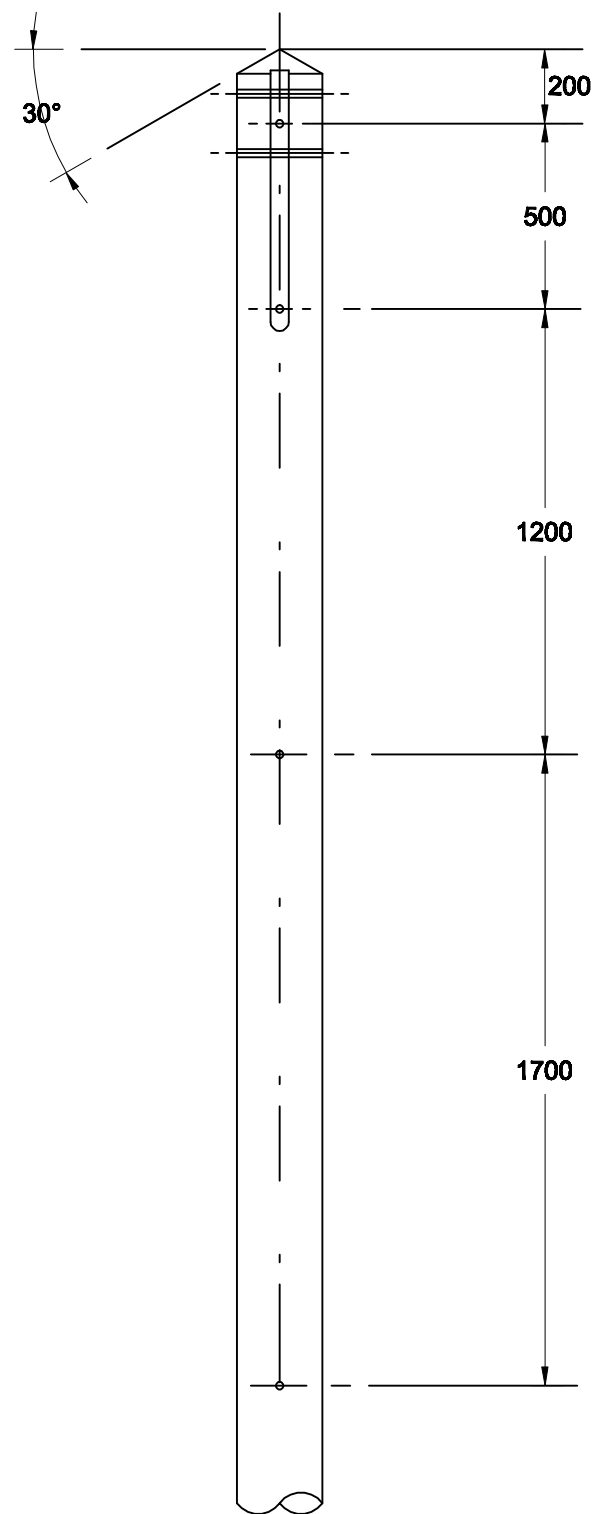


NOTES.

- 1.CLASS OF POLE TO BE STOUT,POLE TOP TO BE 210mm.AFTER FABRICATION.
- 2.ALL HOLES TO BE 22mm.DIA.DRILLED AT RIGHT ANGLES TO VERTICAL CENTRE LINE OF POLE. UNLESS SPECIFIED OTHERWISE. ALL DRILLING AND CUTTING TO BE DONE STRICTLY TO TEMPLATE PRIOR TO PRESERVATIVE TREATMENT.
- 3.POLE BUTT TO BE CUT AT RIGHT ANGLES TO AXIS OF POLE.
- 4.POLE TO BE NOTCHED AND DRILLED FOR DUPLICATE 250 x 125 BAULKES.

POLE LENGTH (m)	DIM X (mm)
9.0 - 11.0 INCLUSIVE	1900
11.5 - 12.0 INCLUSIVE	1700
13.0 - 15.0 INCLUSIVE	1400
16.0 - 18.0 INCLUSIVE	1100

ALL DIMENSIONS SHOWN ARE IN MILLIMETRES UNLESS OTHERWISE STATED.

 NORTHERN POWERGRID Manufacturer Details	Lloyds Court, 78 Grey Street, Newcastle Upon Tyne, NE1 6AF	
	HV OVERHEAD LINES FABRICATION FOR SINGLE POLE TERMINAL DRG. NO. 1.00.043.4010 SHEET 6	
Sheet No. 7	Scale 1:20	Type OVERHEAD LINES
Prepared By Barbara.Gordon	Grid Reference	Ref No. C1040649
Revised 01/10/14	Checked By G HAMMEL	Historic Drg.No. 1000434010
Date Issued 01/10/14		Revision A Notes