


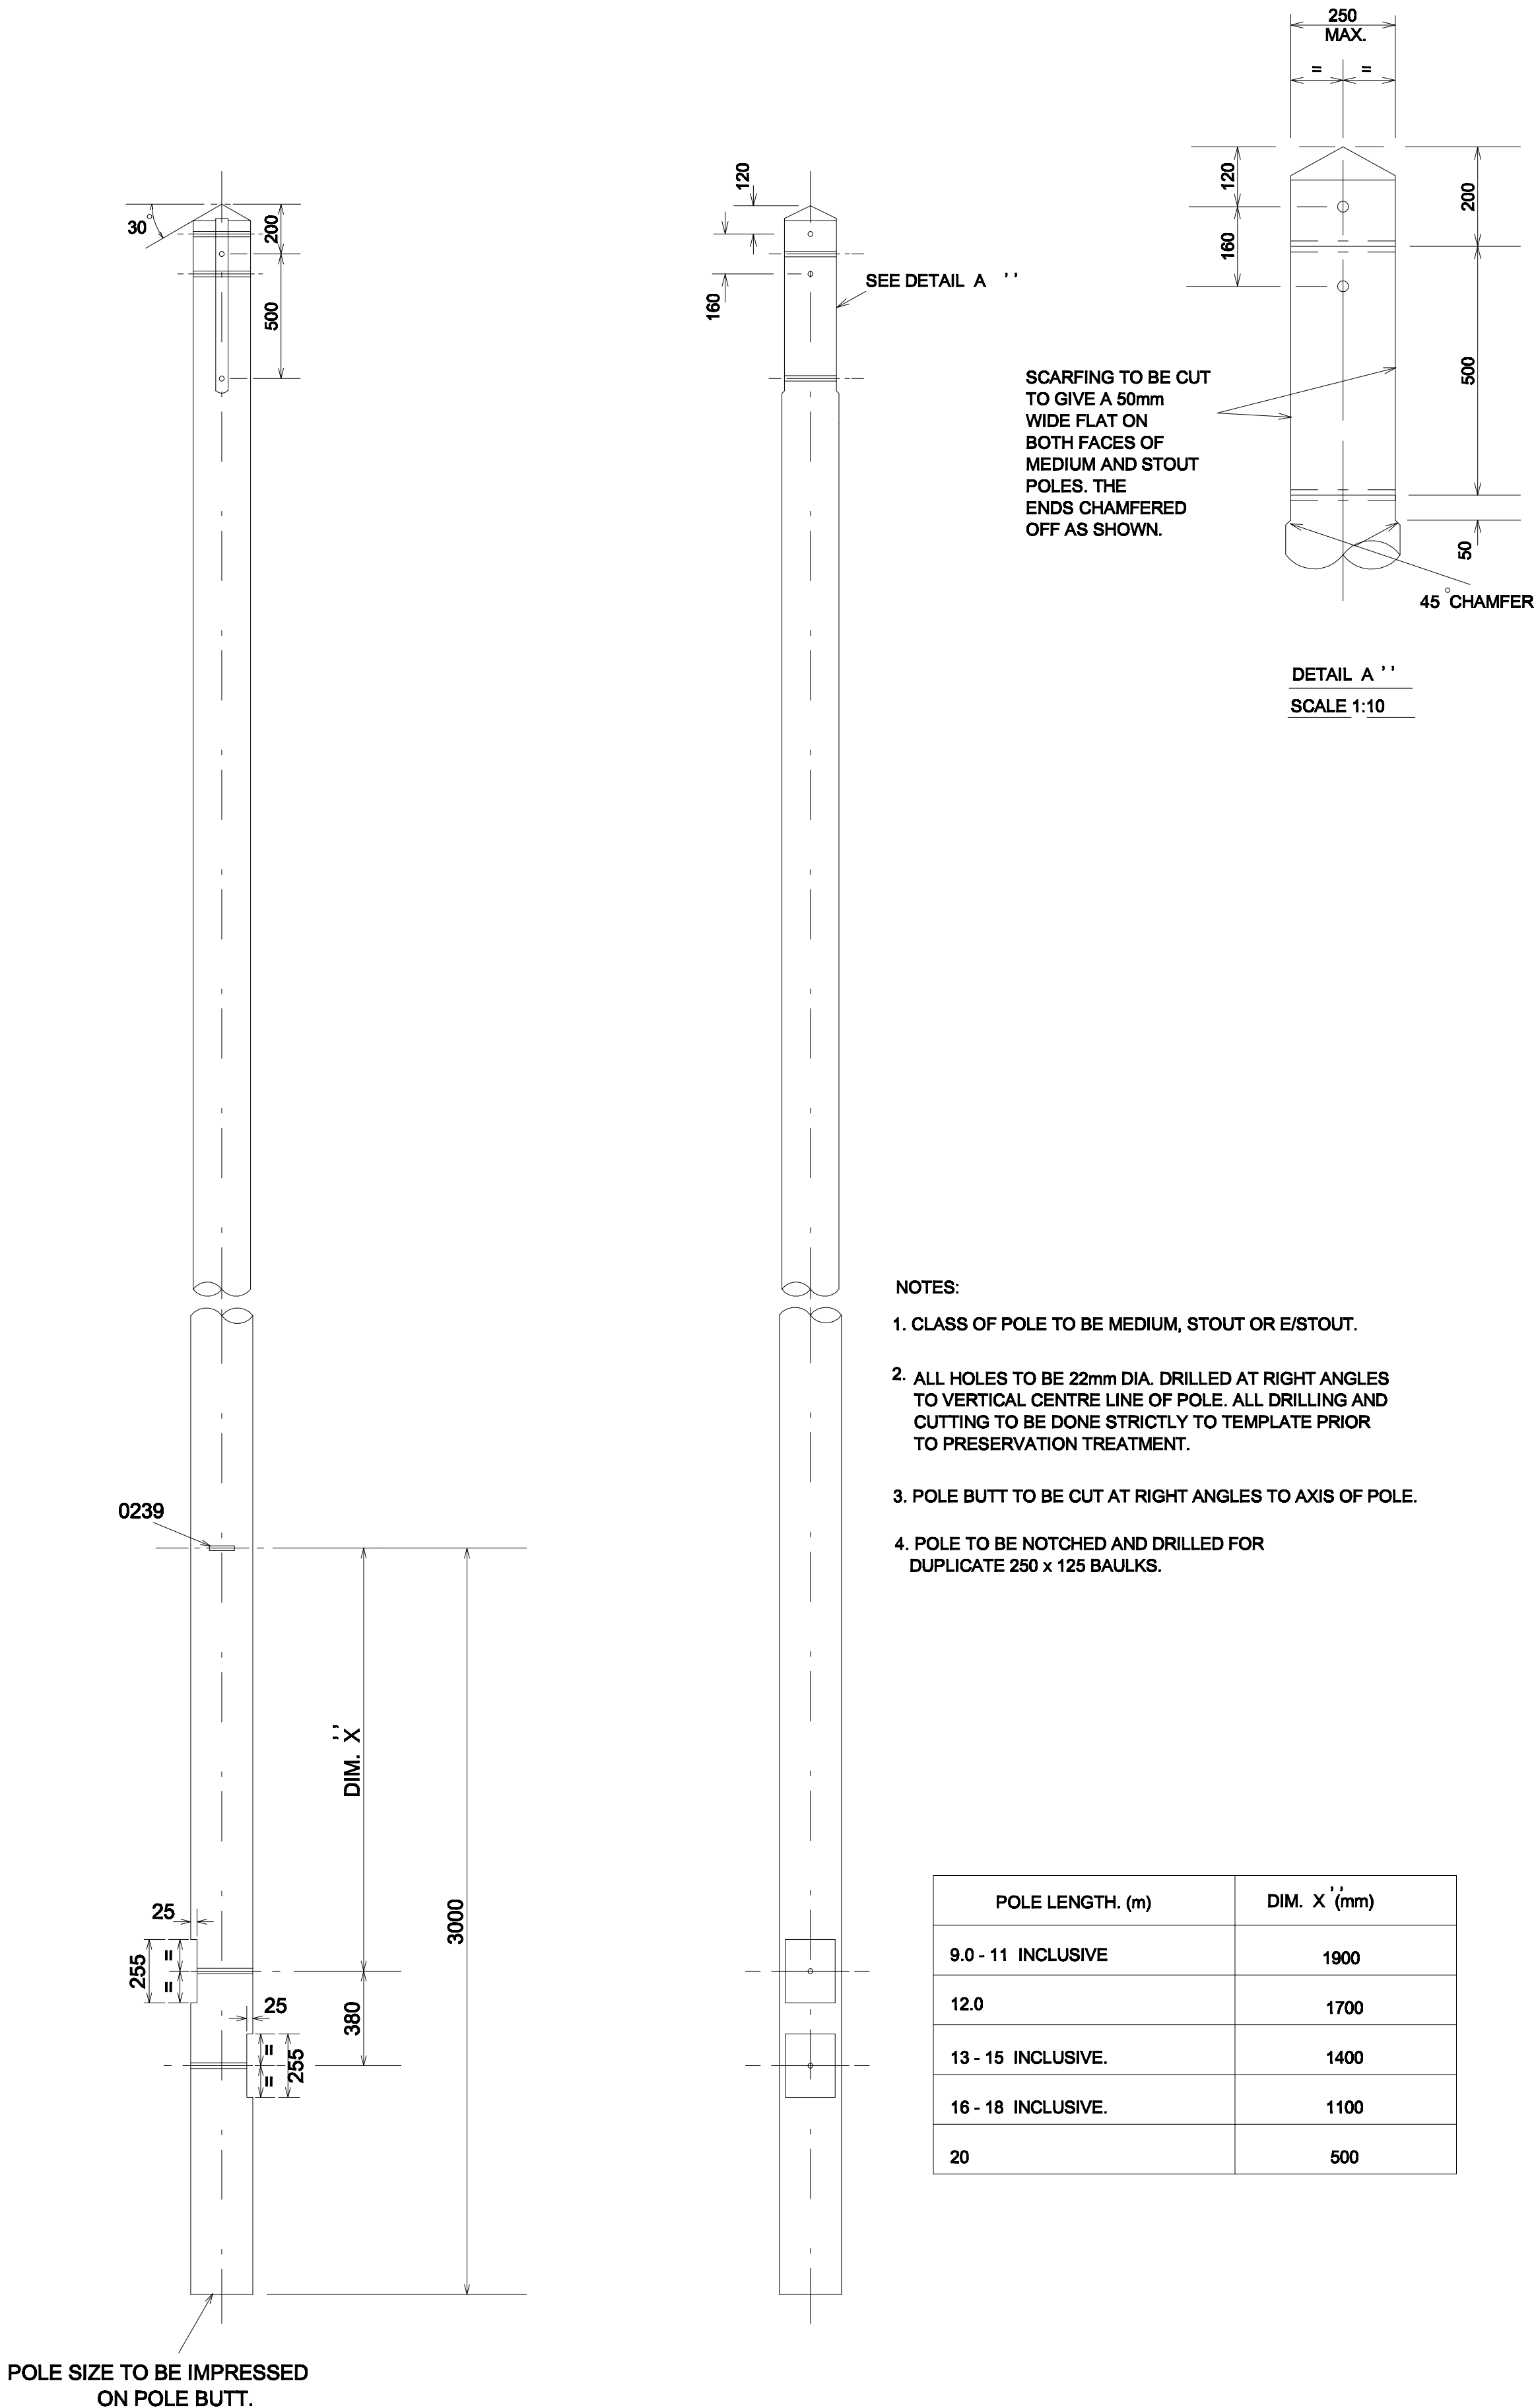

NOTES:

1. CLASS OF POLE TO BE MEDIUM, STOUT OR E/STOUT.
2. ALL HOLES TO BE 22mm DIA. DRILLED AT RIGHT ANGLES TO VERTICAL CENTRE LINE OF POLE. ALL DRILLING AND CUTTING TO BE DONE STRICTLY TO TEMPLATE PRIOR TO PRESERVATION TREATMENT.
3. POLE BUTT TO BE CUT AT RIGHT ANGLES TO AXIS OF POLE.
4. POLE TO BE NOTCHED AND DRILLED FOR DUPLICATE 250 x 125 BAULKS.

POLE LENGTH. (m)	DIM. X (mm)
9.0 - 11 INCLUSIVE	1900
12.0	1700
13 - 15 INCLUSIVE.	1400
16 - 18 INCLUSIVE.	1100
20	500

 Manufacturer Details		Lloyds Court, 78 Grey Street, Newcastle Upon Tyne, NE1 6AF	
		HV OVERHEAD LINES SINGLE POLE FABRICATION FOR ARRANGEMENTS TO ESI 43-40	
Sheet No. 1	Scale 1:20	Type PLANNING SYSTEM	
Prepared By Joan.Oakley	Grid Reference	Ref No. C1004131	Historic Drg.No. 1000434001
Revised 09/06/14	Date Issued 06/12/11	Checked By G HAMMEL	Revision Notes