


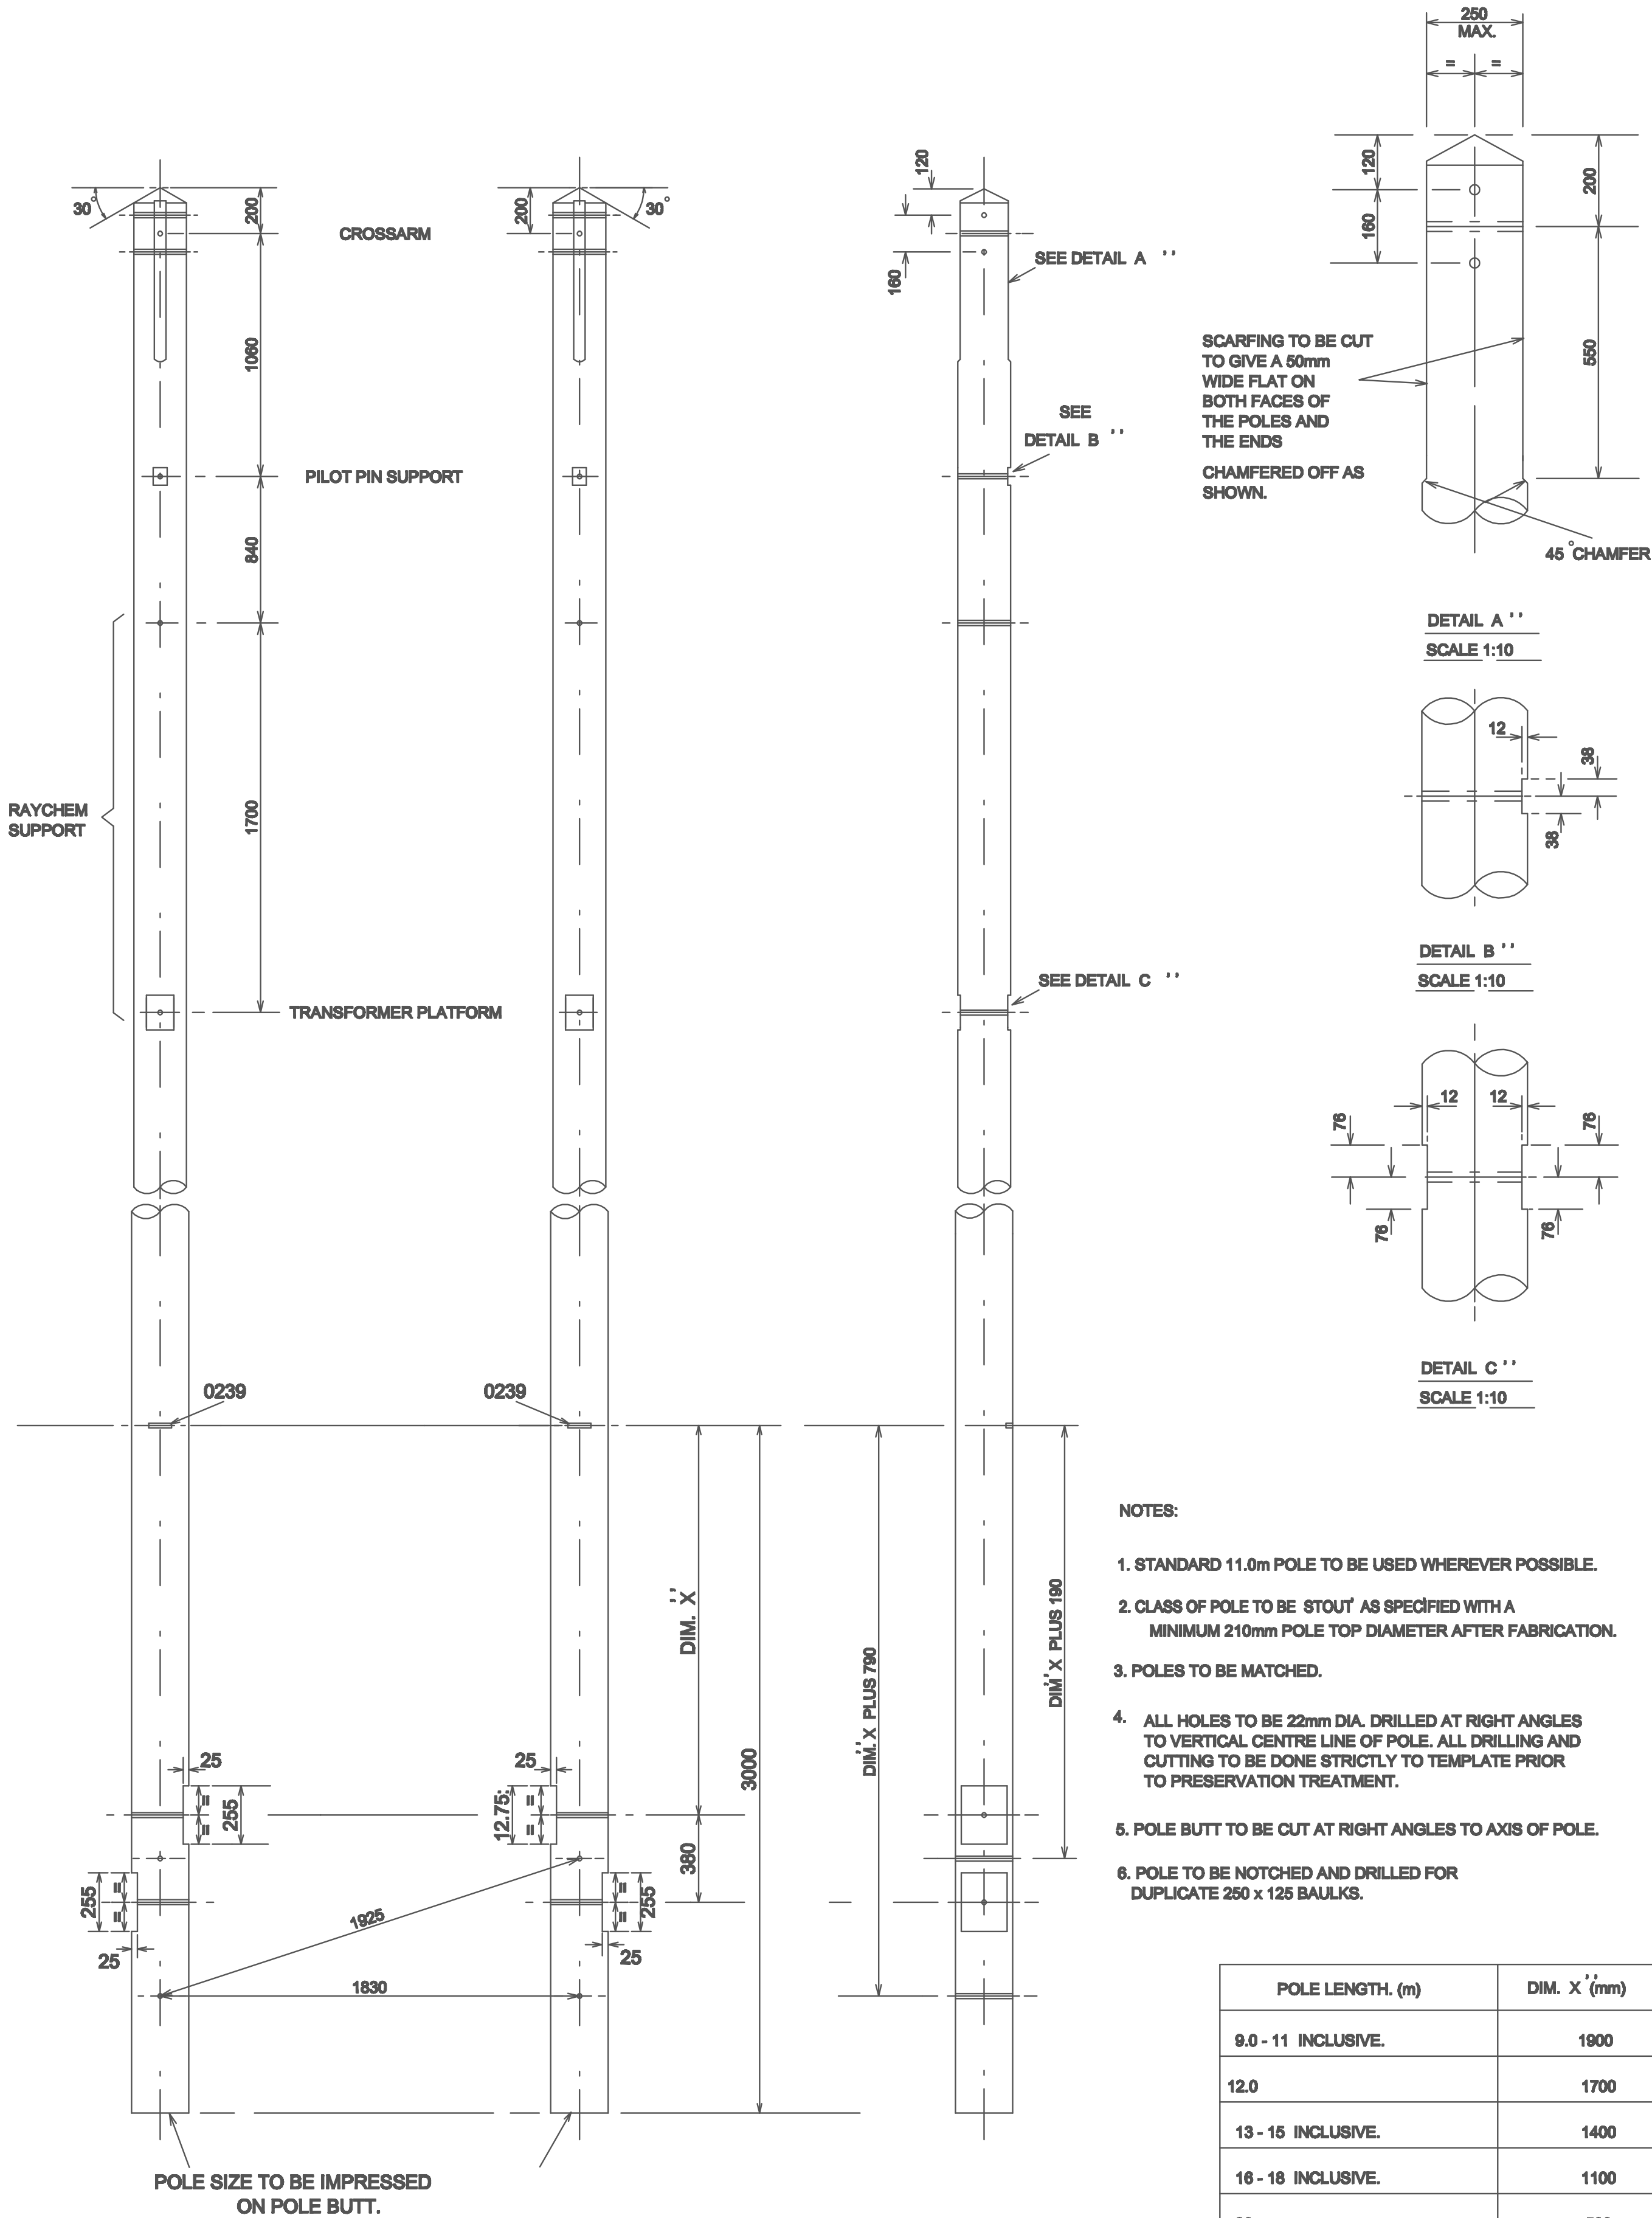

FABRICATION DRAWING FOR USE WITH THE FOLLOWING ARRANGEMENT DRAWINGS:

- DRG.No. 1.00.043.4006 SHEET 1.
- DRG.No. 1.00.043.4007 SHEET 1 & 2.
- DRG.No. 1.00.043.4011 SHEET 1.
- DRG.No. 1.00.043.4011 SHEET 6.
- DRG.No. 1.09.108.0860 SHEET 1.
- DRG.No. 1.09.108.0860 SHEET 3.

ALL DIMENSIONS SHOWN ARE IN MILLIMETRES UNLESS OTHERWISE STATED.

 NORTHERN POWERGRID		Lloyds Court, 78 Grey Street, Newcastle Upon Tyne, NE1 6AF	
Manufacturer Details		HV OVERHEAD LINES MULTIFABRICATION 'H' POLE SUITABLE FOR LINE SECTION OR TERMINAL ARRANGEMENT & PLANT RELATED CABLE OR PLATFORM MOUNTED TRANSFORMER	
Sheet No. 2	Scale	Type PLANNING	SYSTEM
Prepared By Joan.Oakley	Grid Reference	Ref No. C1004137	Historic Drg.No. 1000434002
Revised 04/10/13	Checked By G. HAMMEL	Revision A	Notes
Date Issued 07/12/11			