


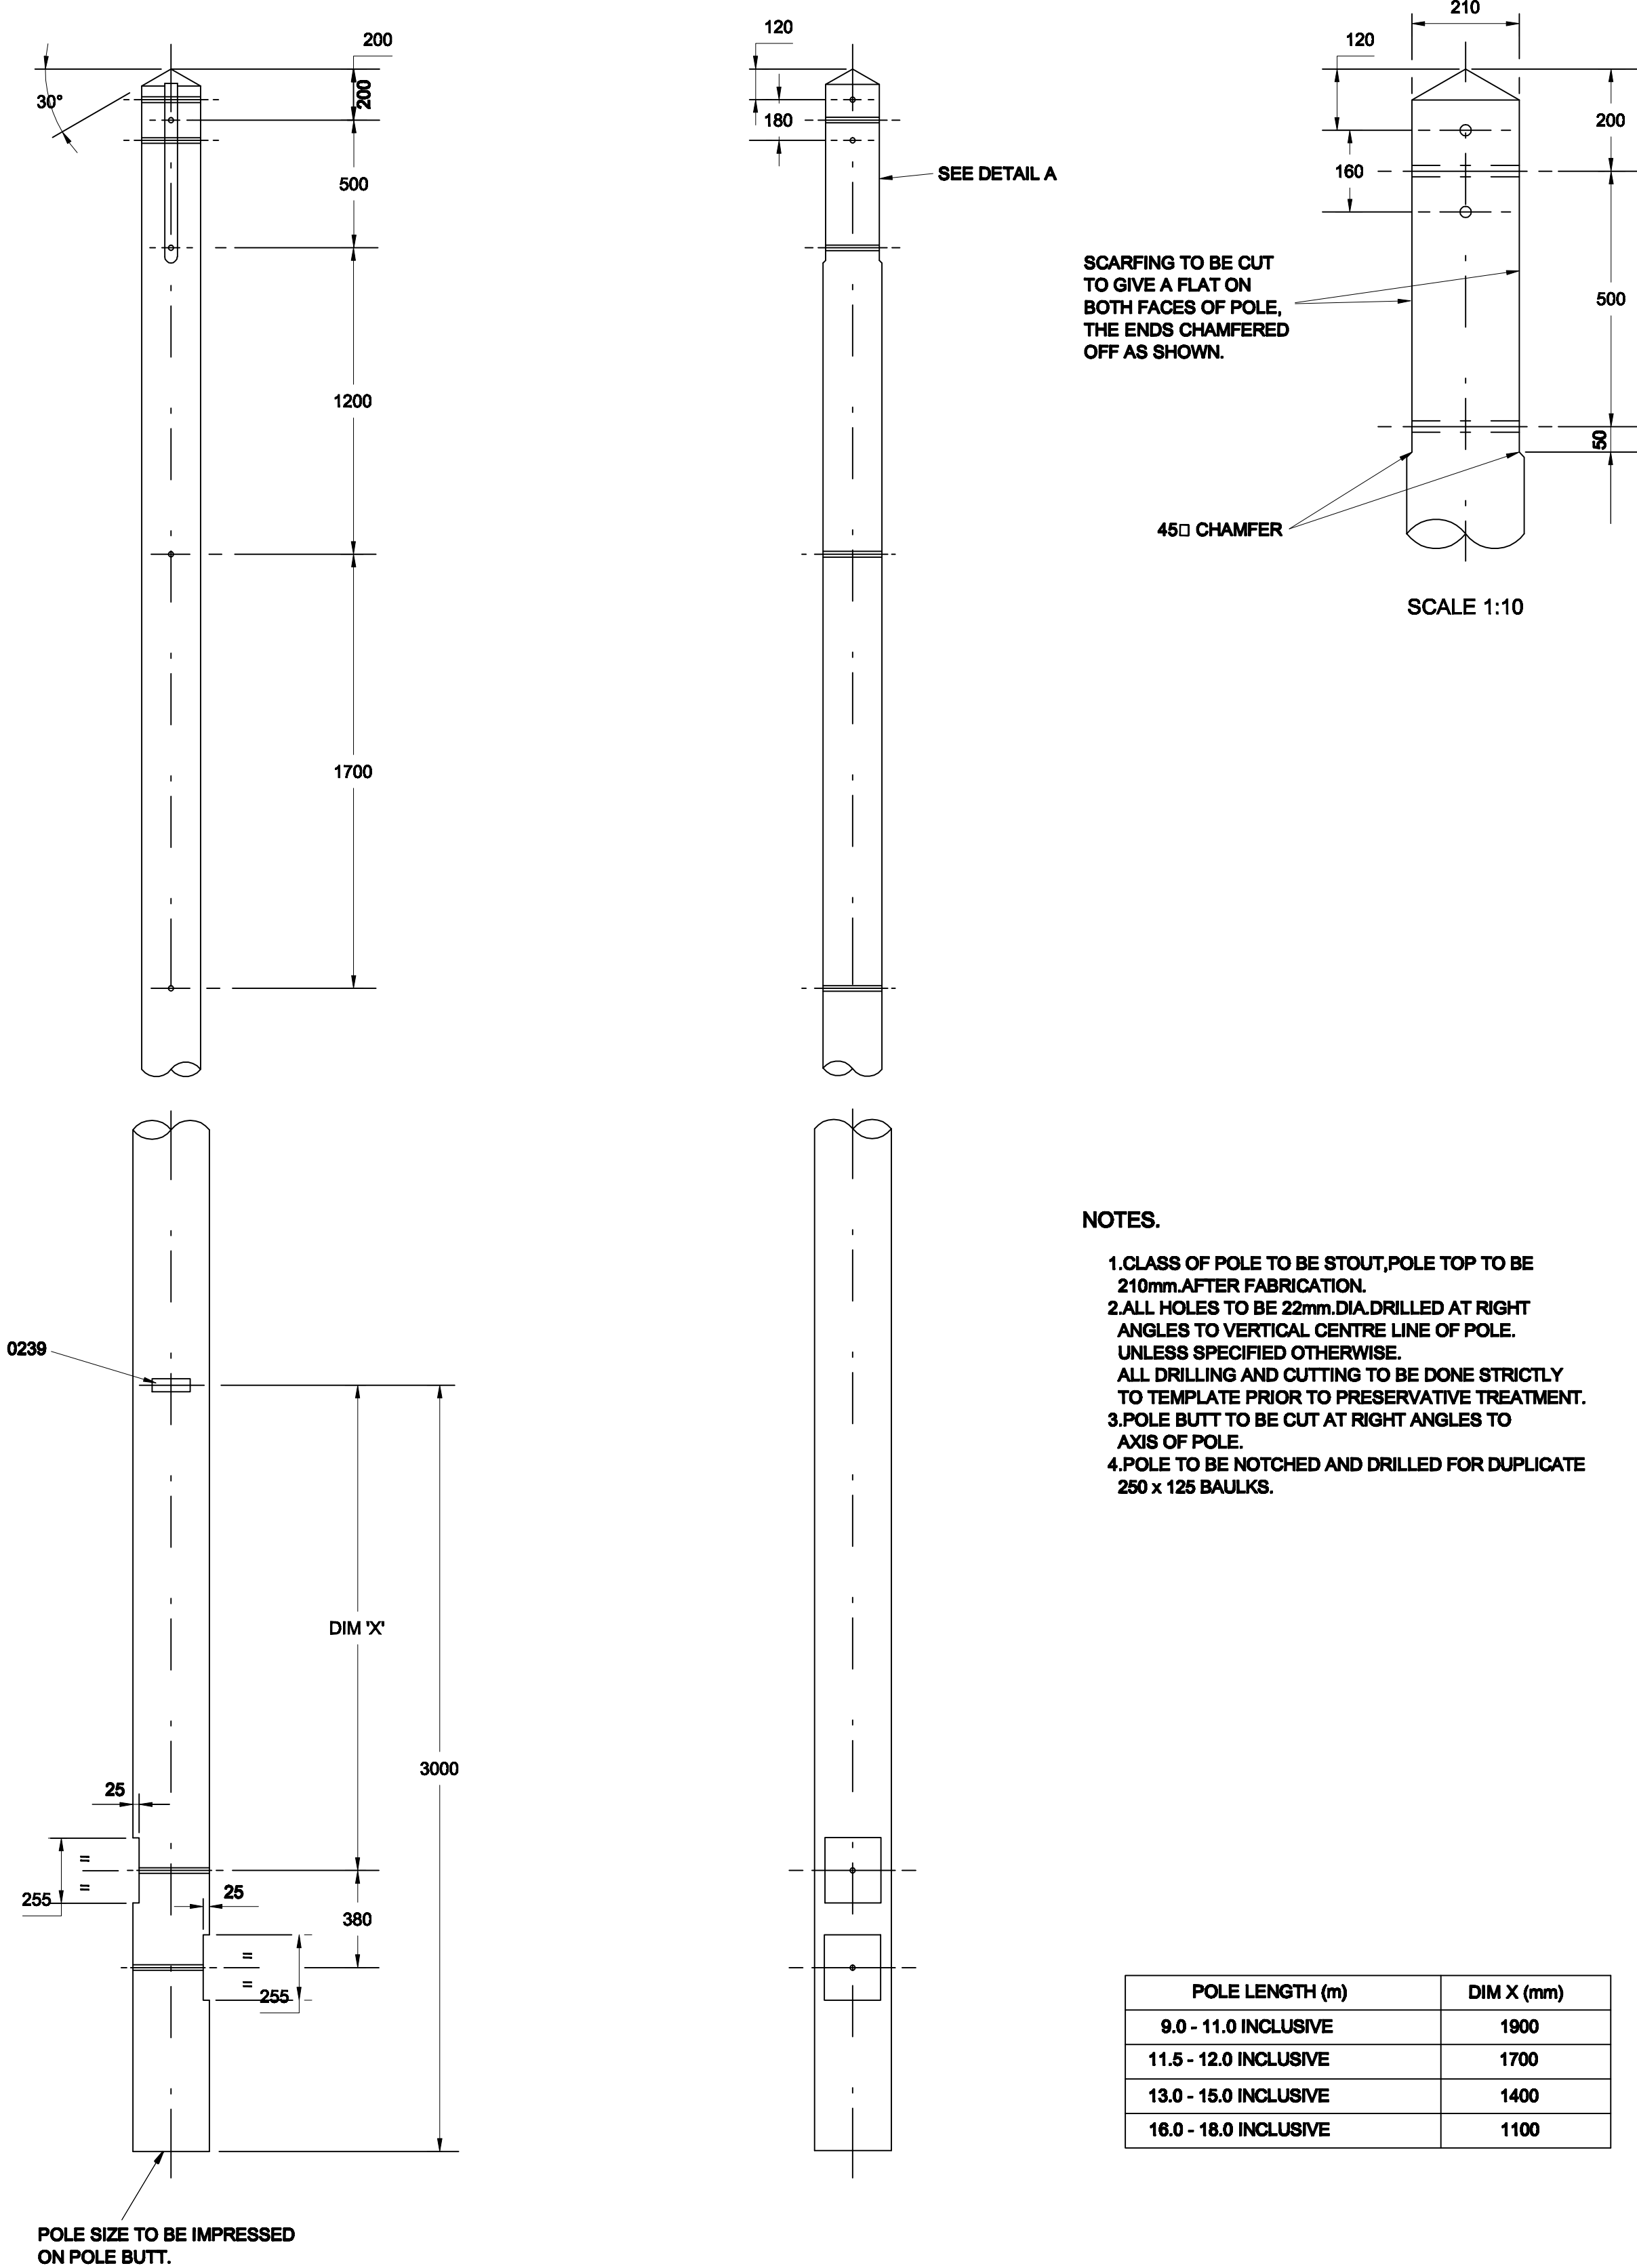

- NOTES.**
- 1.CLASS OF POLE TO BE STOUT,POLE TOP TO BE 210mm.AFTER FABRICATION.
  - 2.ALL HOLES TO BE 22mm.DIA.DRILLED AT RIGHT ANGLES TO VERTICAL CENTRE LINE OF POLE. UNLESS SPECIFIED OTHERWISE. ALL DRILLING AND CUTTING TO BE DONE STRICTLY TO TEMPLATE PRIOR TO PRESERVATIVE TREATMENT.
  - 3.POLE BUTT TO BE CUT AT RIGHT ANGLES TO AXIS OF POLE.
  - 4.POLE TO BE NOTCHED AND DRILLED FOR DUPLICATE 250 x 125 BAULKS.

| POLE LENGTH (m)       | DIM X (mm) |
|-----------------------|------------|
| 9.0 - 11.0 INCLUSIVE  | 1900       |
| 11.5 - 12.0 INCLUSIVE | 1700       |
| 13.0 - 15.0 INCLUSIVE | 1400       |
| 16.0 - 18.0 INCLUSIVE | 1100       |

ALL DIMENSIONS SHOWN ARE IN MILLIMETRES UNLESS OTHERWISE STATED.

|   |  |                                                                                     |          |                     |            |
|---|--|-------------------------------------------------------------------------------------|----------|---------------------|------------|
| <div><div></div><div><div>NORTHERN</div><div>POWERGRID</div></div></div> <div>Manufacturer Details</div> <div><div>Sheet No.</div><div>8</div><div>Scale</div><div>1:20</div></div> <div><div>Prepared By</div><div>Barbara.Gordon</div></div> <div><div>Revised</div><div>01/10/14</div><div>Grid Reference</div></div> <div><div>Date Issued</div><div>01/10/14</div><div>Checked By</div><div>G HAMMEL</div></div> |  | Lloyds Court, 78 Grey Street, Newcastle Upon Tyne, NE1 6AF                          |          |                     |            |
|   |  | HV OVERHEAD LINES<br>FABRICATION FOR SINGLE POLE TERMINAL<br>DRG. NO. 1.00.043.4010 |          |                     |            |
|   |  | Type<br>OVERHEAD<br>LINES                                                           |          |                     |            |
|   |  | Ref No.                                                                             | C1040648 | Historic<br>Drg.No. | 1000434010 |
|   |  | Revision                                                                            | A        | Notes               |            |