



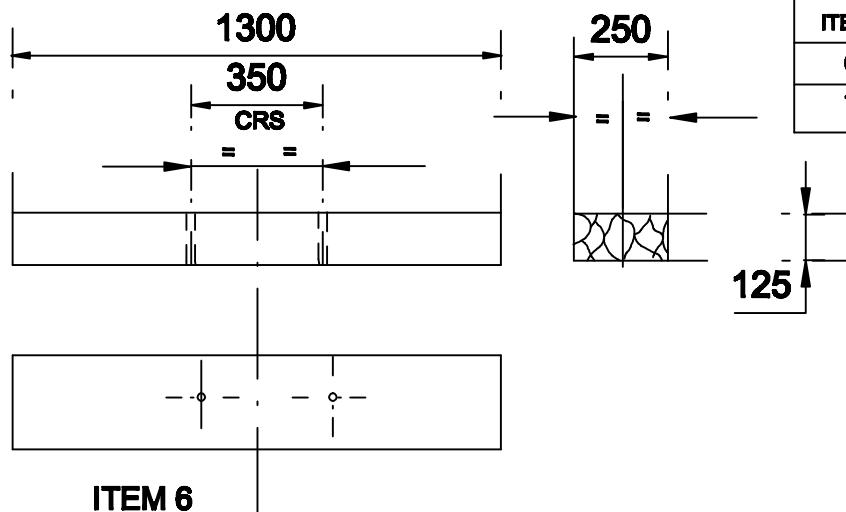

ITEM	CATALOGUE No
6	234475
7	234853

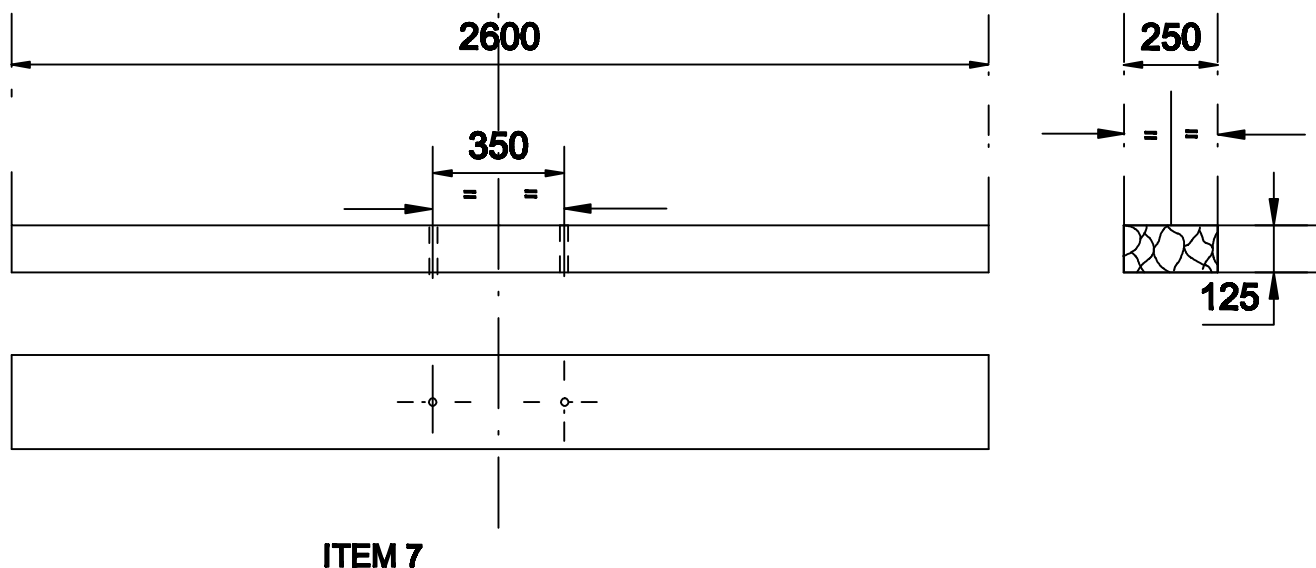

NOTES:

1. TIMBER TO BE BALTIC REDWOOD, SCOTS PINE (PINUS SYLVESTRIS) OR FRENCH MARITIME PINE GENERALLY IN ACCORDANCE WITH BS1990 PART 1
2. BAULKS TO BE CUT FROM SWAN TIMBER TO PRODUCE RECTANGULAR SECTIONS
3. LONGITUDINALLY CUT SURFACES OF BAULKS SHALL BE STRAIGHT AND CLEAN CUT AND THE ANNULAR RINGS SHALL BE APPROX. PARALLEL TO THE WIDE FACE PLANNING NOT REQUIRED
4. BAULKS TO BE TREATED AFTER FABRICATION WITH (A) CREOSOTE TO BS913 (RUEPING PROCESS) OR (B) WATERBORNE SALTS (TANALITH C) TO BS4072
5. HOLES TO BE 22mm DIA.

ALL DIMENSIONS SHOWN ARE IN MILLIMETRES UNLESS OTHERWISE STATED

 NORTHERN POWERGRID		Lloyds Court, 78 Grey Street, Newcastle Upon Tyne, NE1 6AF			
Manufacturer Details		66KV OVERHEAD LINES LAY TERMINAL STRUCTURE			
Sheet No. 2	Scale 1:20				
Prepared By J OAKLEY		Type			
Revised 19/02/14	Grid Reference	Ref No.	C318505	Historic Drg.No.	1.09.101.0650
Date Issued JUN 87	Checked By G. HAMMEL	Revision	C	Notes	