


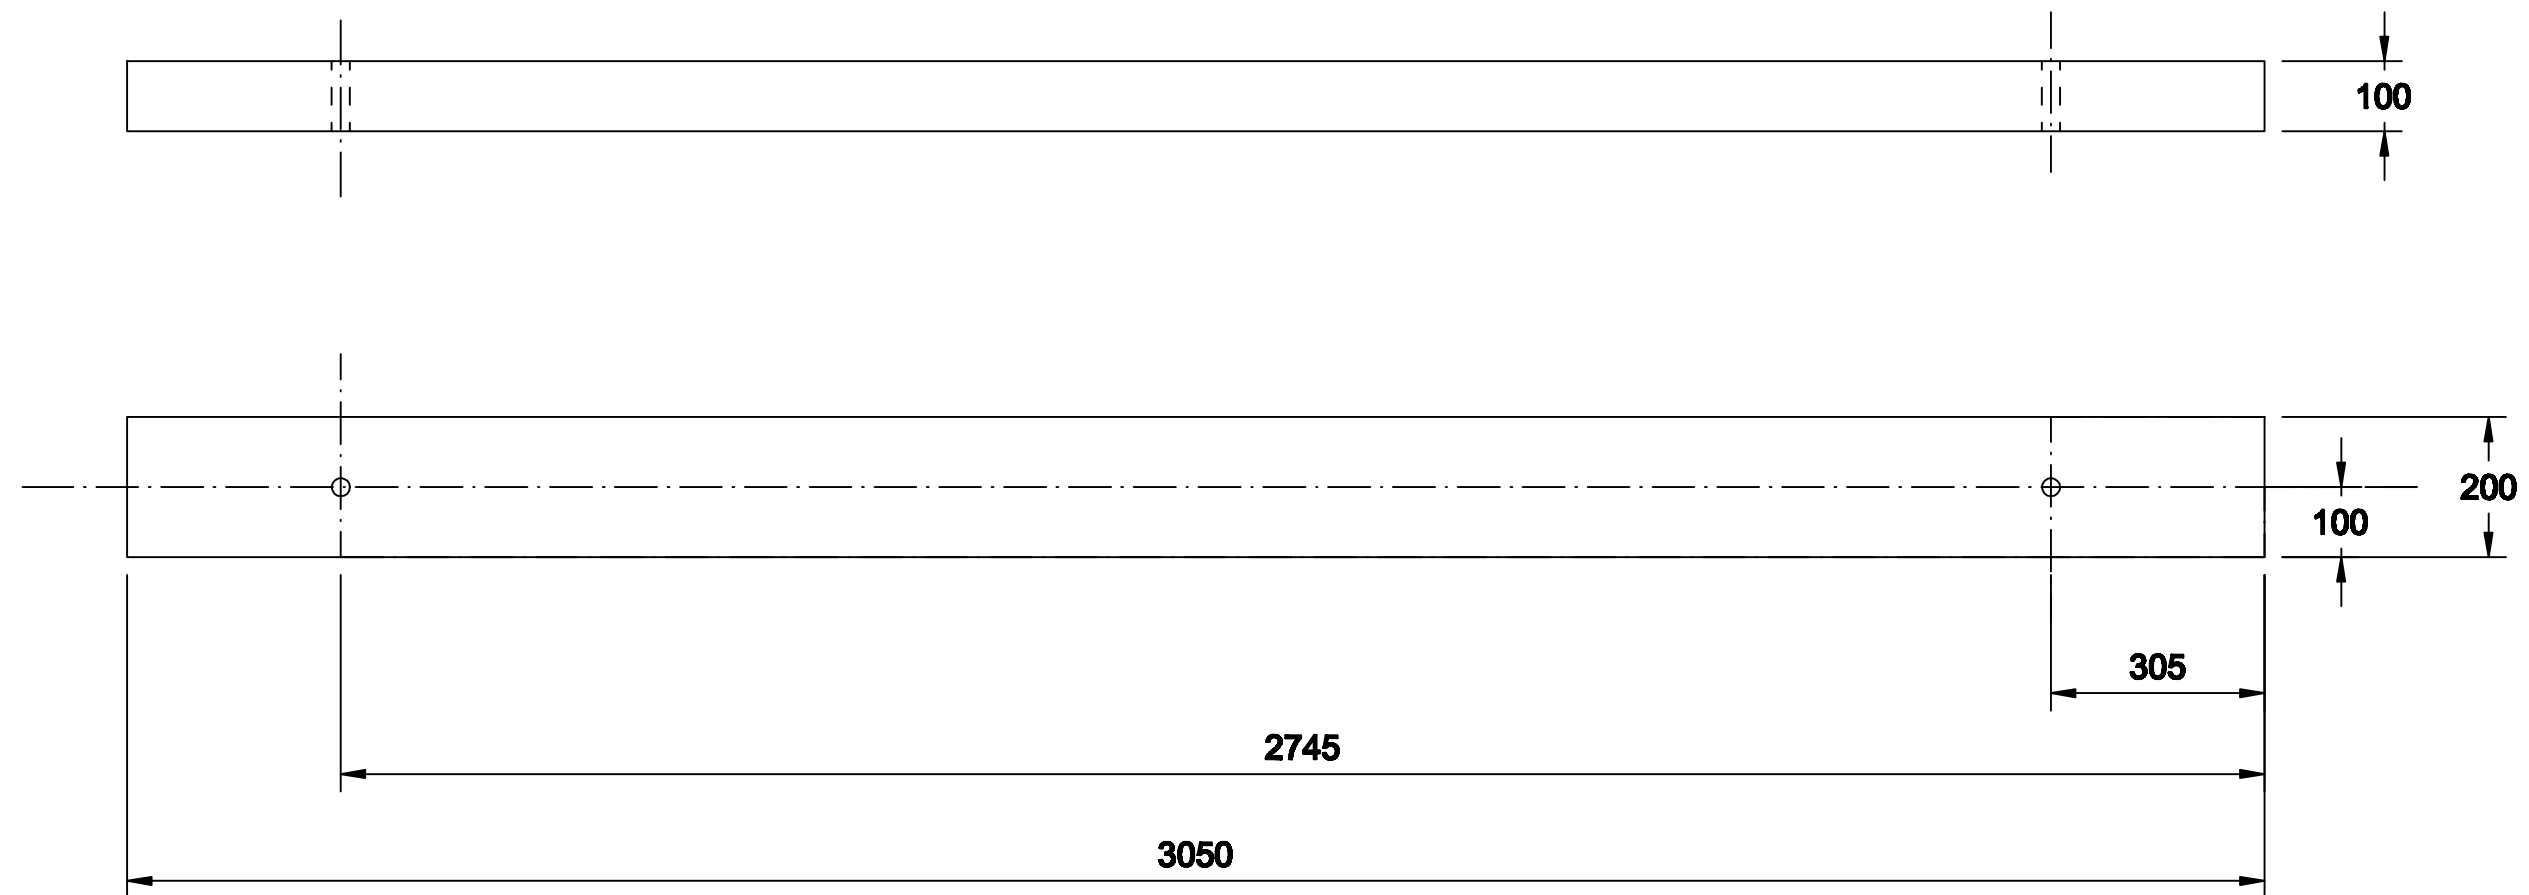

NOTES

1. BAULKS CUT FROM IMPORTED RED FIR.
CREOSOTED TO BS 913 BY RUEPING PROCESS, AFTER FABRICATION
2. ALL HOLES 26mm DIA DRILLED AT RIGHT ANGLES TO CENTRE LINE OF
BAULK

FORMERLY YE DRAWING No Y204L0301

 NORTHERN POWERGRID		Lloyds Court, 78 Grey Street, Newcastle Upon Tyne, NE1 6AF	
		BRACE BLOCK CE/C/37M	
Manufacturer Details			
Sheet No.	1	Scale	1:10
Prepared By		Type	
J OAKLEY			
Revised	19/02/14	Grid Reference	
Date Issued	JAN 05	Checked By	
		G. HAMMEL	
Ref No.	C319093	Historic Drg.No.	1.09.101.0668
Revision	Notes		

ALL DIMENSIONS SHOWN ARE IN MILLIMETRES UNLESS OTHERWISE STATED