


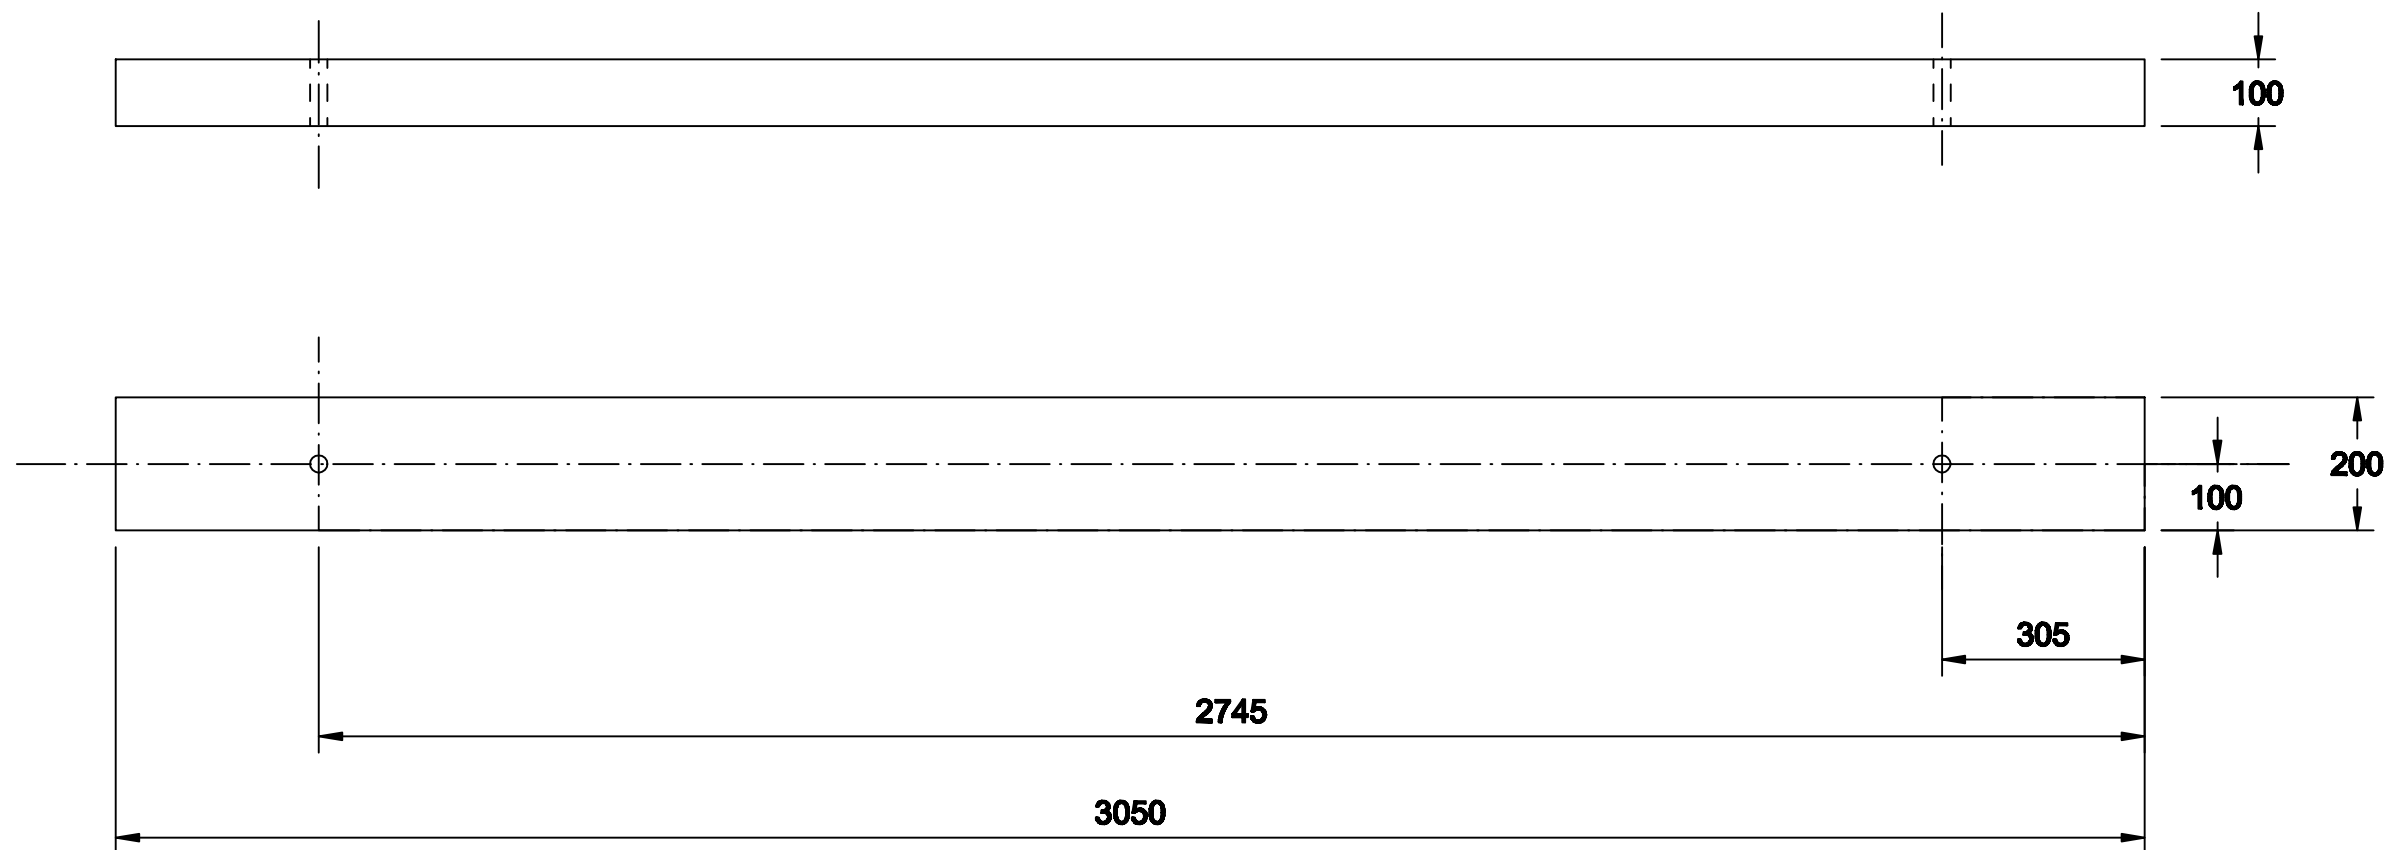

NOTES

1. BAULKS CUT FROM IMPORTED RED FIR.
CREOSOTED TO BS 913 BY RUEPING PROCESS, AFTER FABRICATION
2. ALL HOLES 26mm DIA DRILLED AT RIGHT ANGLES TO CENTRE LINE OF
BAULK

ALL DIMENSIONS SHOWN ARE IN MILLIMETRES UNLESS OTHERWISE STATED

FORMERLY YE DRAWING No Y204L0301

 NORTHERN POWERGRID		Lloyds Court, 78 Grey Street, Newcastle Upon Tyne, NE1 6AF			
		BRACE BLOCK CE/C/37M			
Manufacturer Details					
Sheet No.	1	Scale	1:10		
Prepared By		J OAKLEY		Type	
Revised	19/02/14	Grid Reference		Ref No.	C319093
Date Issued	JAN 05	Checked By		Historic Drg.No.	1.09.101.0668
		G. HAMMEL		Revision	Notes