


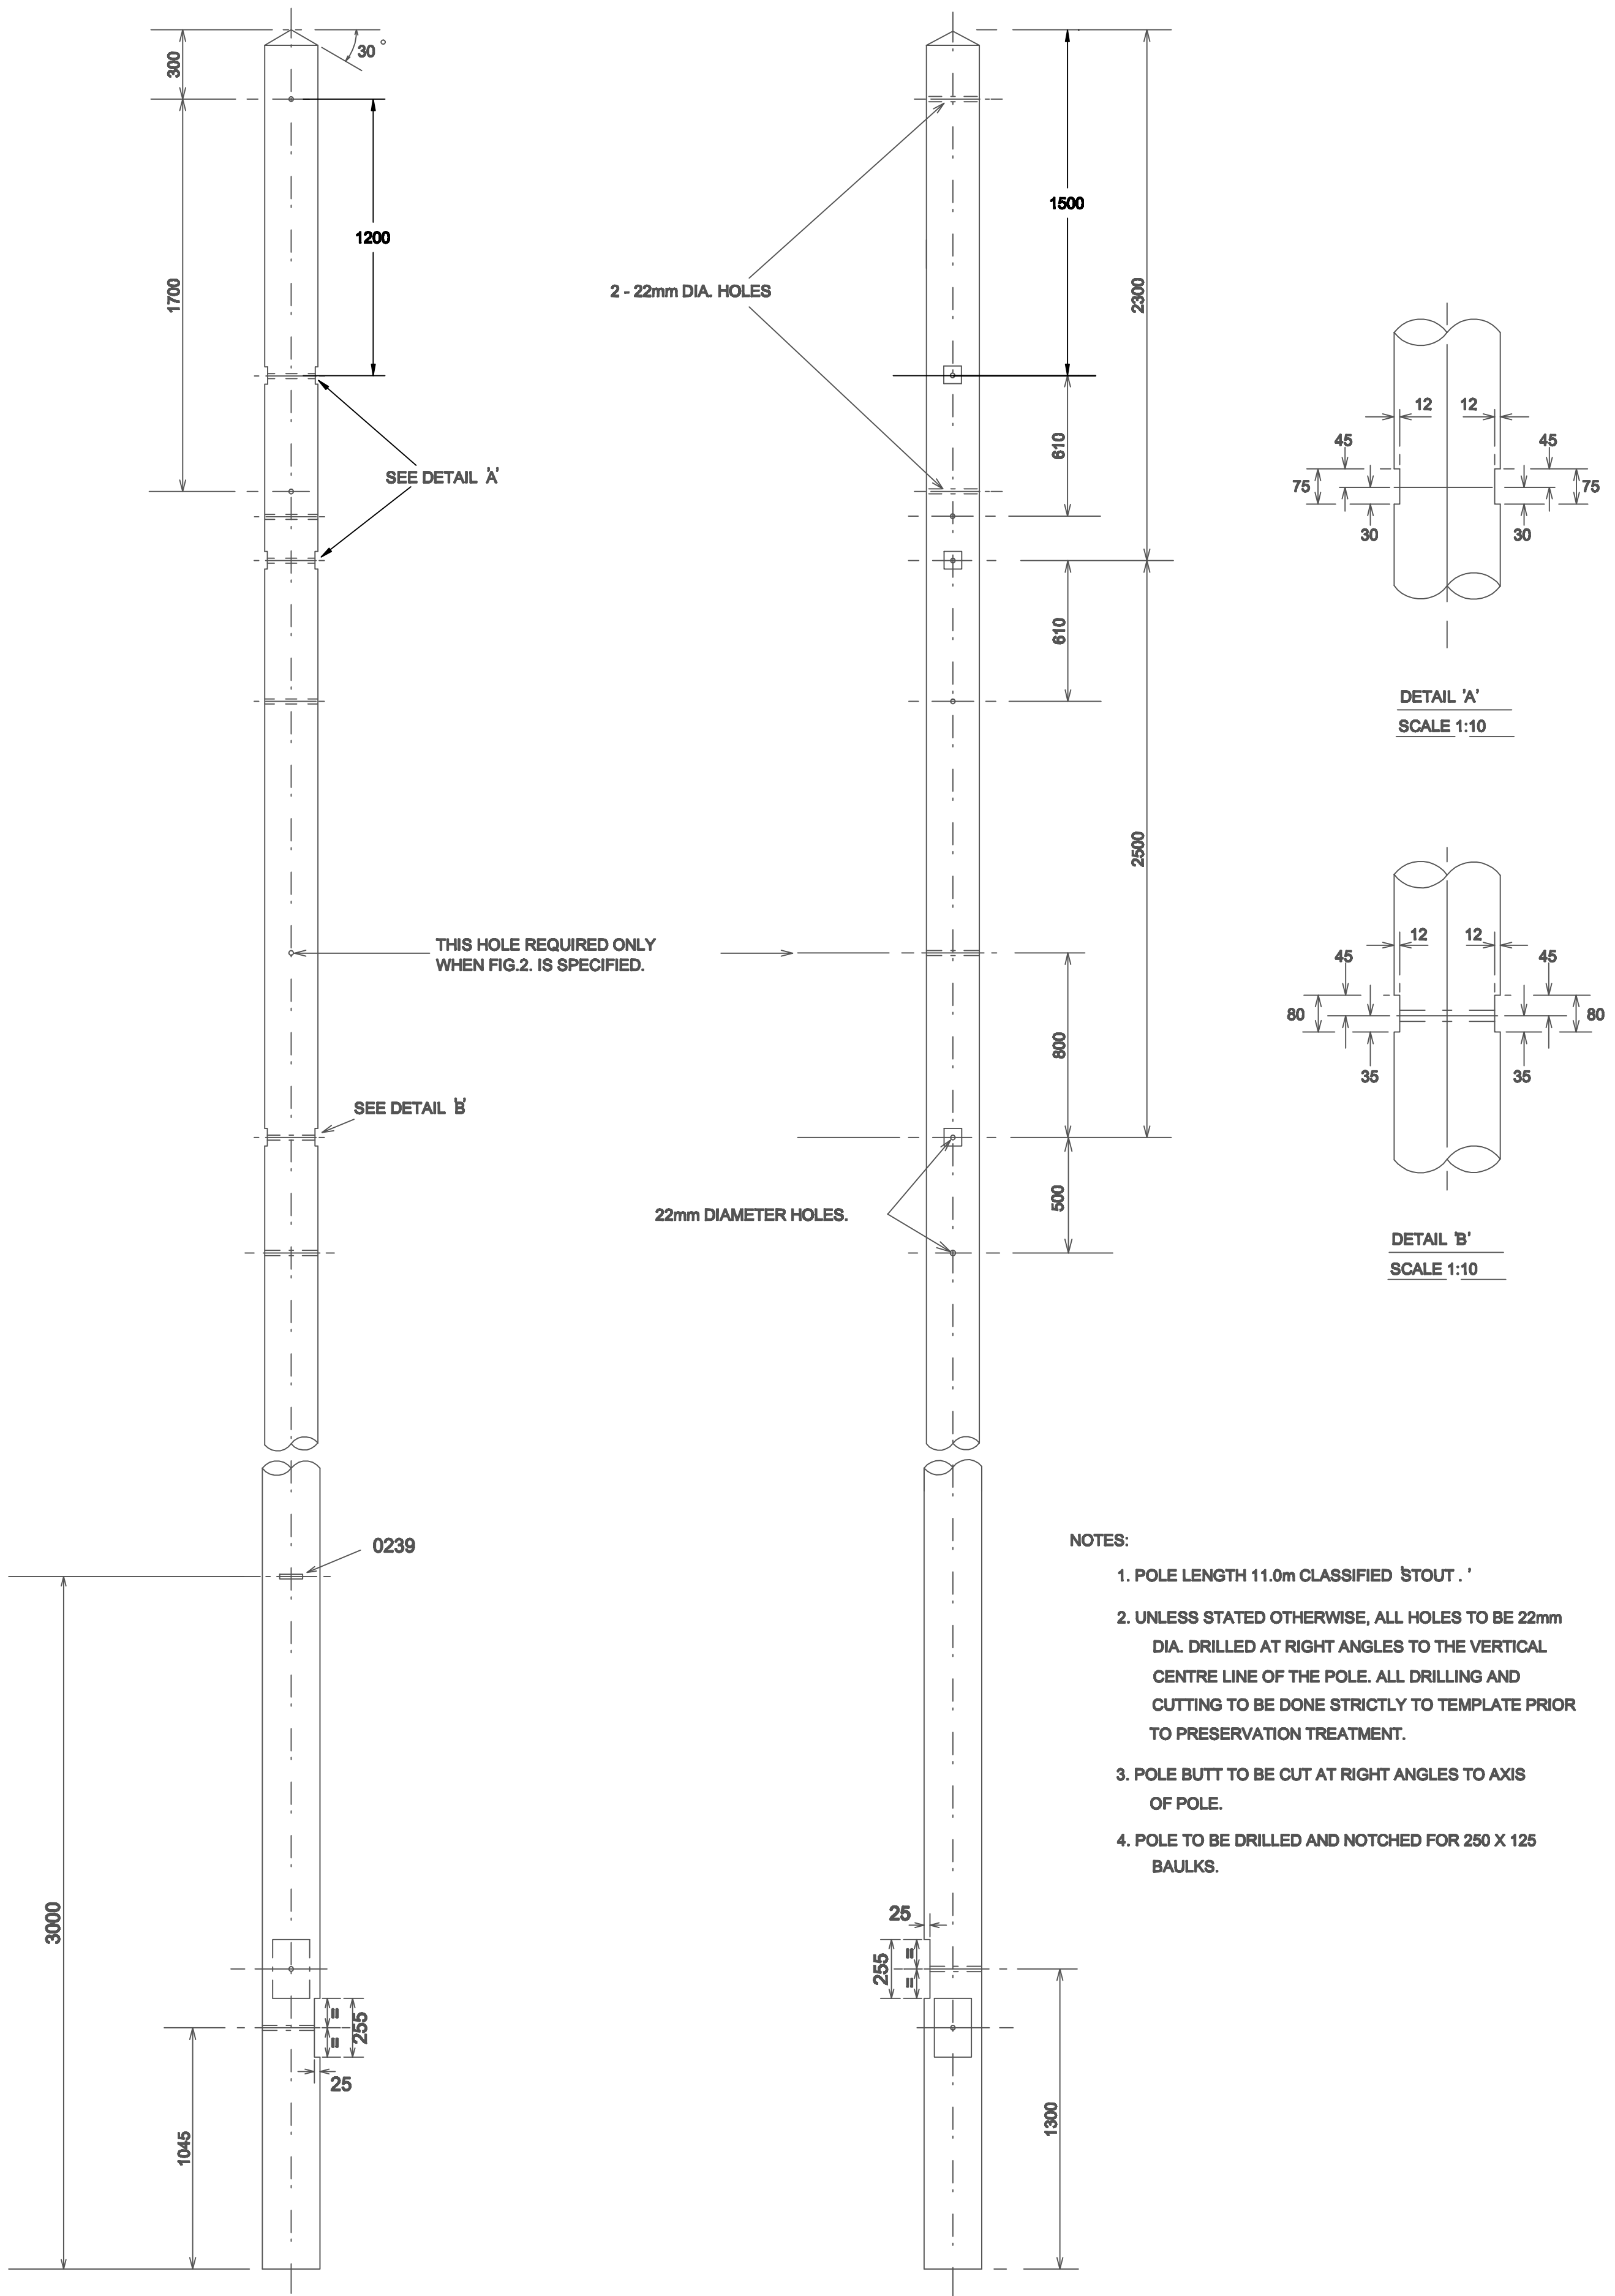

ALL DIMENSIONS SHOWN ARE IN MILLIMETRES UNLESS OTHERWISE STATED.

 NORTHERN POWERGRID		Lloyds Court, 78 Grey Street, Newcastle Upon Tyne, NE1 6AF					
Manufacturer Details		11KV & 20KV OVERHEAD LINES FABRICATION FOR SINGLE PHASE TOTEM POLE SUBSTATION WITH HV FUSE UNITS & HV SUPPLY OFF U/G CABLE & U/G SUPPLY TO LV NETWORK (DRG NO.1.09.107.0819 SHT.3) XXX					
Sheet No.	4					Scale	1:20 & 10
Prepared By J OAKLEY						Type	
Revised 19/02/14	Grid Reference		Ref No.	C101706	Historic Drg.No.	1.09.107.0819	
Date Issued 23/2/05	Checked By G. HAMMEL		Revision	C	Notes		