
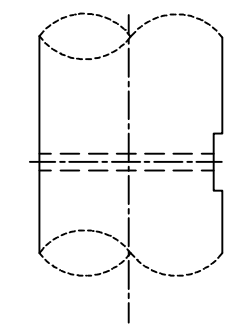
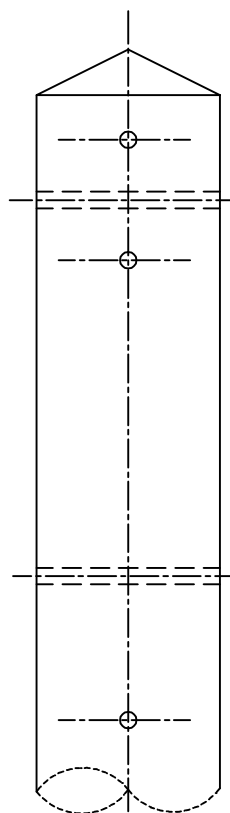
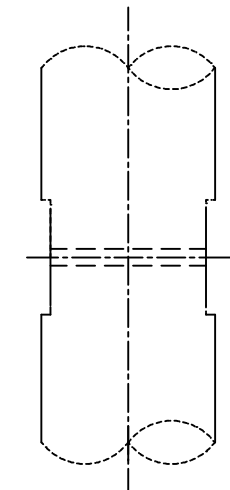
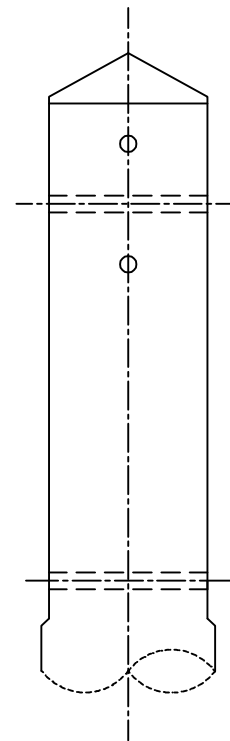


FIG. NUMBERS SUPPLIED	CAT. No.
FIG. 1	237505
FIG. 2	237613
FIG. 3	237473

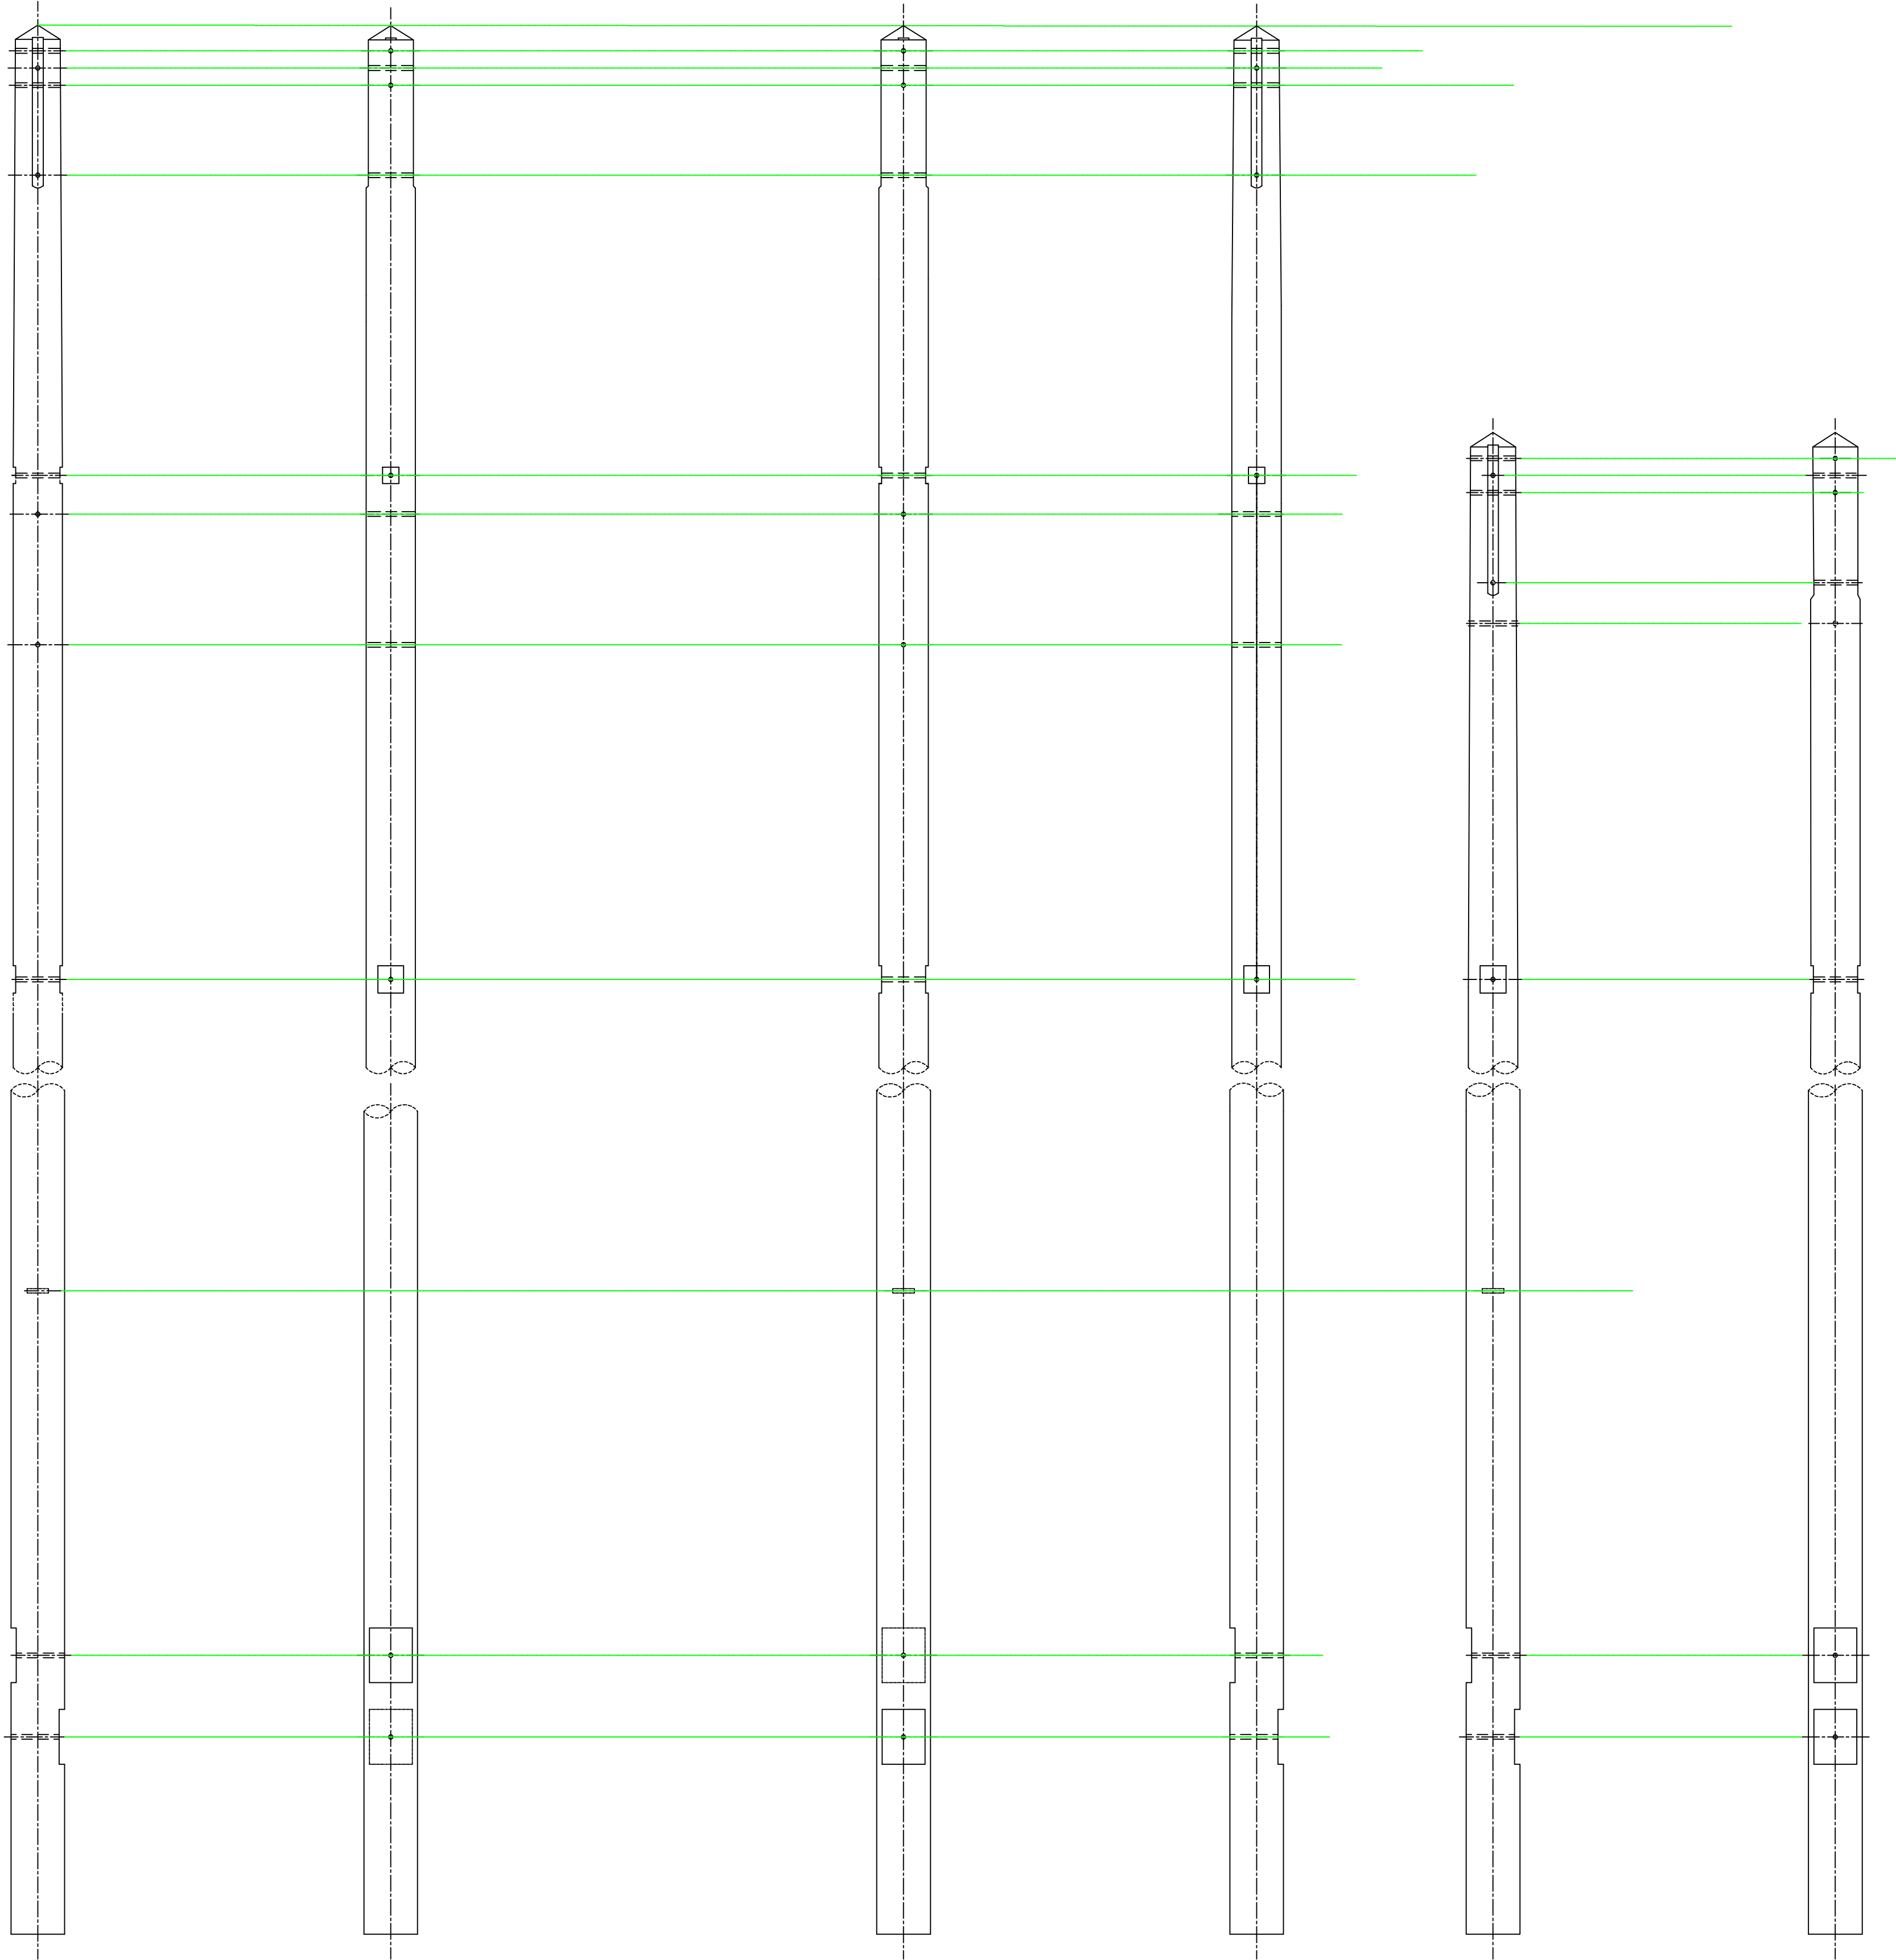

- NOTES:
- 1. LONG LEG - POLE LENGTH 11.0m CLASSIFIED STOUT. } STANDARD POLE LENGTHS
SHORT LEG - POLE LENGTH 9.0m CLASSIFIED STOUT. }
 - 2. WHEN COMPLETE POLE ARRANGEMENTS TO DRG No's 0864 SHT. 1 & 2 ARE REQUIRED, THE ORDERS SHALL QUOTE FABRICATION TO 1.09.108.0864 SHT. 3 FIGS. 1 AND 3 OR 2 AND 3.
 - 3. WHERE A SHORT LEG ONLY IS REQUIRED TO CONVERT EXISTING SINGLE POLE ARRANGEMENTS TO 0864 SHT. 1 OR 2, THE ORDERS SHALL QUOTE FABRICATION TO 1.09.108.0864 SHT. 3 FIG. 3.
 - 4. ALL HOLES SHALL BE 22mm DIA., DRILLED AT RIGHT ANGLES TO VERTICAL CENTRE LINE. ALL DRILLING AND CUTTING TO BE DONE STRICTLY TO TEMPLATE AND PRIOR TO CREOSOTING.
 - 5. ALL UNUSED POLE BOLT HOLES TO BE PLUGGED.

		Lloyds Court, 78 Grey Street, Newcastle Upon Tyne, NE1 6AF	
Manufacturer Details		11 AND 20KV OVERHEAD LINES FABRICATION DETAILS FOR DRAWINGS 1.09.108.0864 SHEET 1 AND SHEET 2	
Sheet No. 3	Scale 1:20	Type OVERHEAD	LINES
Prepared By Joan Oakley	Grid Reference	Ref No. C1007482	Historic Drg.No. 1091080864
Revised 03/03/14	Checked By G HAMMEL	Revision B	Notes
Date Issued 19/03/12			