

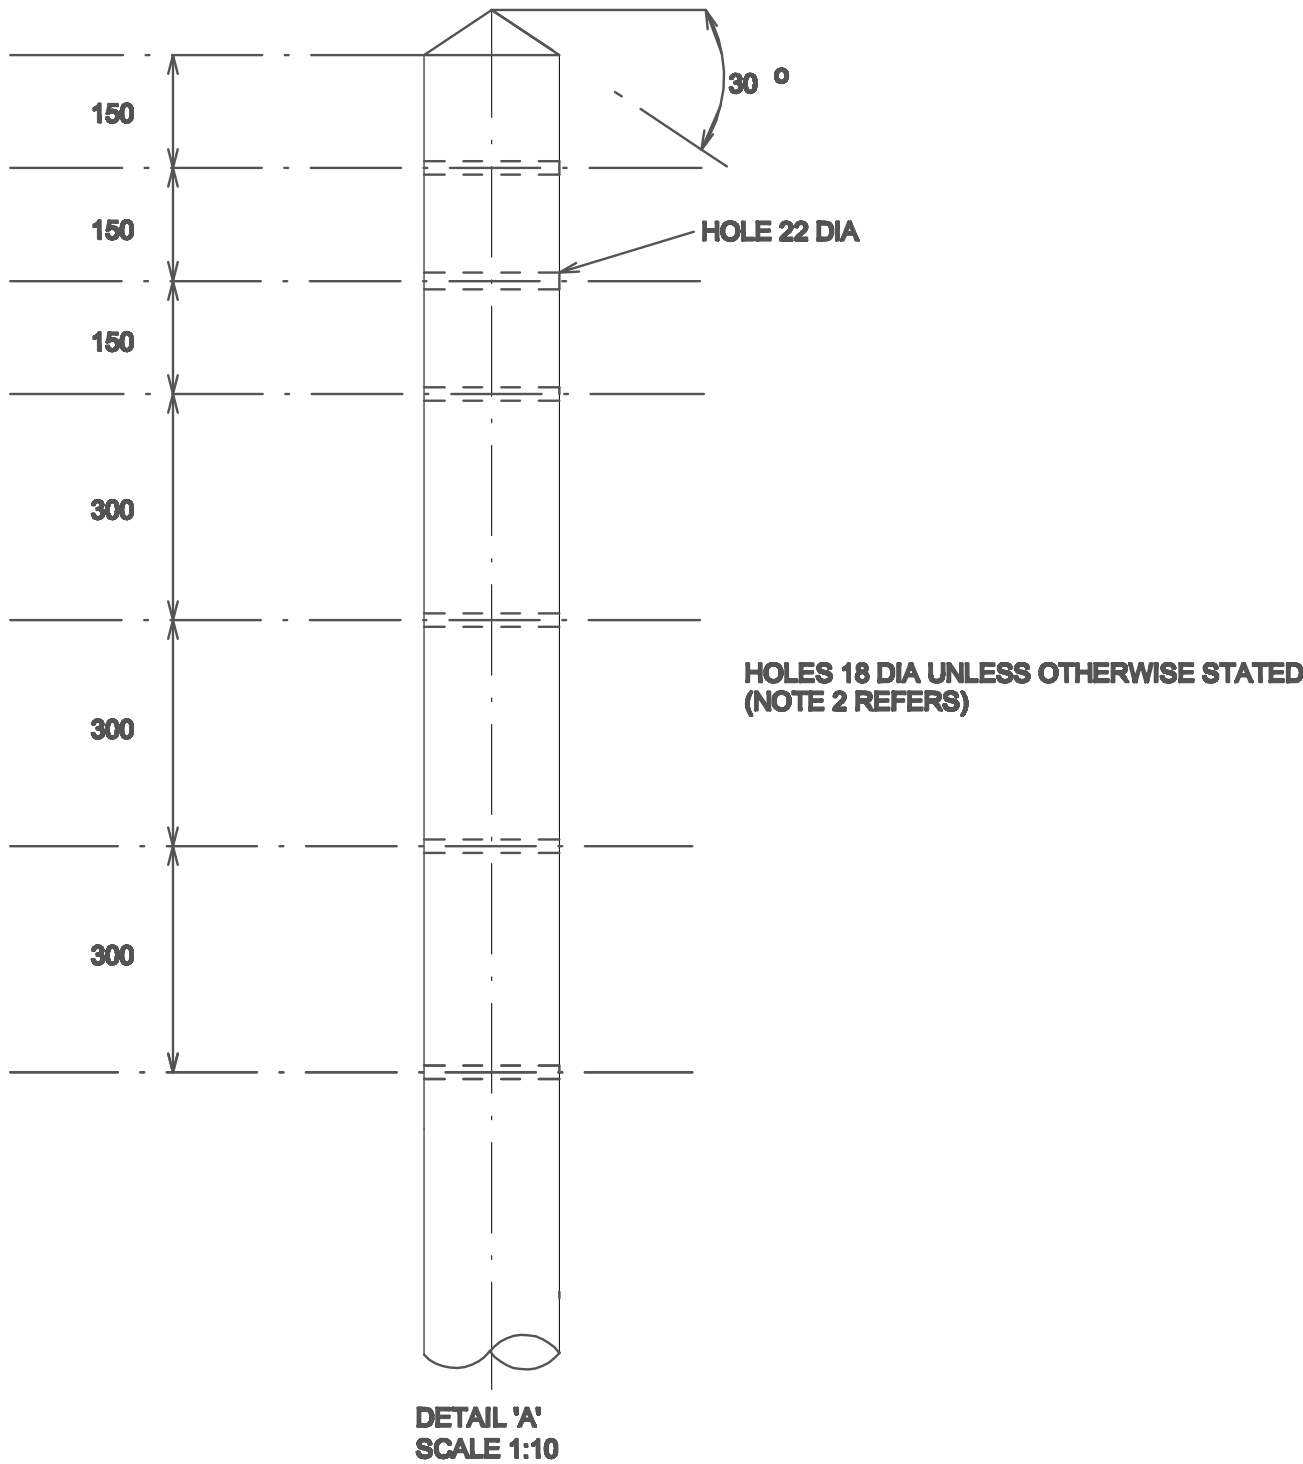


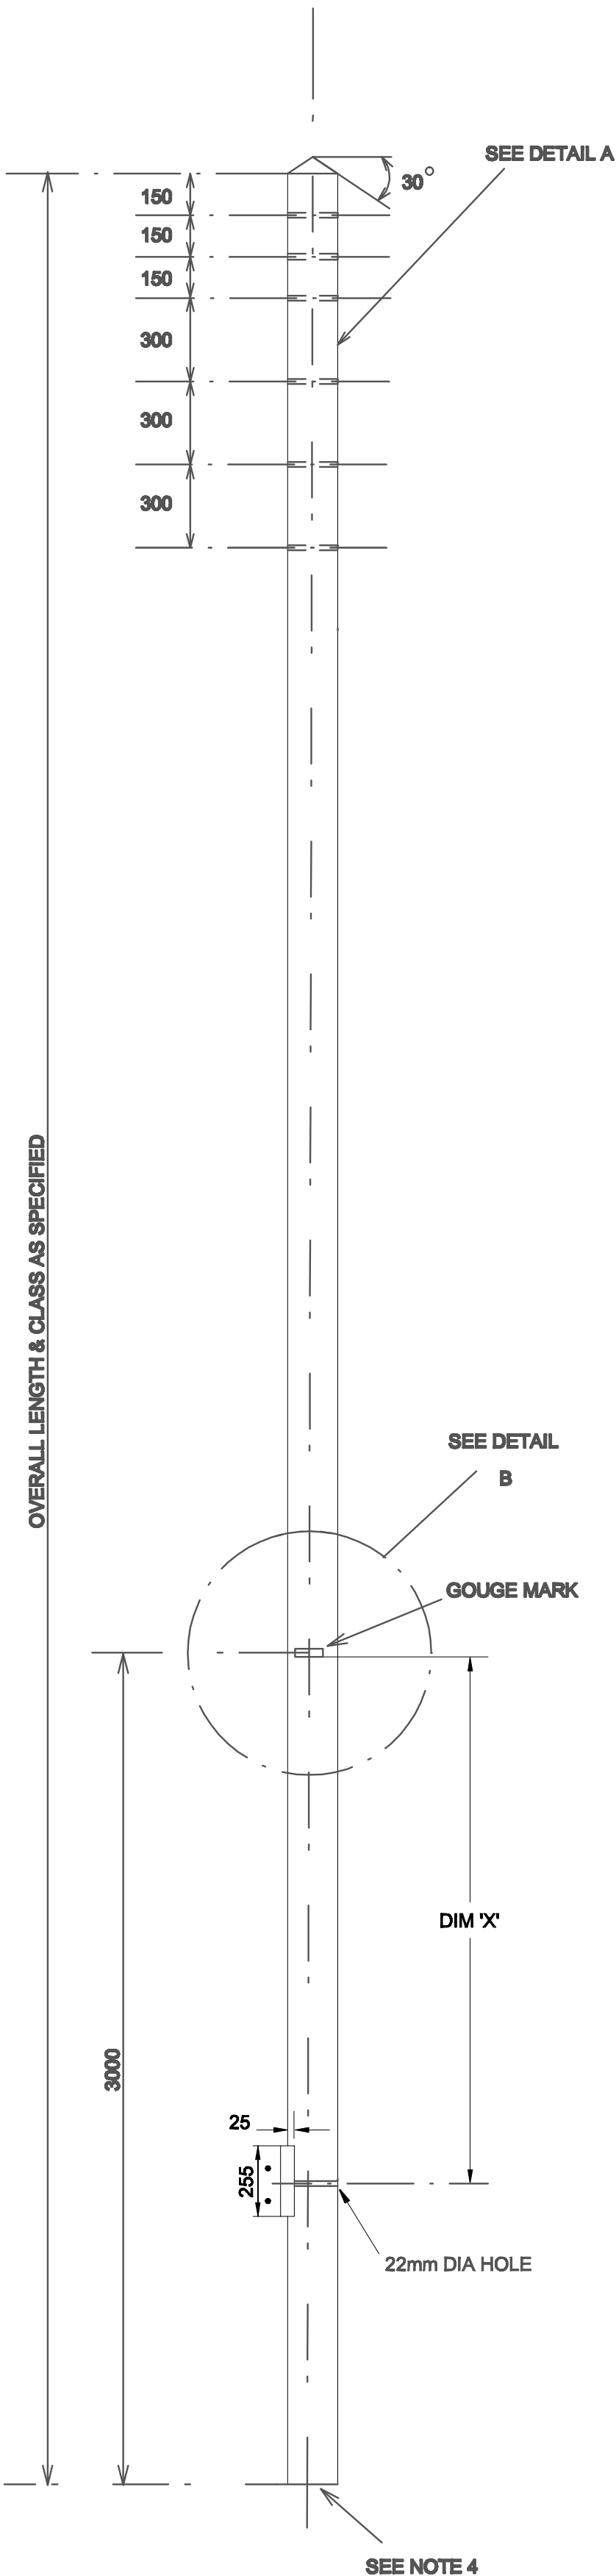

N.B.
CHARACTERS TO BE
50mm HIGH

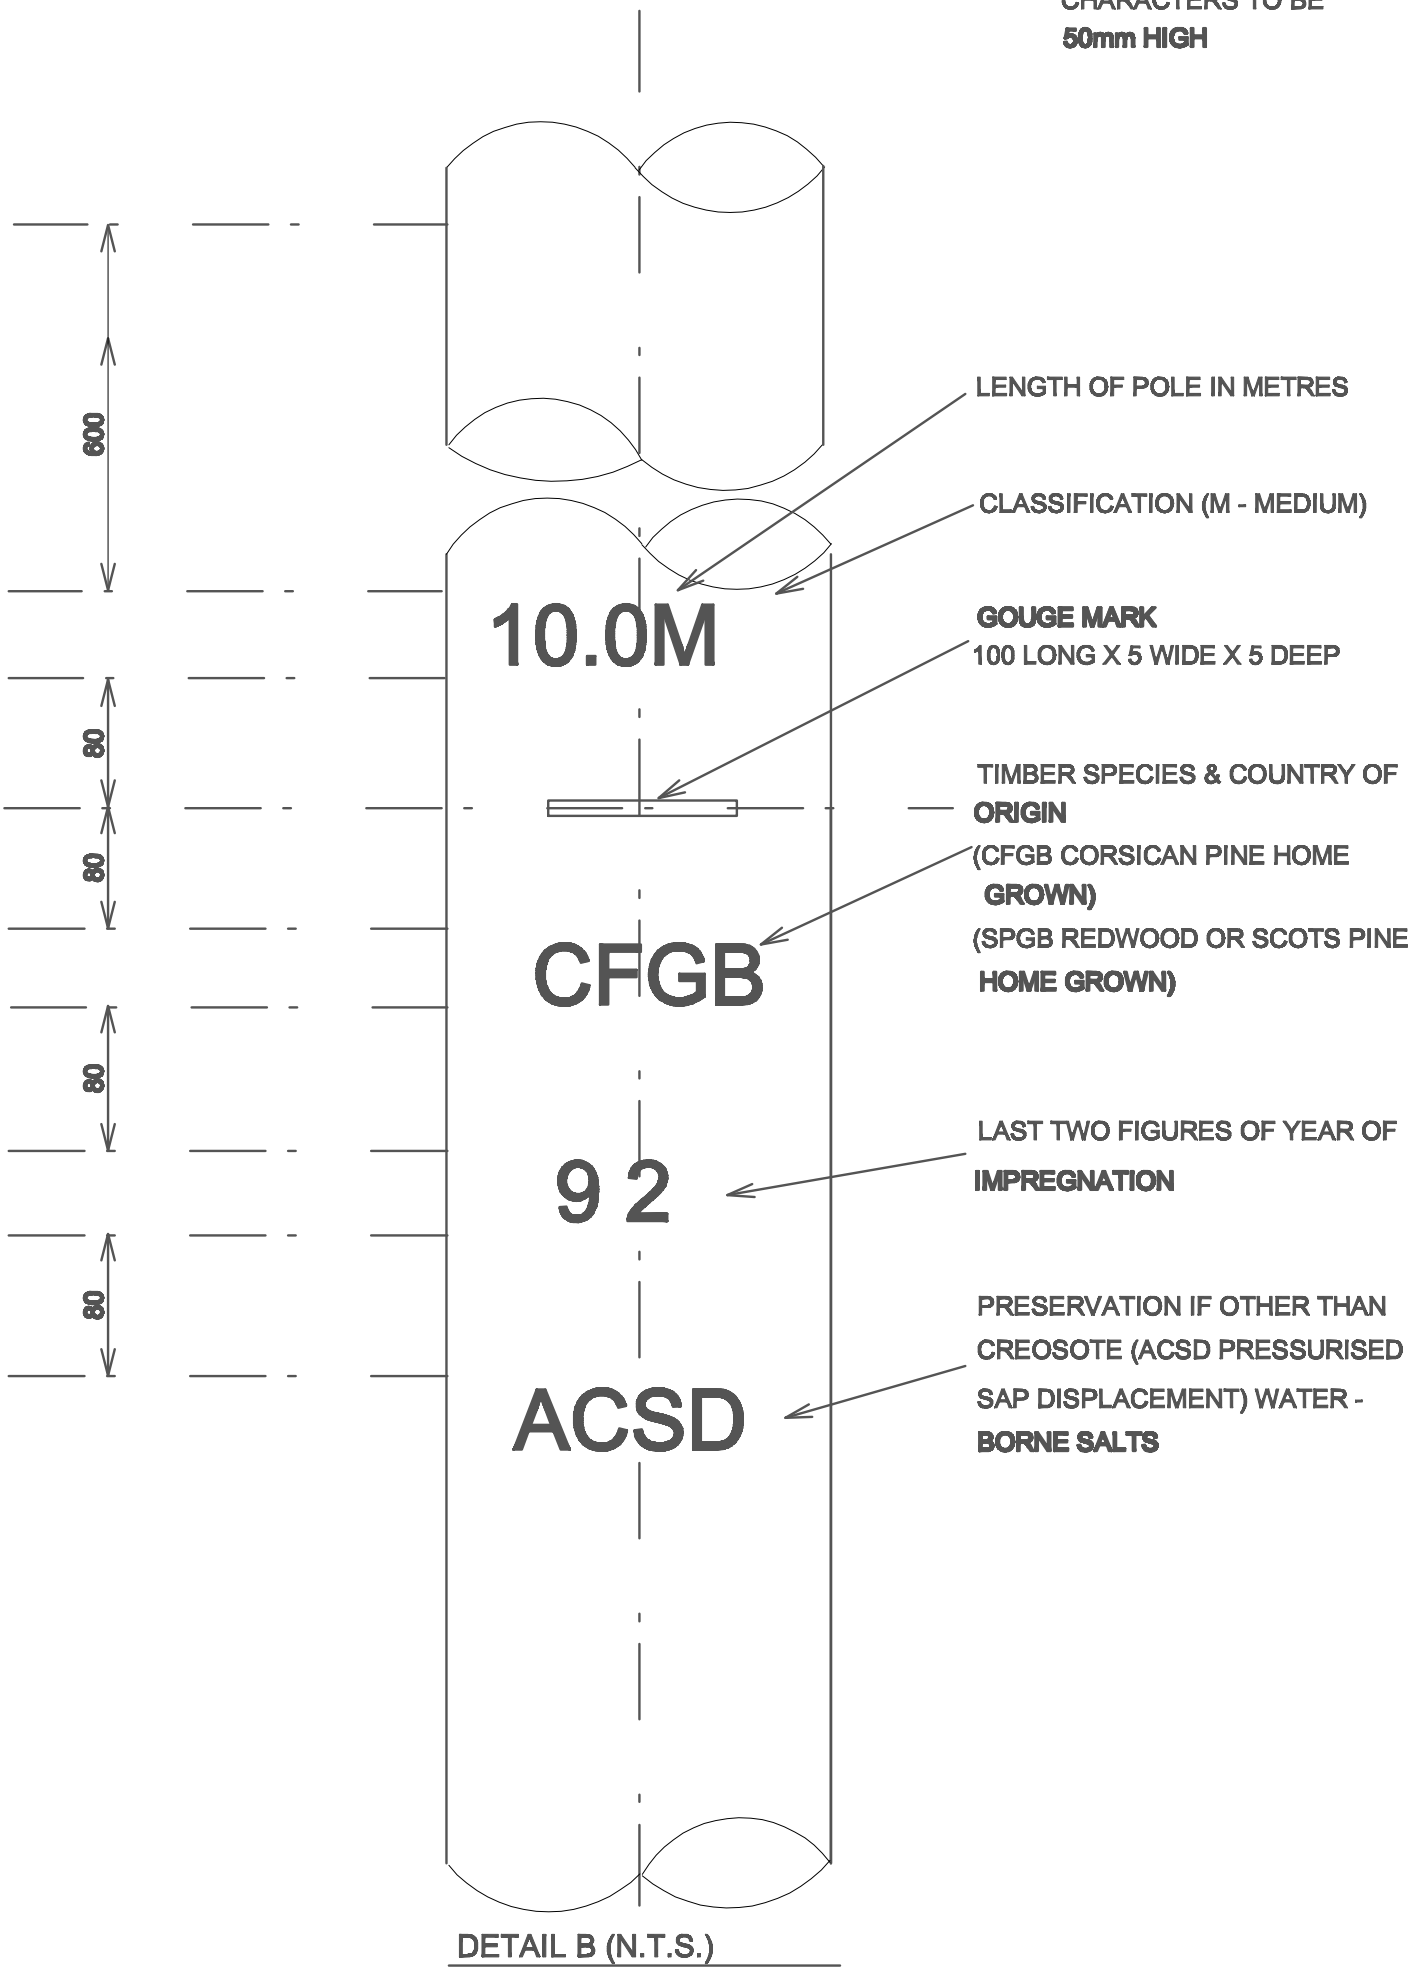

- NOTES:**
- POLES SHALL BE SOURCED, FABRICATED AND TREATED IN ACCORDANCE WITH ENA TS 43-88 AND NPS/001/001. UNLESS STATED OTHERWISE ON THE PROJECT ORDER POLES SHALL BE TREATED WITH CREOSOTE.
 - NUMBER AND SPACING OF HOLES TO BE SPECIFIED.
 - POLE TO BE EVENLY QUARTERED. APEX - 120
 - POLE LENGTH, CLASSIFICATION, DATE OF TREATMENT & SUPPLIERS NAME OR MARK TO BE MARKED ON THE BUTT END GRAIN AND AT THE 3m. GOUGE MARK. THIS MAY BE ACHIEVED BY ENGRAVING THE WOOD OR THE USE OF RECESSED ENGRAVED DISCS. (THE POLE BUTT MAY ALSO EMPLOY THE USE OF METAL MARKER TAPES).
 - BASED ON ESI STANDARD 43-88 APPENDIX N AND ESI DRG No 4330011.
 - HOLES TO BE 18mm DIA UNLESS SPECIFIED OTHERWISE.
- ALL DIMENSIONS SHOWN ARE IN MILLIMETRES UNLESS OTHERWISE STATED

POLE LENGTH (m)	DIMENSION 'X' (mm)	SINKING DEPTH (mm)
9.0 - 10.0	1900	1600
11.0 - 14.0	1700	1800



Manufacturer Details

Sheet No.
3

Scale
1:20

Prepared By
Joan.Oakley

Revised
04/11/13

Date Issued
20/01/05

Grid Reference

Checked By
G HAMMEL

Lloyds Court, 78 Grey Street, Newcastle Upon Tyne, NE1 6AF

LV OVERHEAD LINES
DRILLING AND MARKING OF WOOD
POLES FOR OPEN WIRE AND ABC CONSTRUCTION

Type
OVERHEAD

LINES

Ref No. C101820

Historic
Drg.No.

1091193301

Revision L Notes