



THESE HOLES TO BE DRILLED TO TEMPLATE FROM THIS SIDE OF POLE

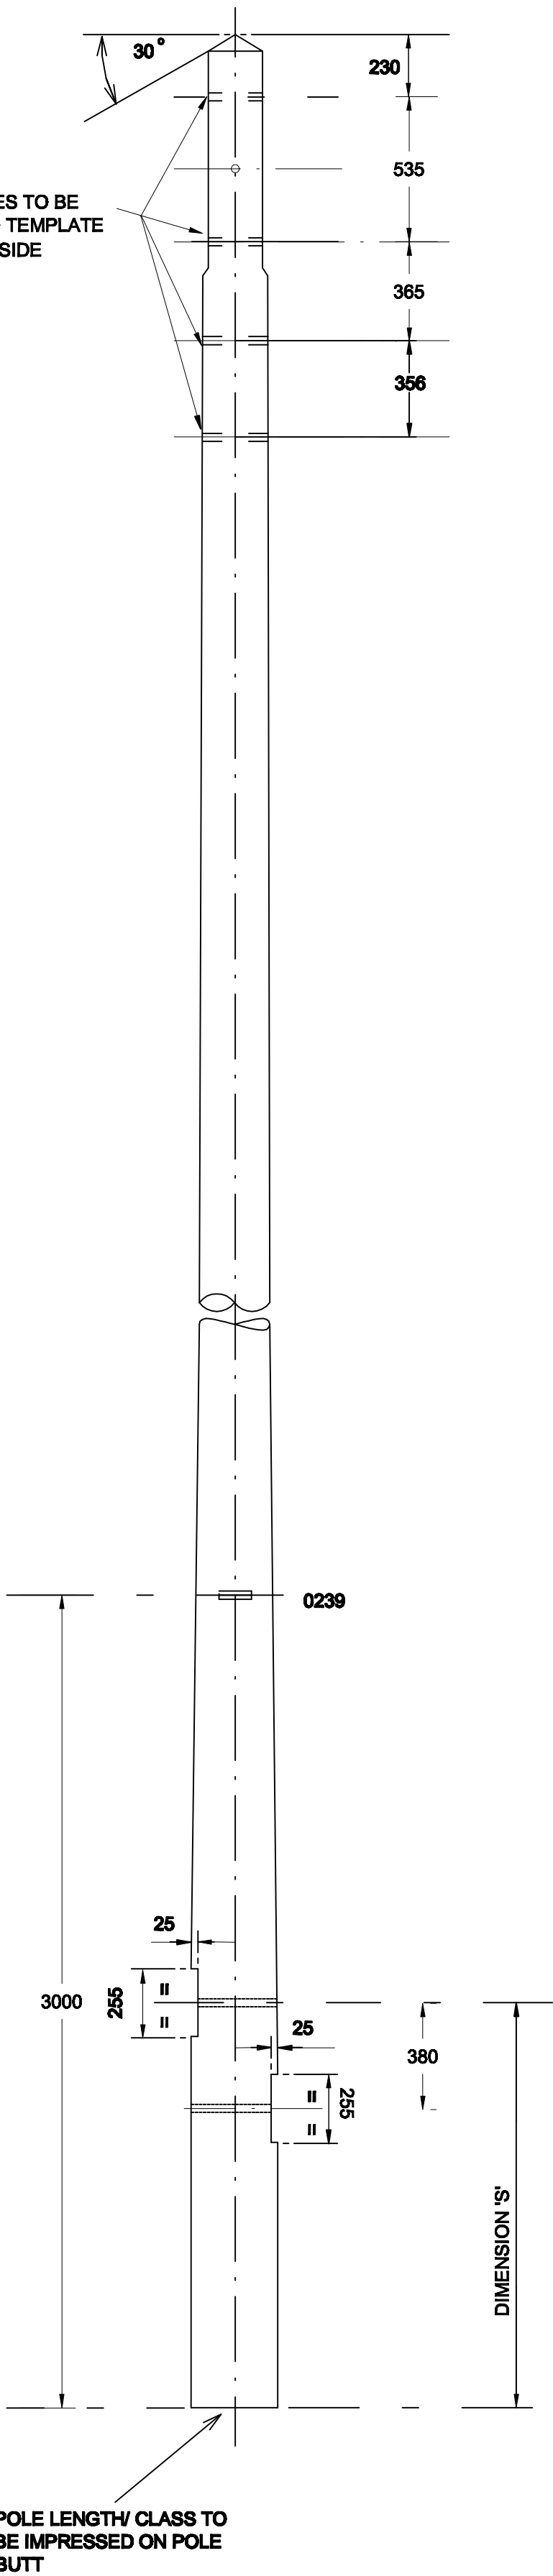

THIS VIEW SHOWS THE POLE FACE (NATURAL LIE OF POLE.)

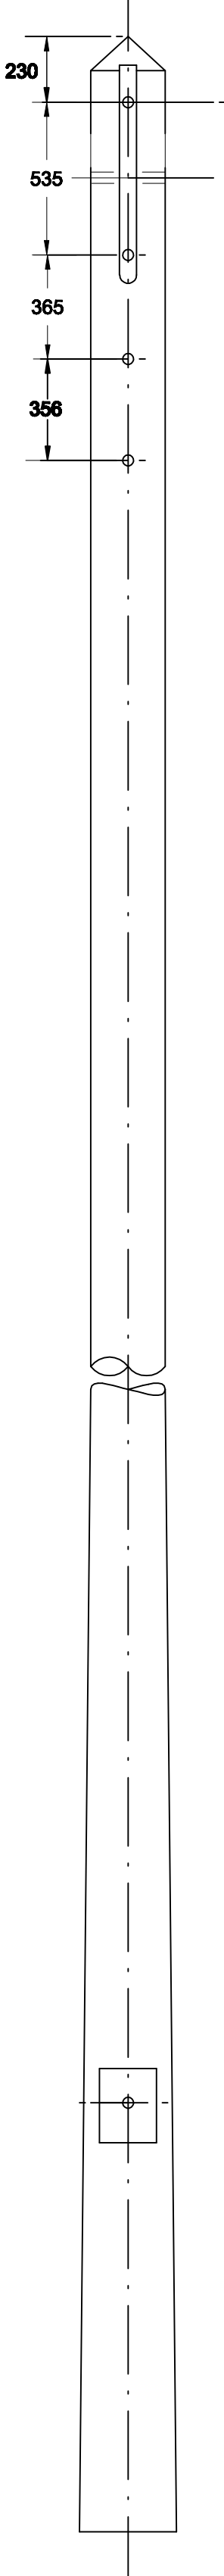

SCARFING TO BE CUT TO GIVE A 50mm WIDE FLAT ON TWO FACES THE ENDS CHAMFERED OFF AS SHOWN.

45° CHAMFER

DETAIL 'A'

NOTES

1. CLASS OF POLE TO BE 'STOUT' OR EXTRA STOUT IN ACCORDANCE WITH 1.09.101.0238
2. POLE BUTT TO BE CUT AT RIGHT ANGLES TO AXIS OF POLE
3. ALL HOLES TO BE 22mm DIA. DRILLED AT RIGHT ANGLES TO VERTICAL CENTRE LINE OF POLE. ALL DRILLING AND CUTTING TO BE DONE STRICTLY TO TEMPLATE PRIOR TO CREOSOTING
4. POLE TO BE NOTCHED AND DRILLED FOR  
1 x 250 x 125 x 2500 AND  
1 x 250 x 125 x 1300 LONG BAULKS
5. EXTRA STOUT POLES TO BE NORMALLY FITTED WITH DOUBLE BAULKS. EXTRA STOUT POLES DESIGNED TO INCREASE WIND SPANS MAY BE UNSUITABLE FOR POOR GROUND CONDITIONS. SEE SPECIFICATION.

| POLE LENGTH             | DIM. 'S' |
|-------------------------|----------|
| 13.0m - 15.0m INCLUSIVE | 2.1      |
| 16.0m - 18.0m INCLUSIVE | 2.1      |
| 20.0m - 24m INCLUSIVE   | 2.5      |

ALL DIMENSIONS SHOWN ARE IN MILLIMETRES UNLESS OTHERWISE STATED



Manufacturer Details

Sheet No.  
2

Scale  
1:20

Prepared By  
Barbara Gordon

Revised  
01/10/14

Date Issued  
01/10/14

Grid Reference

Checked By  
M MOODY

Lloyds Court, 78 Grey Street, Newcastle Upon Tyne, NE1 6AF

132KV SINGLE CIRCUIT OVERHEAD LINES  
DRILLING, SCARFING  
AND MARKING FOR SINGLE  
INTERMEDIATE POLE ARRANGEMENT

Type  
OVERHEAD

POLES

Ref No.  
C1040650

Historic  
Drg.No.

1091380006

Revision

Notes