
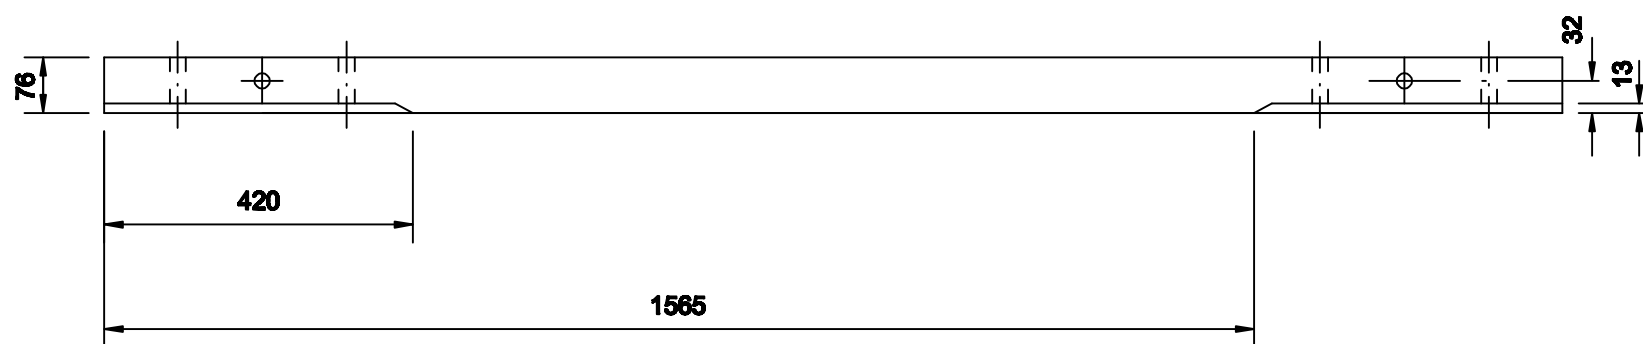


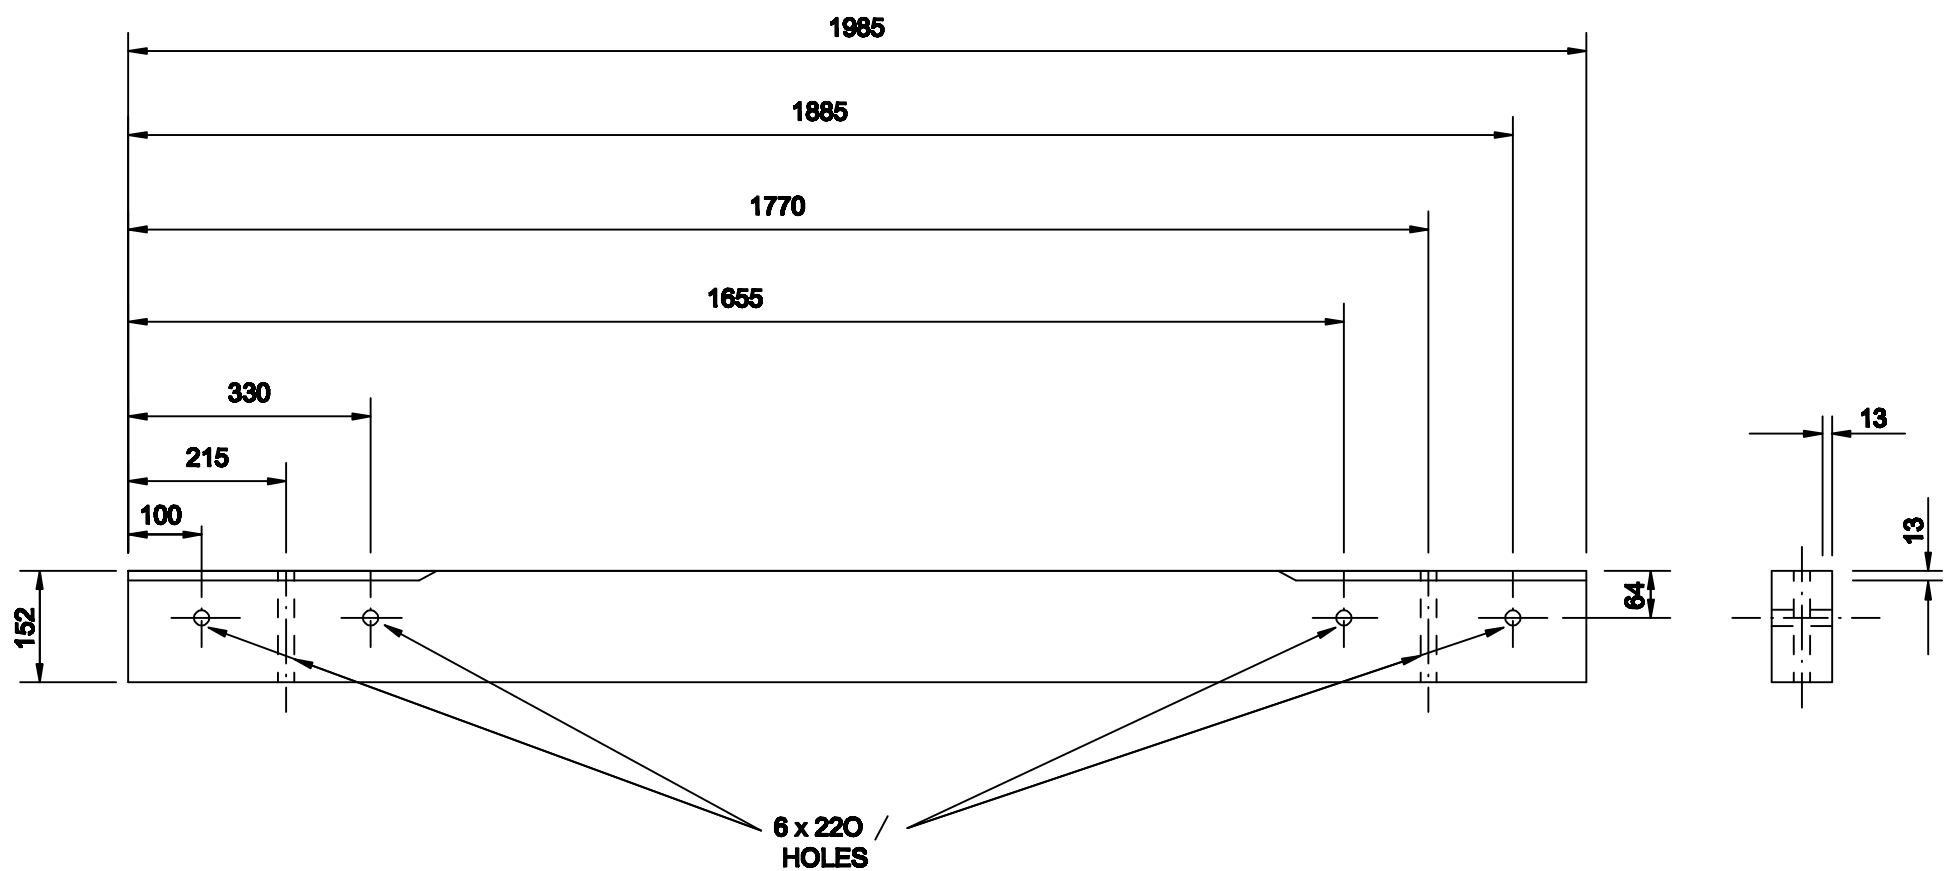

NOTE
 ALL DIMENSIONS TO BE FINISHED DIMENSIONS WITH TIMBERSMOOTH FINISHED
 ALL HOLES TO BE TEMPLATE DRILLED
 HOLES TO BE DRILLED FROM SCARFED FACES

MATERIAL: BEST QUALITY SELECTED PURPLEHEART TIMBER

FORMERLY DRG. Y205L0904

		Lloyds Court, 78 Grey Street, Newcastle Upon Tyne, NE1 6AF	
		TIMBER INSERT FOR CROSSARMS OVERHEAD LINE SPEC DC1	
Manufacturer Details			
Sheet No. 1	Scale 1:10		
Prepared By Barbara.Gordon		Type OVERHEAD	LINES
Revised 01/10/14	Grid Reference	Ref No. C1040655	Historic Drg.No. 1091380007
Date Issued 01/10/14	Checked By G HAMMEL	Revision	Notes