



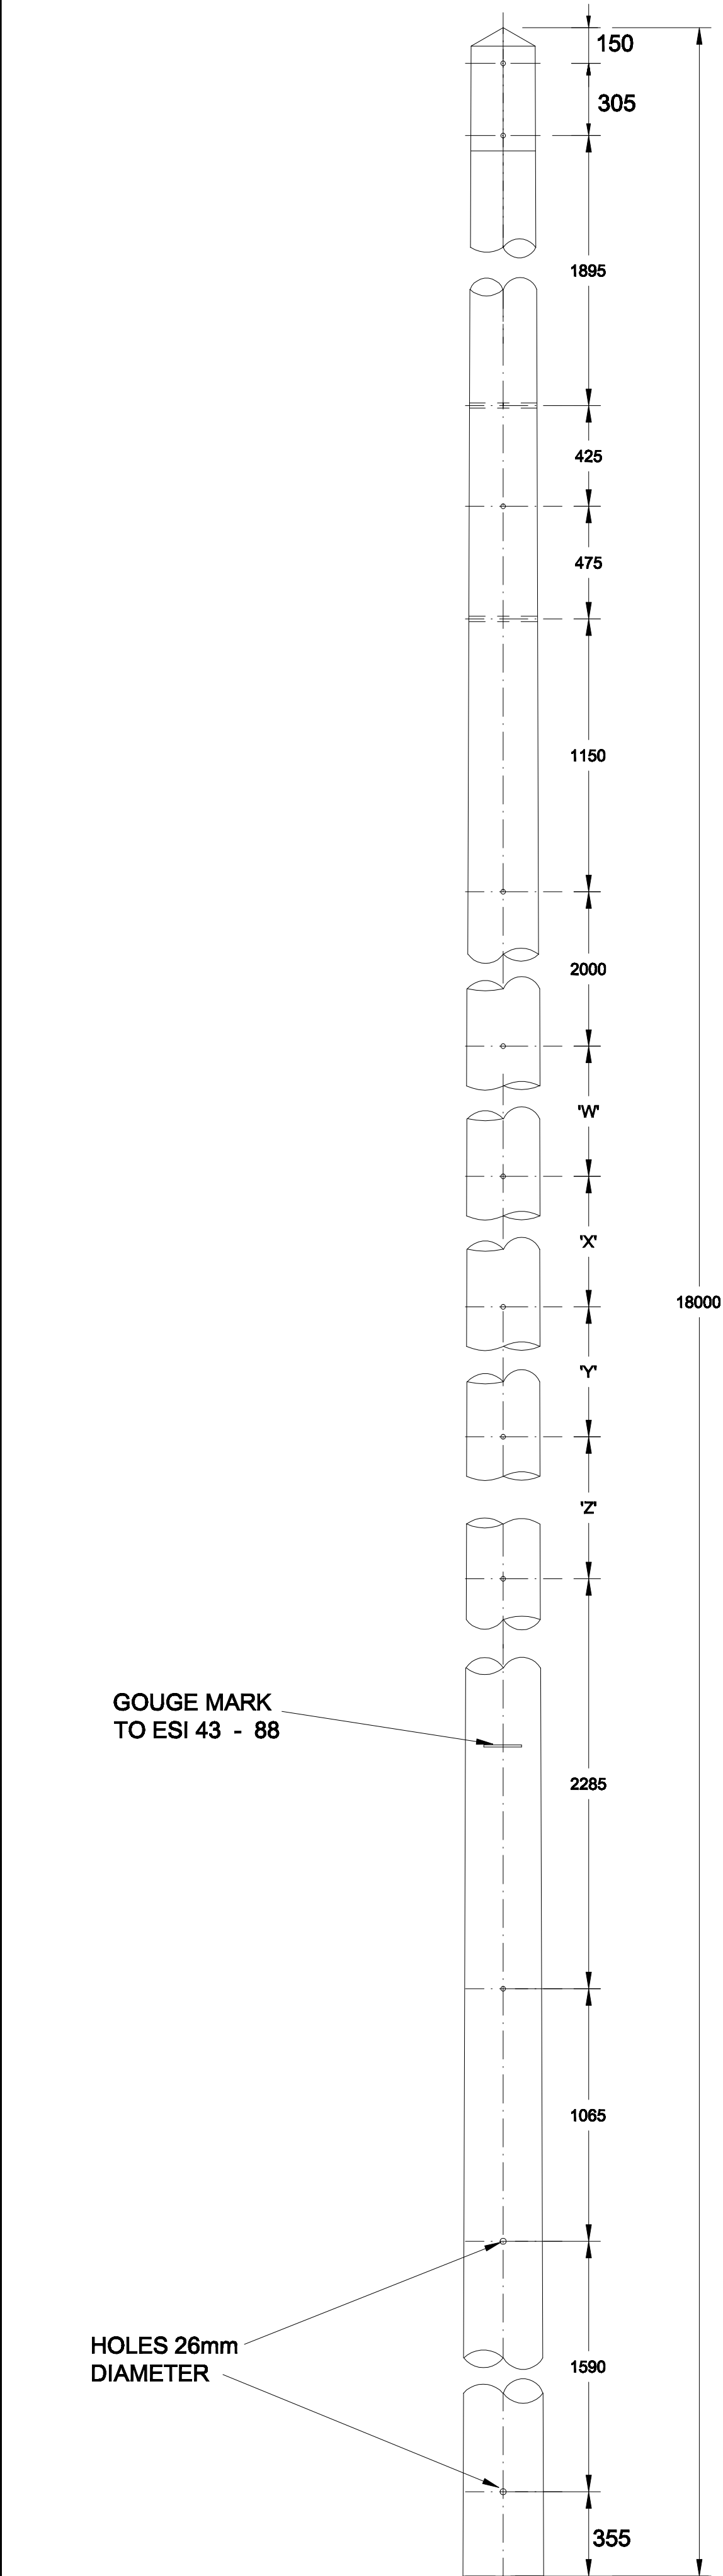

ALL DIMENSIONS SHOWN ARE IN MILLIMETRES UNLESS OTHERWISE STATED

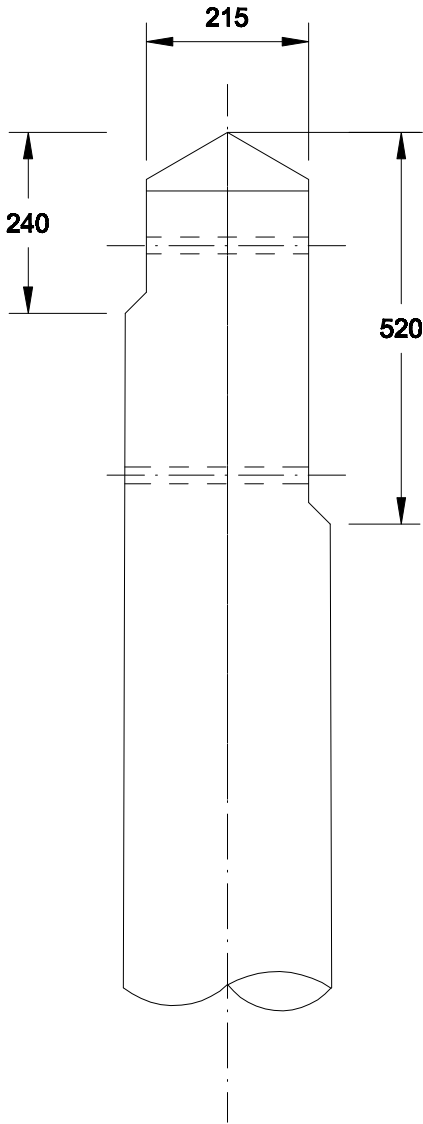

SCALE 1:10

NOTES

- POLES TO BE "STOUT " CLASS
- POLES TO BE MATCHED FOR "H" STRUCTURES. EACH PAIR OF POLES TO BE MARKED WITH IDENTICAL PAIRING NUMBERS
- ALL HOLES TO BE 22mm DIAMETER (EXCEPT WHERE STATED) TO BE DRILLED AT RIGHT ANGLES TO THE CENTRE LINE OF THE POLE. ALL DRILLING AND CUTTING TO BE DONE STRICTLY TO TEMPLATE PRIOR TO PRESERVATION TREATMENT

POLE LENGTH	DIM 'W'	DIM 'X'	DIM 'Y'	DIM 'Z'
18.0m	2000	2000	2000	305
17.0m	2000	2000	1455	0
16.0m	2000	2000	455	0
15.0m	2000	1605	0	0
14.0m	2000	605	0	0
13.0m	1705	0	0	0
12.0m	705	0	0	0
11.5m	405	0	0	0

FORMERLY YE DRAWING No Y204L0606 sheet 8

NORTHERN POWERGRID Manufacturer Details		Lloyds Court, 78 Grey Street, Newcastle Upon Tyne, NE1 6AF			
		POLE FABRICATION FOR 66KV POLYMERIC CABLE TERMINATION WITH PORCELAIN TYPE MB75 SURGE DIVERSERS CE/C/37 (M1)			
		Sheet No. 1		Scale 1:20	
Prepared By Barbara Gordon		Type OVERHEAD		POLES	
Revised 01/10/14	Grid Reference	Ref No.	C1040654	Historic Drg.No.	1091380009
Date Issued 01/10/14	Checked By G HAMMEL	Revision	Notes		