


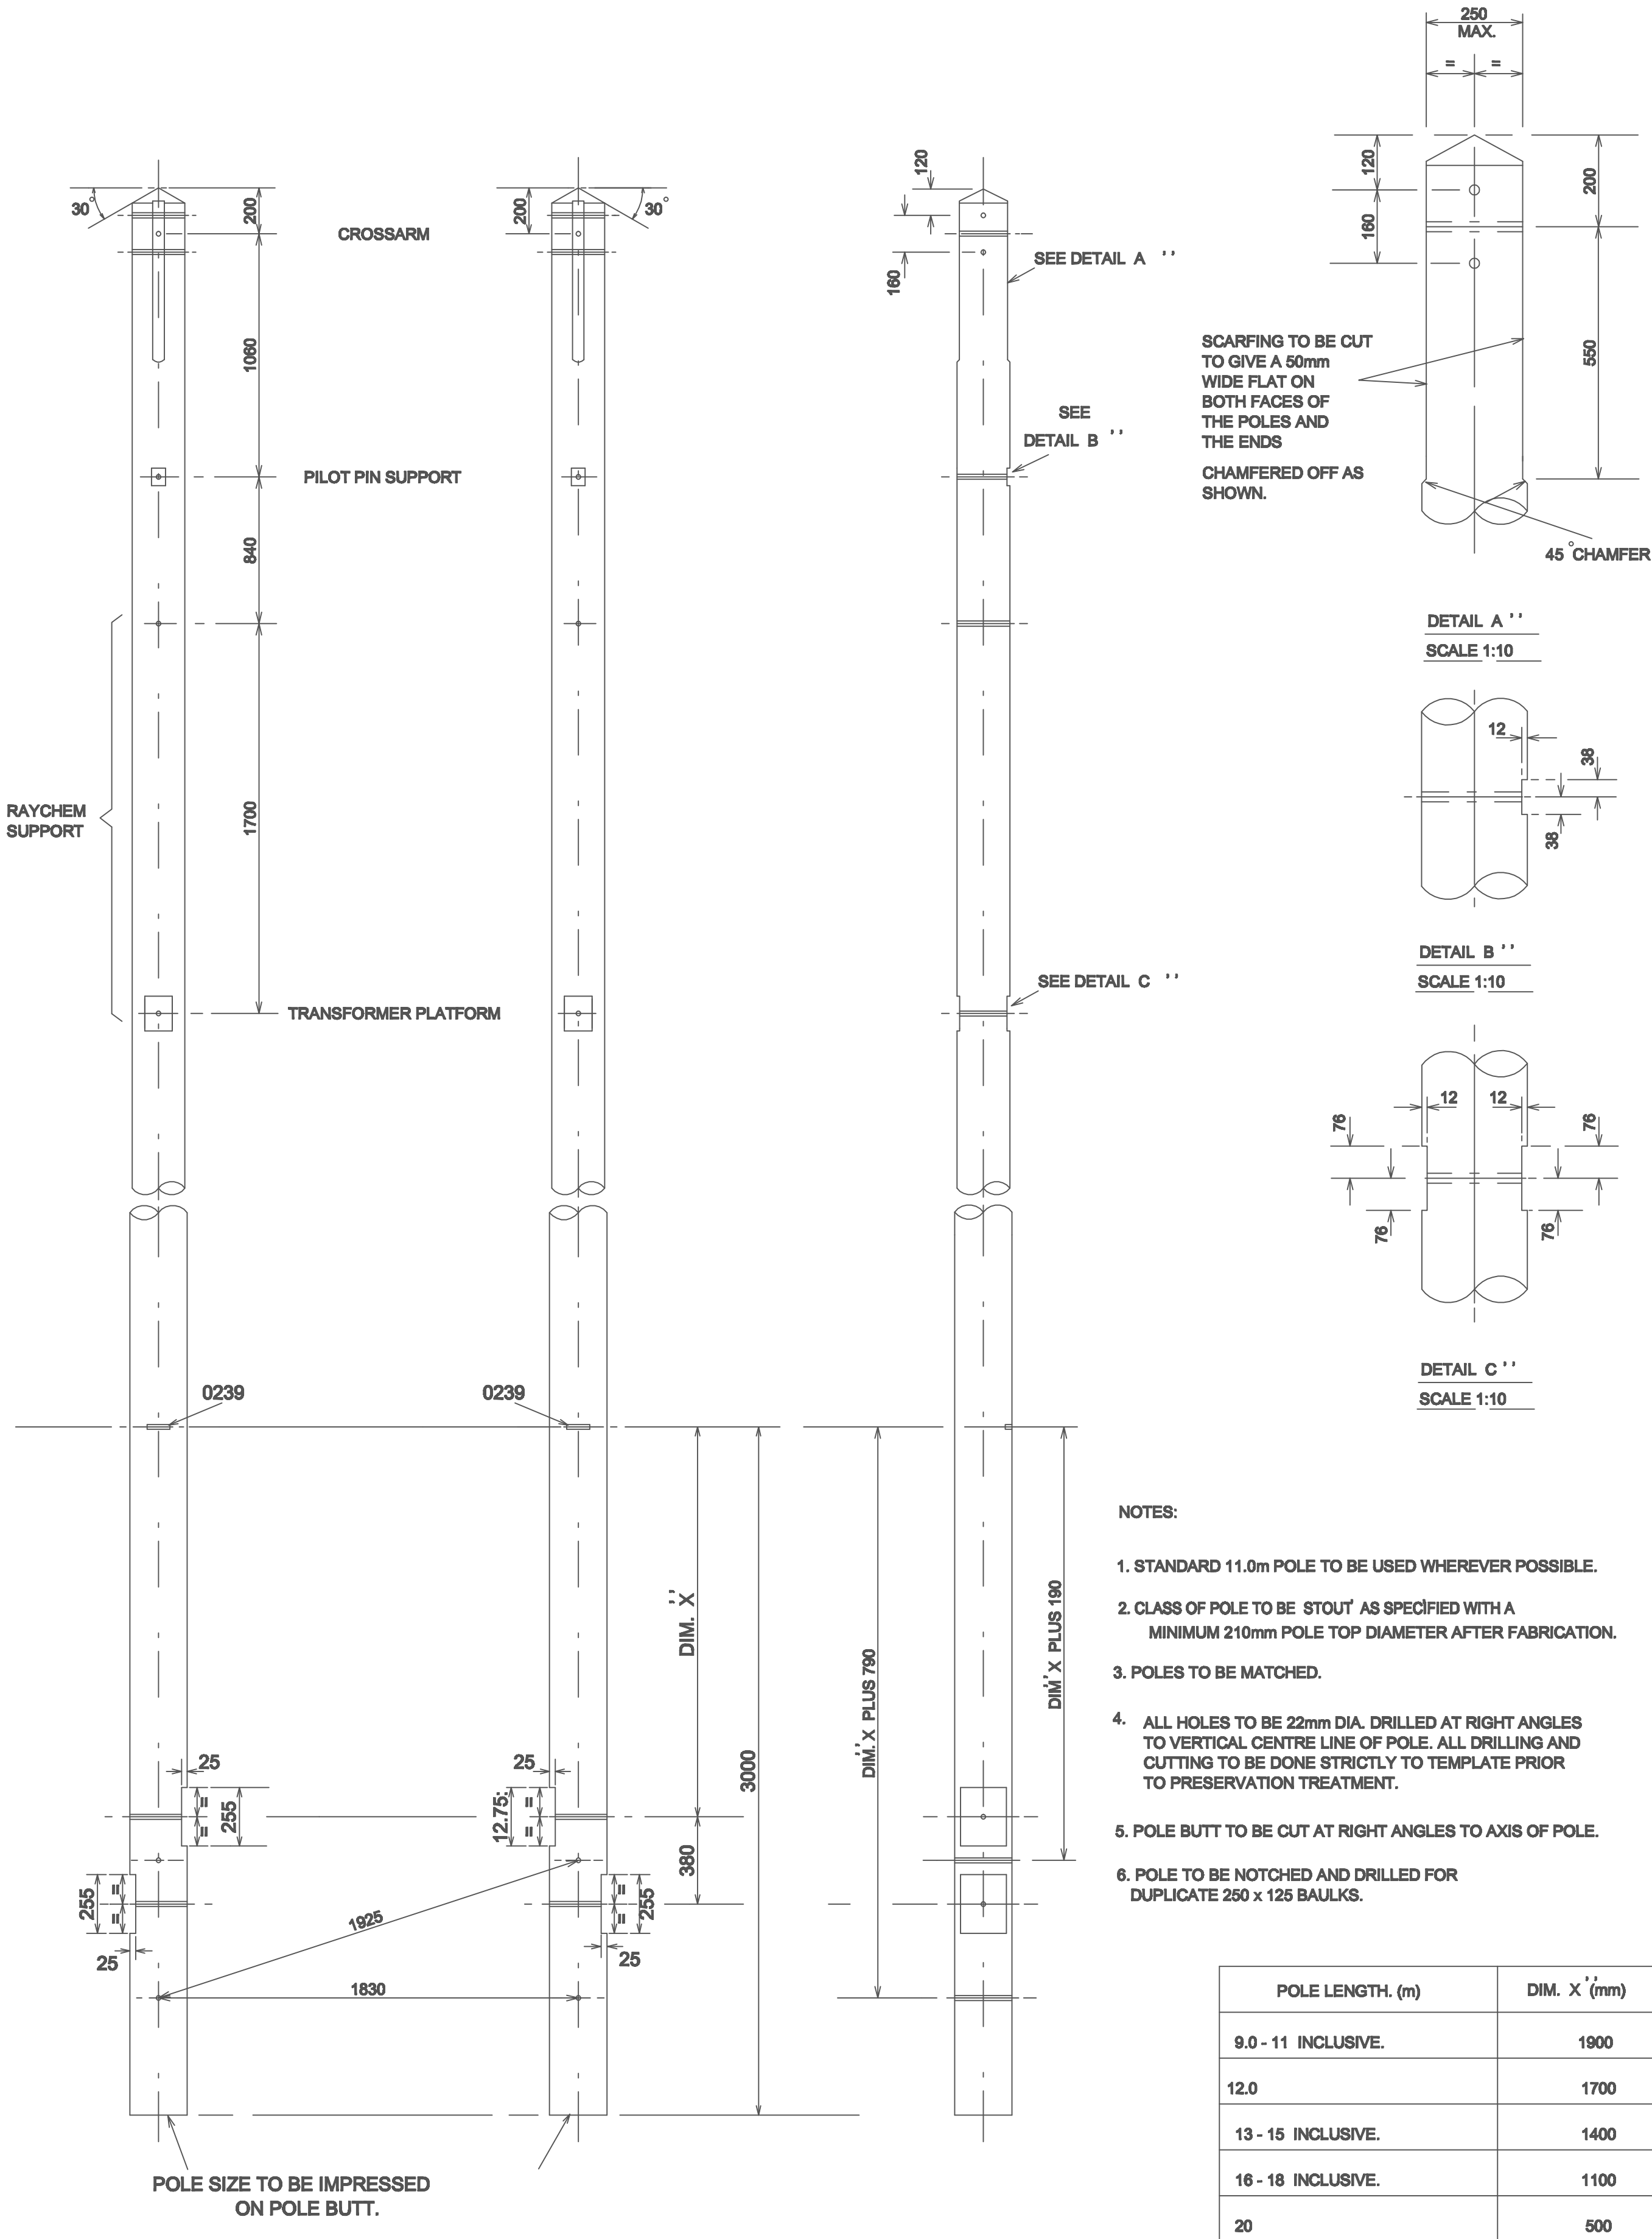

FABRICATION DRAWING FOR USE WITH THE FOLLOWING ARRANGEMENT DRAWINGS:

- DRG.No. 1.00.043.4006 SHEET 1.
- DRG.No. 1.00.043.4007 SHEET 1 & 2.
- DRG.No. 1.00.043.4011 SHEET 1.
- DRG.No. 1.00.043.4011 SHEET 6.
- DRG.No. 1.09.108.0860 SHEET 1.
- DRG.No. 1.09.108.0860 SHEET 3.

ALL DIMENSIONS SHOWN ARE IN MILLIMETRES UNLESS OTHERWISE STATED.

		Lloyds Court, 78 Grey Street, Newcastle Upon Tyne, NE1 6AF	
Manufacturer Details		HV OVERHEAD LINES MULTI-FABRICATION 'H' POLE SUITABLE FOR LINE SECTION OR TERMINAL ARRANGEMENT & PLANT RELATED CABLE OR PLATFORM MOUNTED TRANSFORMER	
Sheet No. 2	Scale 1:20	Type ESI	ESI
Prepared By Janis.Webb	Grid Reference	Ref No. C147654	Historic Drg.No. 1000434002
Revised 24/04/06	Checked By G HAMMEL	Revision C	Notes
Date Issued 23/02/05			