

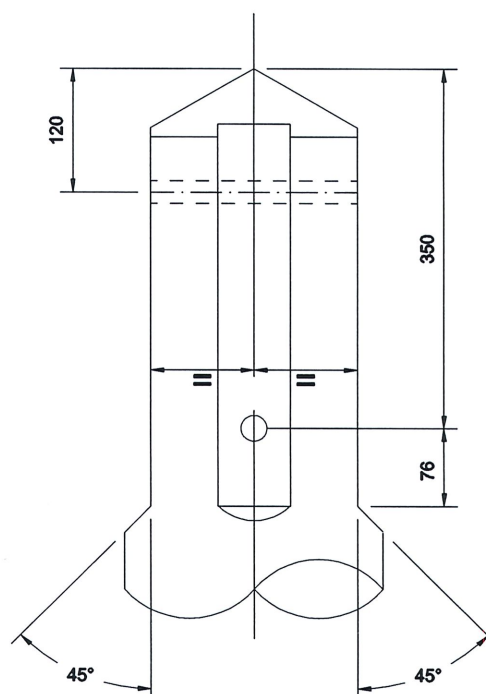


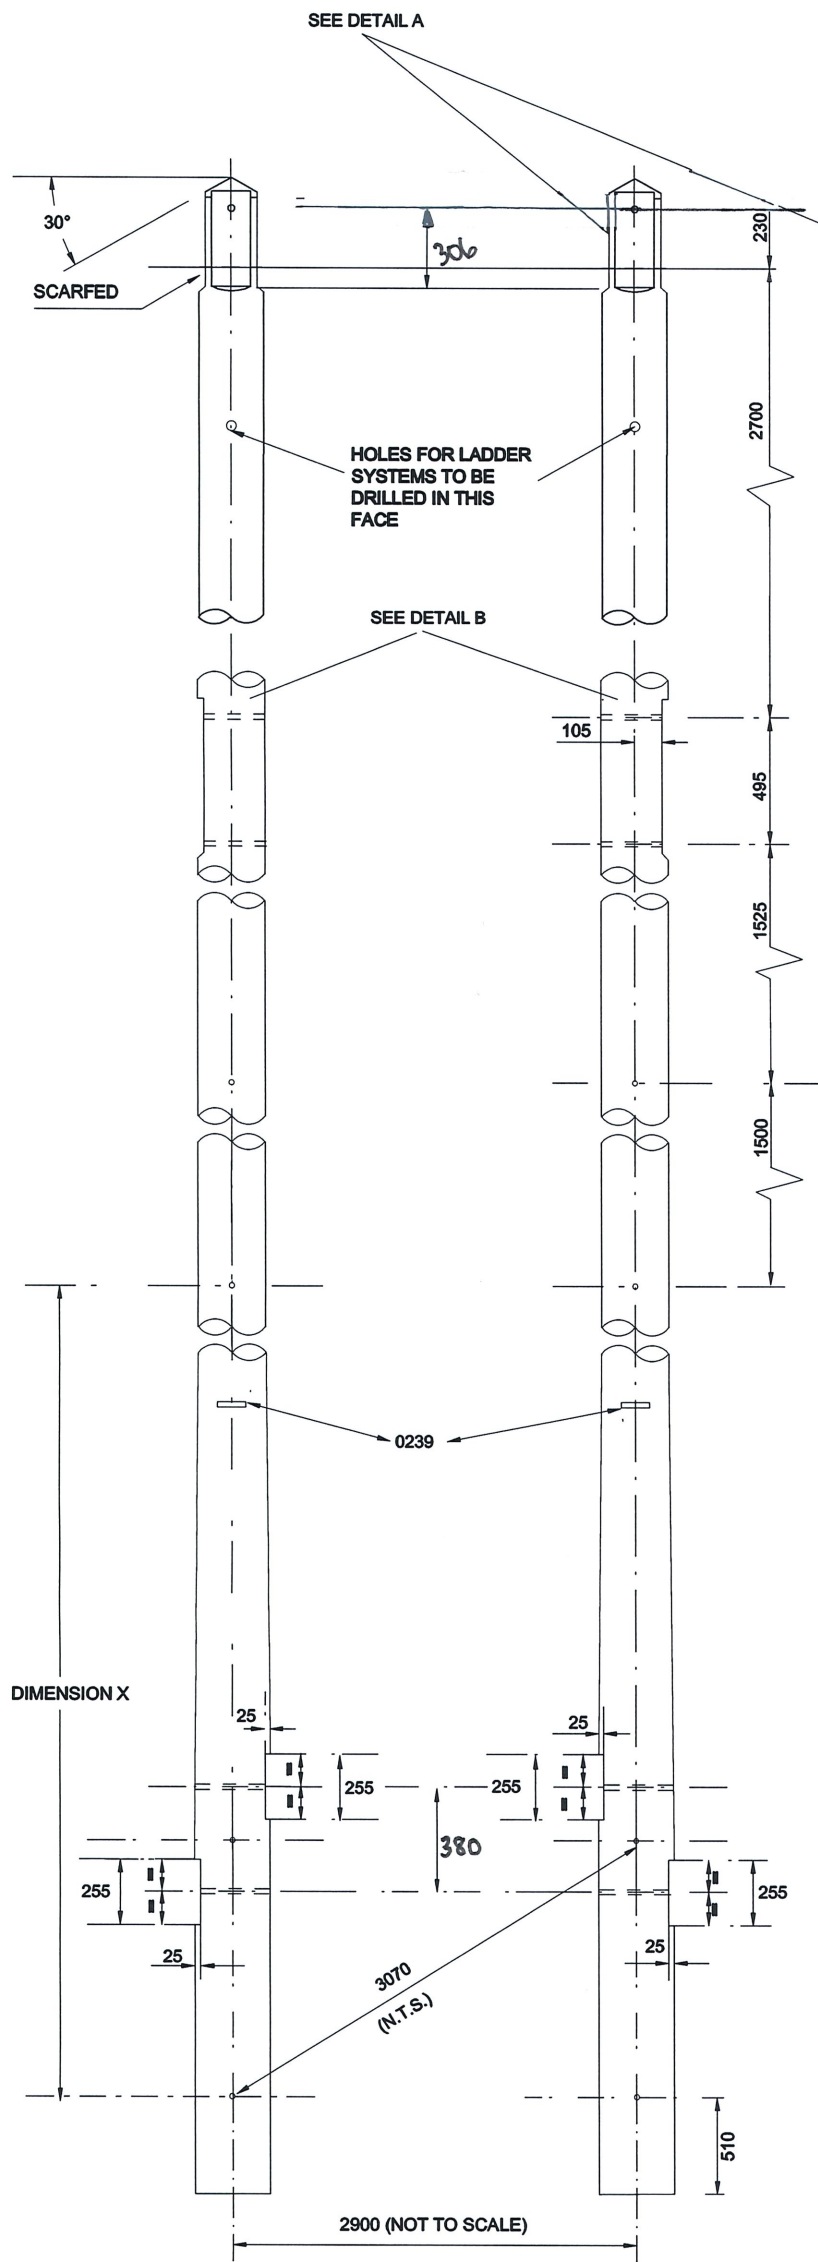


SIDE ELEVATION ON VIEW 'A' & 'B'
SCALE 1:5

SIDE ELEVATION

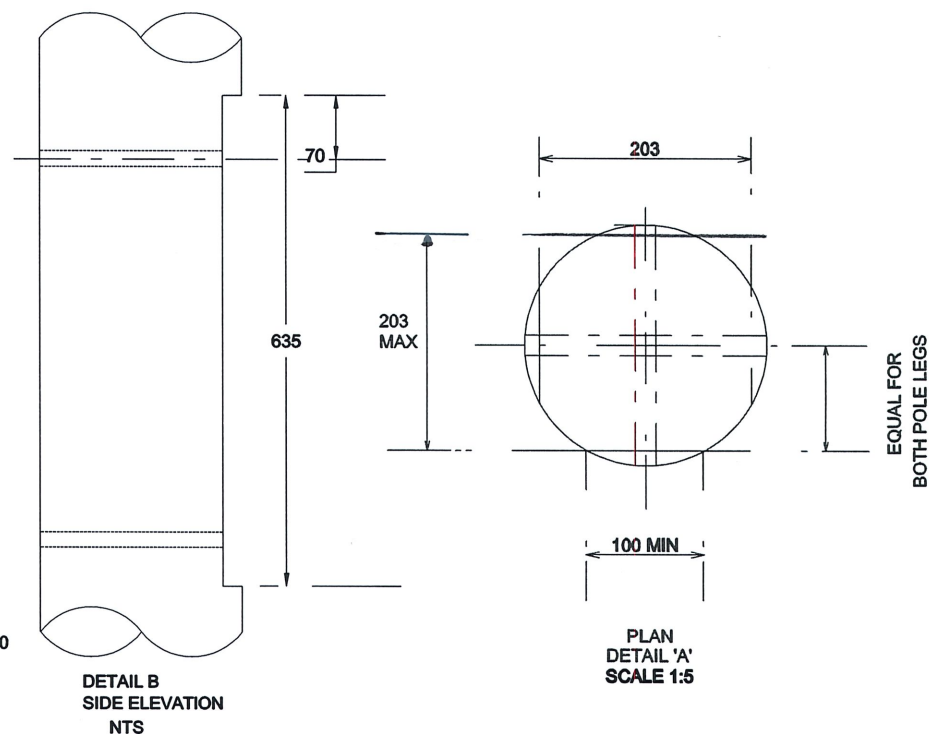

DETAIL B
PLAN

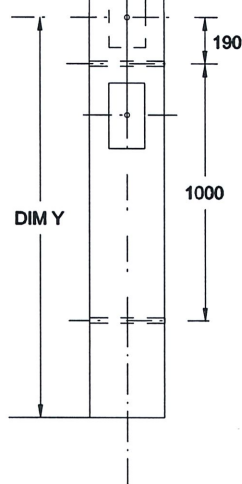

NOTES:

- POLE LEGS TO BE MATCHED. POLE TOP MINIMUM DIAMETER BEFORE FABRICATION STOUT - 230mm
- ALL HOLES TO BE 22mm DIA. DRILLED AT RIGHT ANGLES TO VERTICAL CENTRE LINE OF POLE. ALL DRILLING AND CUTTING TO BE DONE STRICTLY TO TEMPLATE PRIOR TO CREASOTING.
- POLE BUTTS TO CUT AT RIGHT ANGLES TO AXIS OF POLE.
- POLE LEGS TO BE NOTCHED AND DRILLED FOR 250 X 125 WOOD BAULKS AS SHOWN
- POLE TO BE SUPPLIED WITH 4 - 1300 X 250 X 125 BAULKS TO DRG NO 1 00 043 9130 TYPE 2 CUT FROM THE SQUARE AND 4 - M20 GALVANISED BOLTS EACH WITH 1 FLAT AND 1 CURVED GALVANISED WASHER TO DRG NOS 1 00 043 9604 AND 9605 RESPECTIVELY.
- HOLES NOT REQUIRED FOR PARTICULAR APPLICATIONS WILL BE PLUGGED ON SITE

ALL DIMENSIONS SHOWN ARE IN MILLIMETRES UNLESS OTHERWISE STATED

POLE LENGTH	DIM X	DIM Y
12.0m	4920	1700
13.0m	5920	1700
14.0m	6920	1700
15.0m	7920	1700
16.0m	8920	1900

NORTHERN POWERGRID Manufacturer Details		Lloyds Court, 78 Grey Street, Newcastle Upon Tyne, NE1 6AF	
Sheet No. 5	Scale 1:20	66KV SINGLE CIRCUIT LINES DRILLING AND SCARFING FOR TERMINAL SUPPORT WITH SURGE ARRESTERS - 1173 SHEET 4	
Prepared By Barbara Gordon	Grid Reference	Type OVERHEAD	POLES
Revised 16/06/15	Checked By S SALKELD	Ref No. C995434	Historic Drg.No. 1091231173
Date Issued 16/02/11		Revision G	Notes