
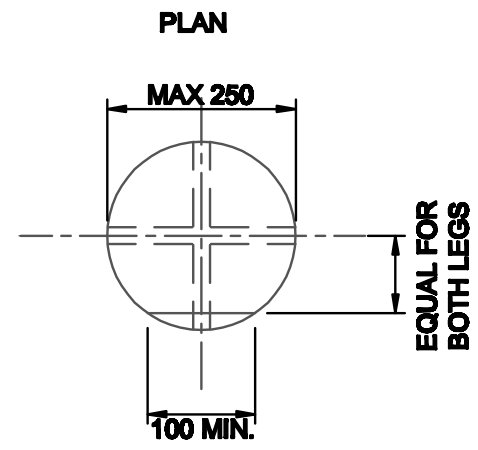
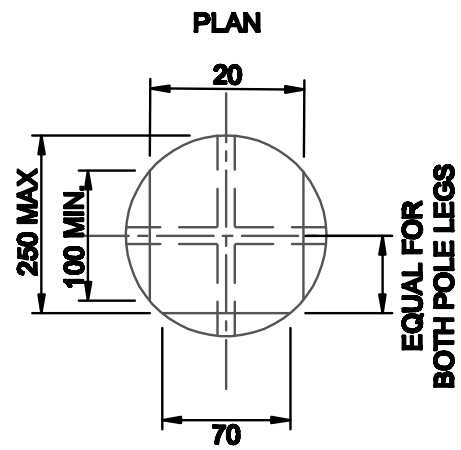
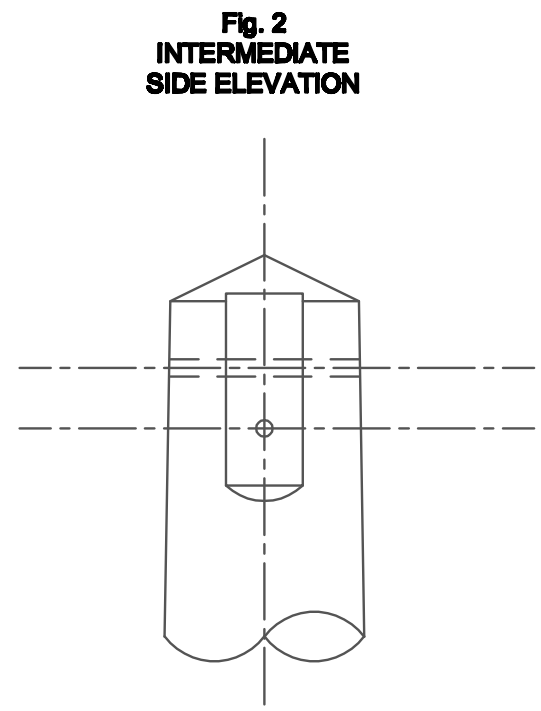
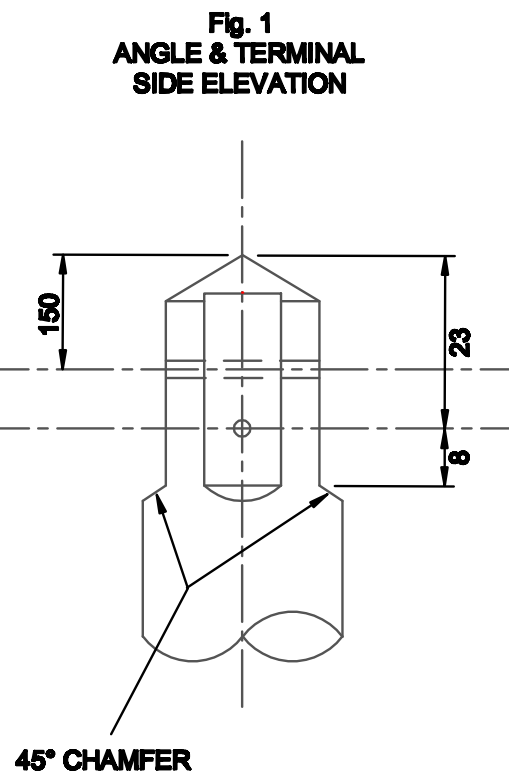


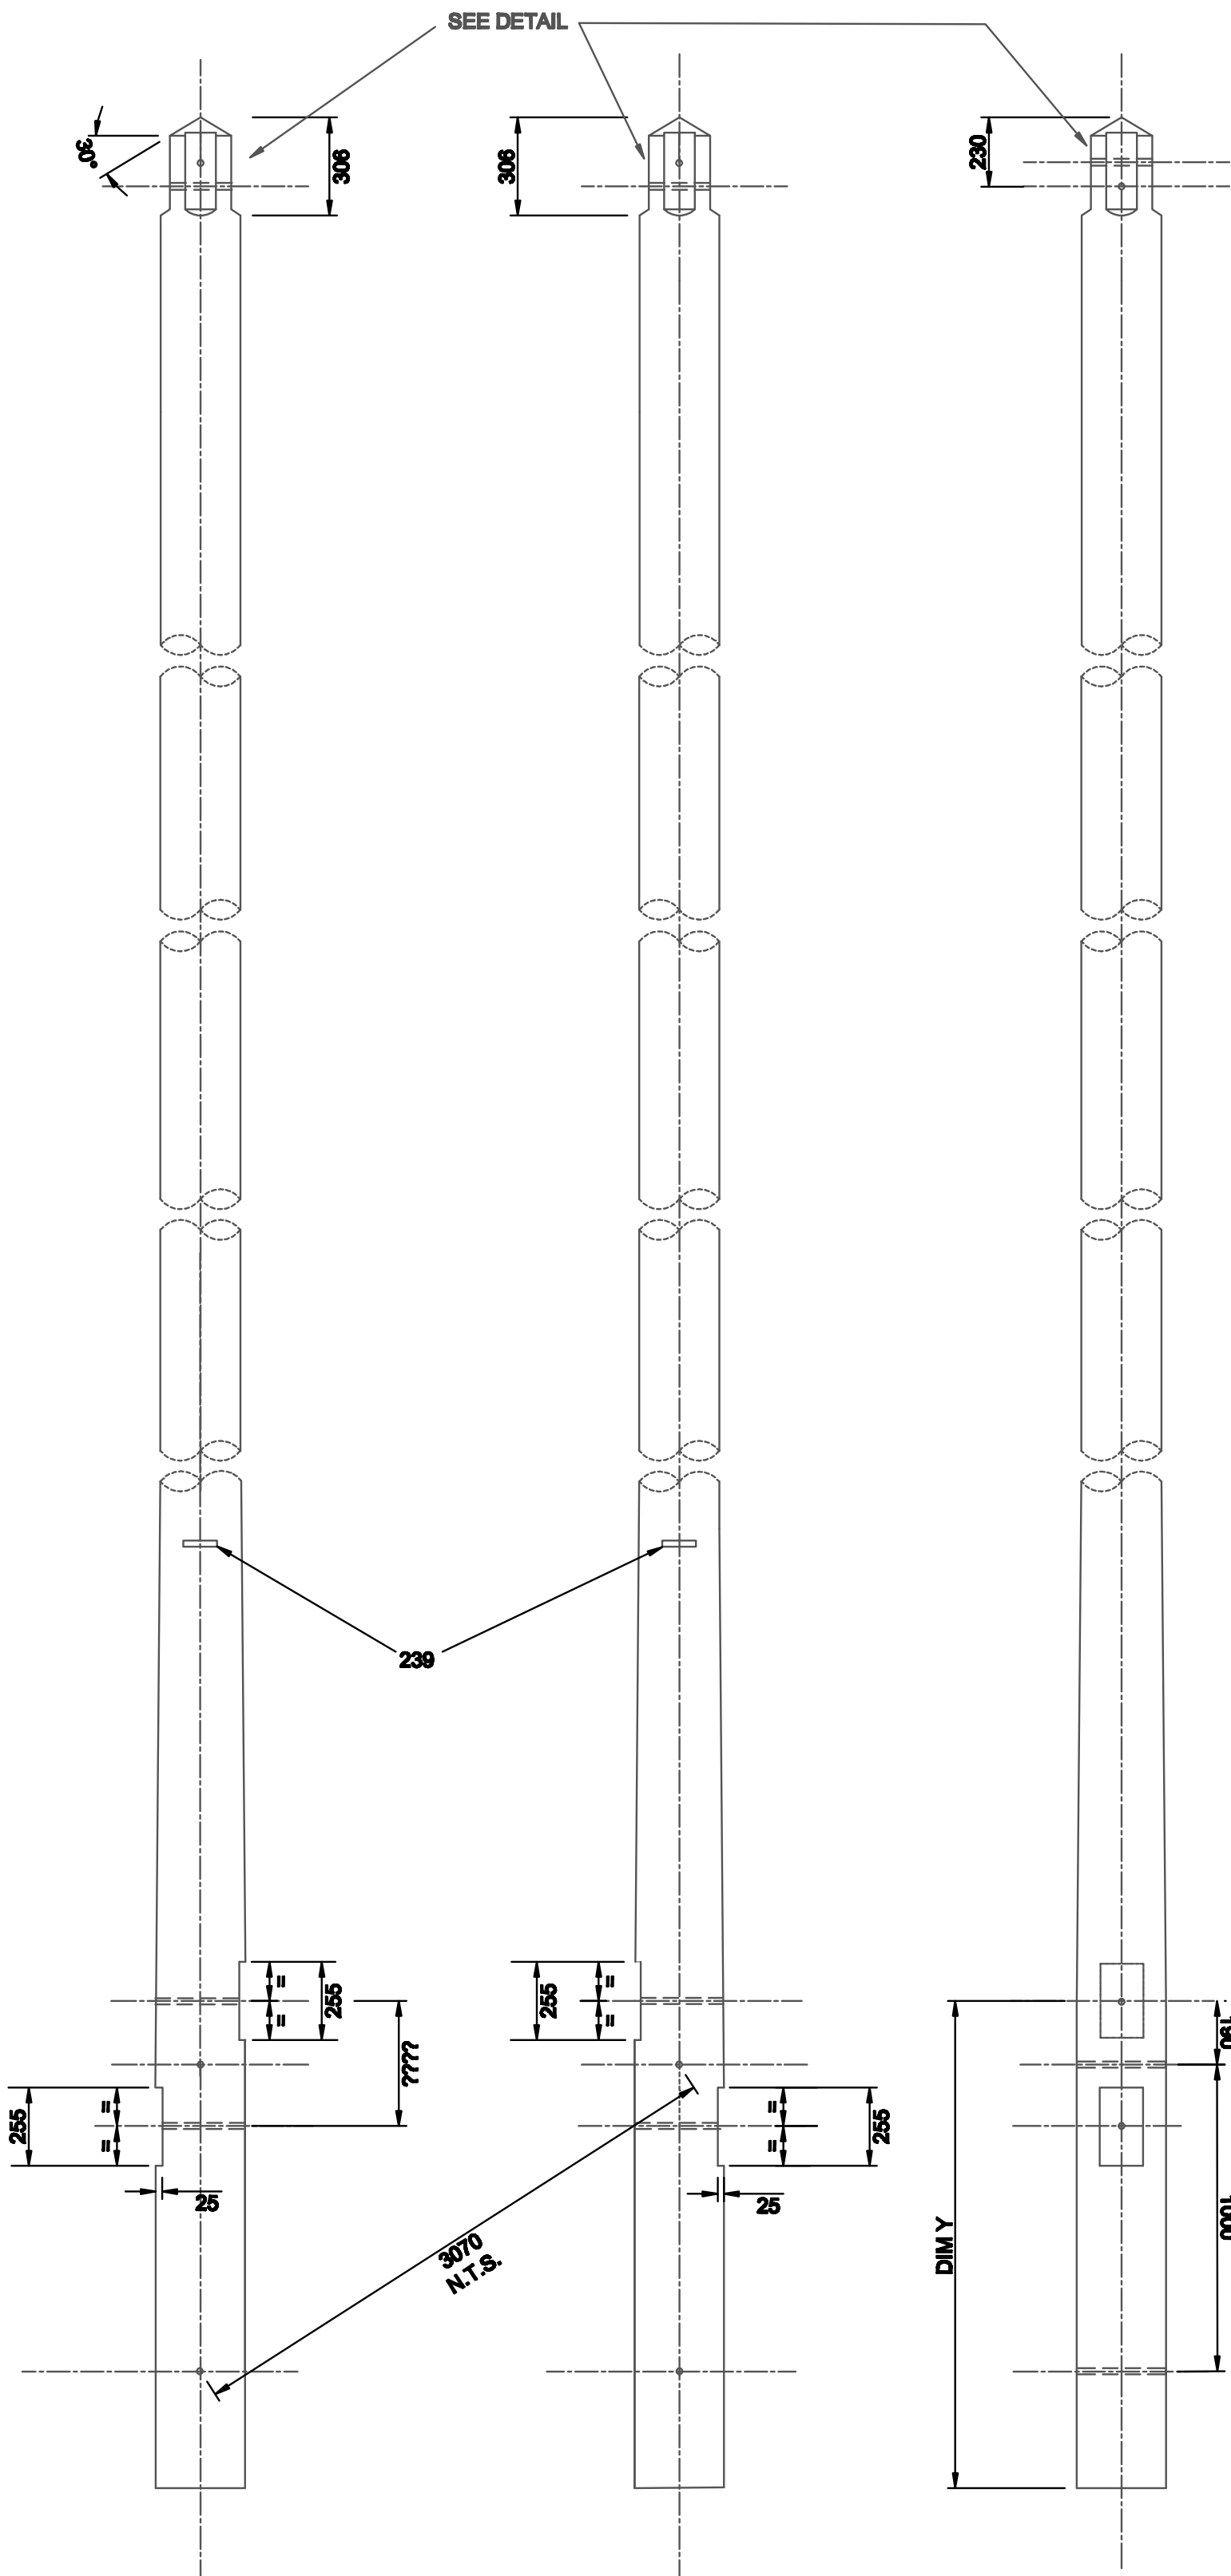

POLE TOP MIN. DIA. BEFORE
FABRICATION E/STOUT 228mm
(NORMALLY FABRICATED FROM
STD. POLE HEIGHT PLUS 2m.

POLE TOP MIN. DIA. BEFORE
FABRICATION STOUT 195mm

DETAIL
SCALE 1/10

- NOTES:
- POLE LEGS TO BE MATCHED. POLE TOP MINIMUM DIAMETER BEFORE FABRICATION TO SUIT POLE FIGS.
 - ALL HOLES TO BE 22mm DIA. DRILLED AT RIGHT ANGLES TO VERTICAL CENTRE LINE OF POLE. ALL DRILLING AND CUTTING TO BE DONE STRICTLY TO TEMPLATE PRIOR TO CREASOTING.
 - POLE BUTTS TO CUT AT RIGHT ANGLES TO AXIS OF POLE.
 - POLE LEGS TO BE NOTCHED AND DRILLED FOR 250 X 125 WOOD BAULKS AS SHOWN
 - POLE TO BE SUPPLIED WITH 4 - 1300 X 250 X 125 BAULKS TO DRG NO 1 00 043 9130 TYPE 2 CUT FROM THE SQUARE AND 4 - M20 GALVANISED BOLTS EACH WITH 1 FLAT AND 1 CURVED GALVANISED WASHER TO DRG NOS 1 00 043 9804 AND 9805 RESPECTIVELY.
 - HOLES NOT REQUIRED FOR PARTICULAR APPLICATIONS WILL BE PLUGGED ON SITE

ALL DIMENSIONS SHOWN ARE IN MILLIMETRES UNLESS OTHERWISE STATED

POLE LENGTH	DIM X	DIM Y
UP TO AND INCLUDING 12.0m	-	1500
13.0m TO 15.0m INCLUSIVE	-	1700
16.0m AND 17.0m	-	1900
18.0m	7955	1900
20.0m	9255	2500
22.0m	10255	2500
24.0m	11255	2500



Manufacturer Details	
Sheet No. 1	Scale 1:20
Prepared By Joan.Oakley	
Revised 18/06/13	Grid Reference
Date Issued 16/02/11	Checked By S SALKELD

Lloyds Court, 78 Grey Street, Newcastle Upon Tyne, NE1 6AF			
66KV SINGLE CIRCUIT OVERHEAD LINES DRILLING, SCARFING AND MARKING FOR STANDARD PORTAL TYPE POLE TO SPECIFICATION OHL 4/84			
Type OVERHEAD		POLES	
Ref No.	C995423	Historic Drg.No.	1091231187
Revision	L	Notes	