


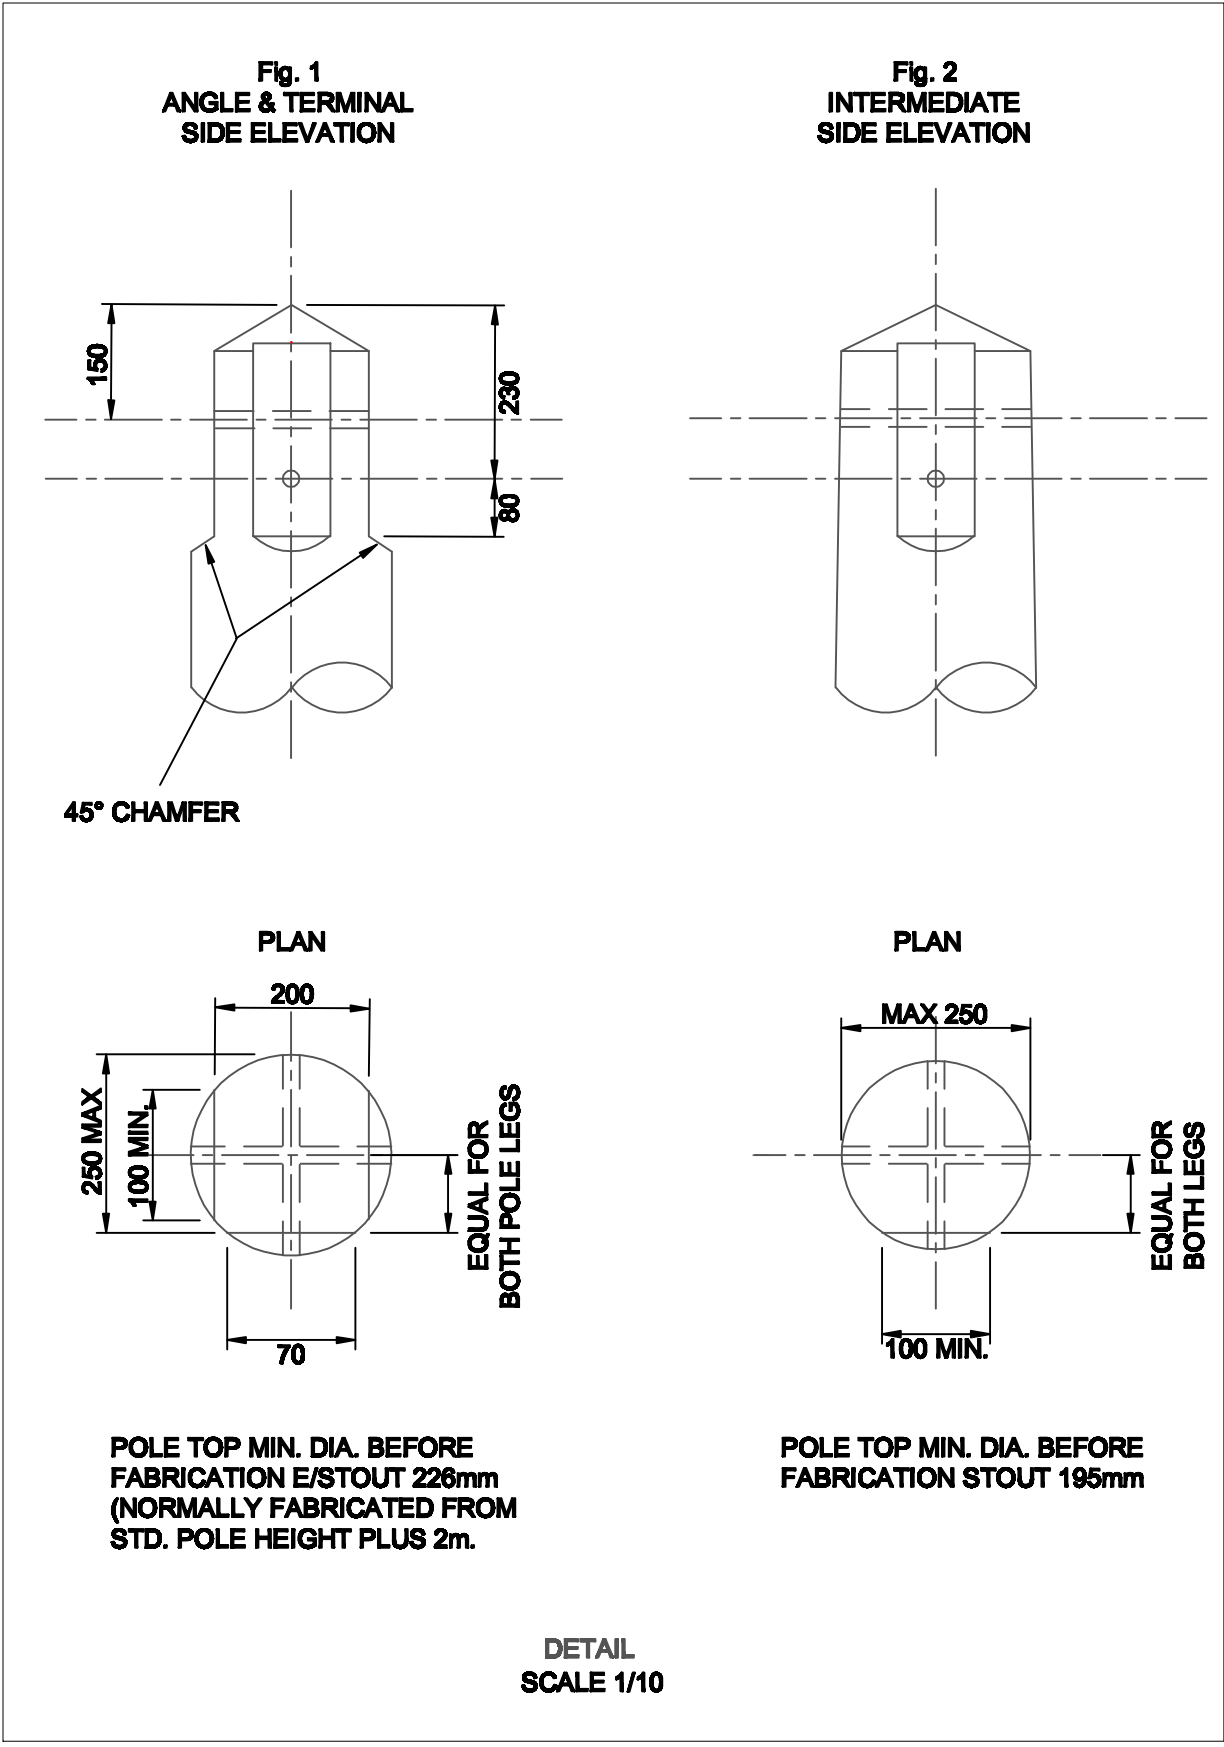

- | POLE LENGTH | DIM X | DIM Y |
|---------------------------|-------|-------|
| UP TO AND INCLUDING 12.0m | - | 1500 |
| 13.0m TO 15.0m INCLUSIVE | - | 1700 |
| 16.0m AND 17.0m | - | 1900 |
| 18.0m | 7955 | 1900 |
| 20.0m | 9255 | 2500 |
| 22.0m | 10255 | 2500 |
| 24.0m | 11255 | 2500 |

Lloyds Court, 78 Grey Street, Newcastle Upon Tyne, NE1 6AR			
66KV SINGLE CIRCUIT OVERHEAD LINES DRILLING, SCARFING AND MARKING FOR STANDARD PORTAL TYPE POLE TO SPECIFICATION OHL 4/84			
Type OVERHEAD		POLES	
Ref No.	C995423	Historic Drg.No.	1091231187
Revision M		Notes	