


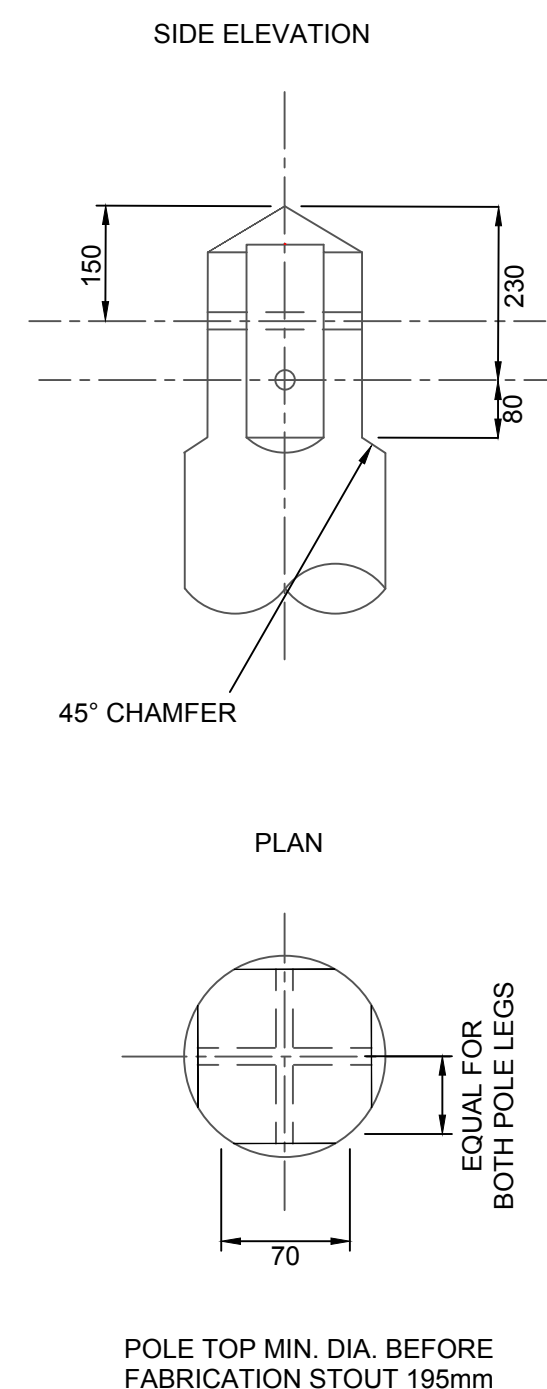

POLE TOP MIN. DIA. BEFORE
FABRICATION STOUT 195mm

DETAIL
SCALE 1/10

POLE LENGTH	DIM Y
UP TO AND INCLUDING 12.0m	1500
13.0m TO 15.0m INCLUSIVE	1700
16.0m AND 17.0m	1900
18.0m	1900
20.0m	2500
22.0m	2500
24.0m	2500

NOTES:

1. ALL HOLES TO BE 22mm DIA. DRILLED AT RIGHT ANGLES TO VERTICAL CENTRE LINE OF POLE. ALL DRILLING AND CUTTING TO BE DONE STRICTLY TO TEMPLATE PRIOR TO CREASOTING.
2. POLE BUTTS TO CUT AT RIGHT ANGLES TO AXIS OF POLE.
3. POLE LEGS TO BE NOTCHED AND DRILLED FOR 250 X 125 WOOD BAULKS AS SHOWN
4. HOLES NOT REQUIRED FOR PARTICULAR APPLICATIONS WILL BE PLUGGED ON SITE

ALL DIMENSIONS SHOWN ARE IN MILLIMETRES UNLESS OTHERWISE STATED

 NORTHERN POWERGRID		Lloyds Court, 78 Grey Street, Newcastle Upon Tyne, NE1 6AF	
		66KV SINGLE CIRCUIT OVERHEAD LINES DRILLING, SCARFING AND MARKING FOR STANDARD PORTAL TYPE POLE TO SPECIFICATION OHL 4/84	
Manufacturer Details			
Sheet No. 1	Scale 1:20		
Prepared By Barbara.Rimmer		Type OVERHEAD	POLES
Revised 04/06/20	Grid Reference	Ref No. C995423	Historic Drg.No. 1091231187
Date Issued 16/02/11	Checked By S SALKELD	Revision 0	Notes