

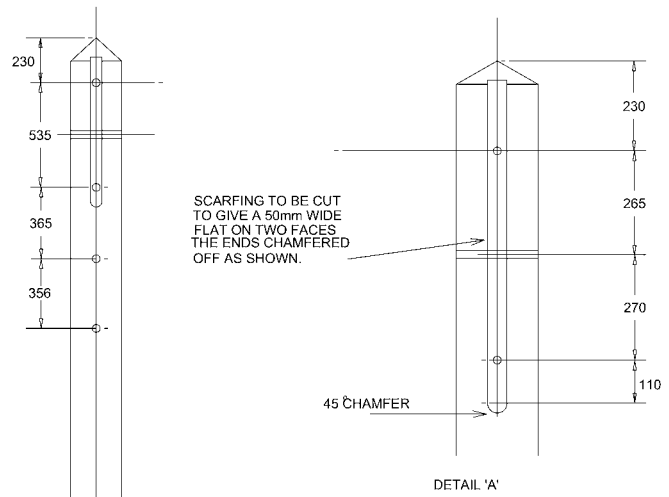


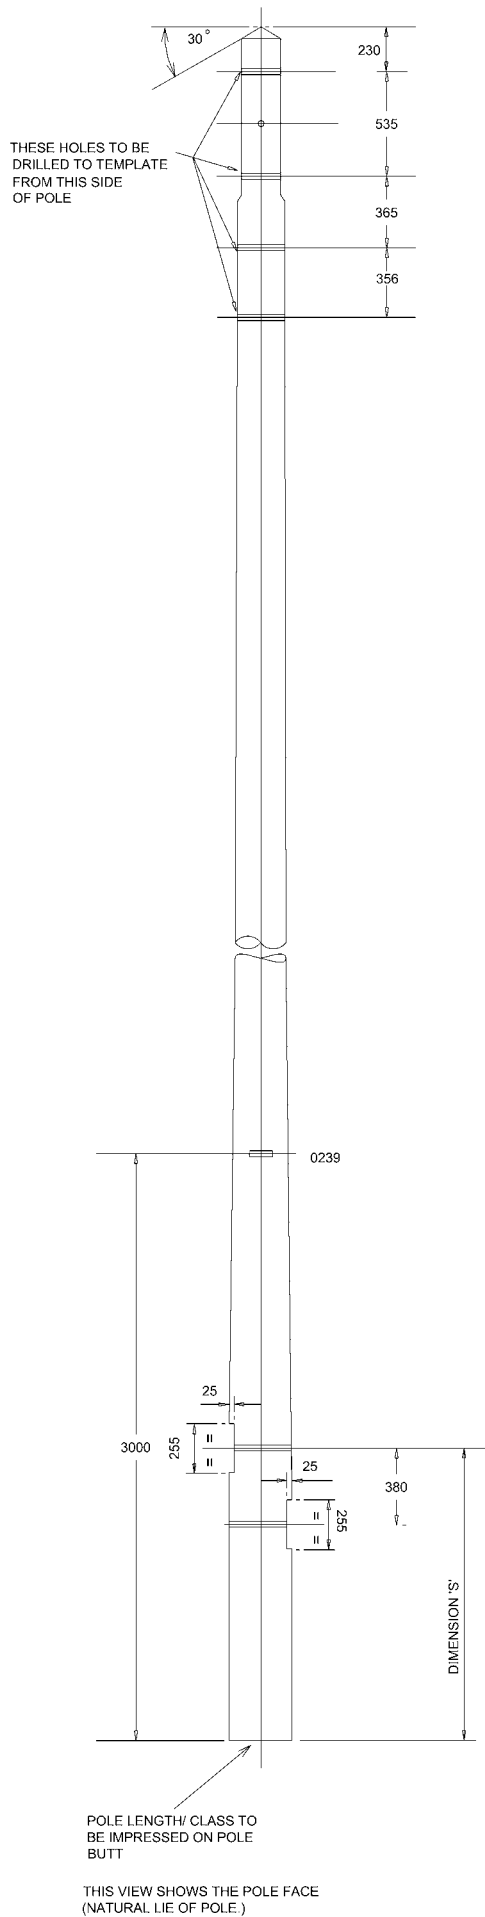

NOTES

1. CLASS OF POLE TO BE 'STOUT' OR EXTRA STOUT IN ACCORDANCE WITH 1.09.101.0238
2. POLE BUTT TO BE CUT AT RIGHT ANGLES TO AXIS OF POLE
3. ALL HOLES TO BE 22mm DIA. DRILLED AT RIGHT ANGLES TO VERTICAL CENTRE LINE OF POLE. ALL DRILLING AND CUTTING TO BE DONE STRICTLY TO TEMPLATE PRIOR TO CREOSOTING
4. POLE TO BE NOTCHED AND DRILLED FOR
1 x 250 x 125 x 2500 AND
1 x 250 x 125 x 1300 LONG BAULKS
5. EXTRA STOUT POLES TO BE NORMALLY FITTED WITH DOUBLE BAULKS. EXTRA STOUT POLES DESIGNED TO INCREASE WIND SPANS MAY BE UNSUITABLE FOR POOR GROUND CONDITIONS. SEE SPECIFICATION.

POLE LENGTH	DIM. 'S'
8.5m - 12m INCLUSIVE	1.5
13.0m - 15.0m INCLUSIVE	1.7
16.0m - 18.0m INCLUSIVE	1.9
20.0m - 24m INCLUSIVE	2.5

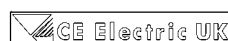

Manufacturer Details

Sheet No.

Scale

Prepared By

1:20

Revised

Grid Reference

Date Issued

Checked By

Lloyds Court, 78 Grey Street, Newcastle Upon Tyne, NE1 6AF

132KV SINGLE CIRCUIT OVERHEAD LINES
DRILLING, SCARFING
AND MARKING FOR SINGLE
INTERMEDIATE POLE ARRANGEMENT

Type

OVERHEAD

POLES

Ref No.

C102523

Historic
Drg. No.

1091380006

Revision A

Notes

ALL DIMENSIONS SHOWN ARE IN MILLIMETRES UNLESS OTHERWISE STATED