
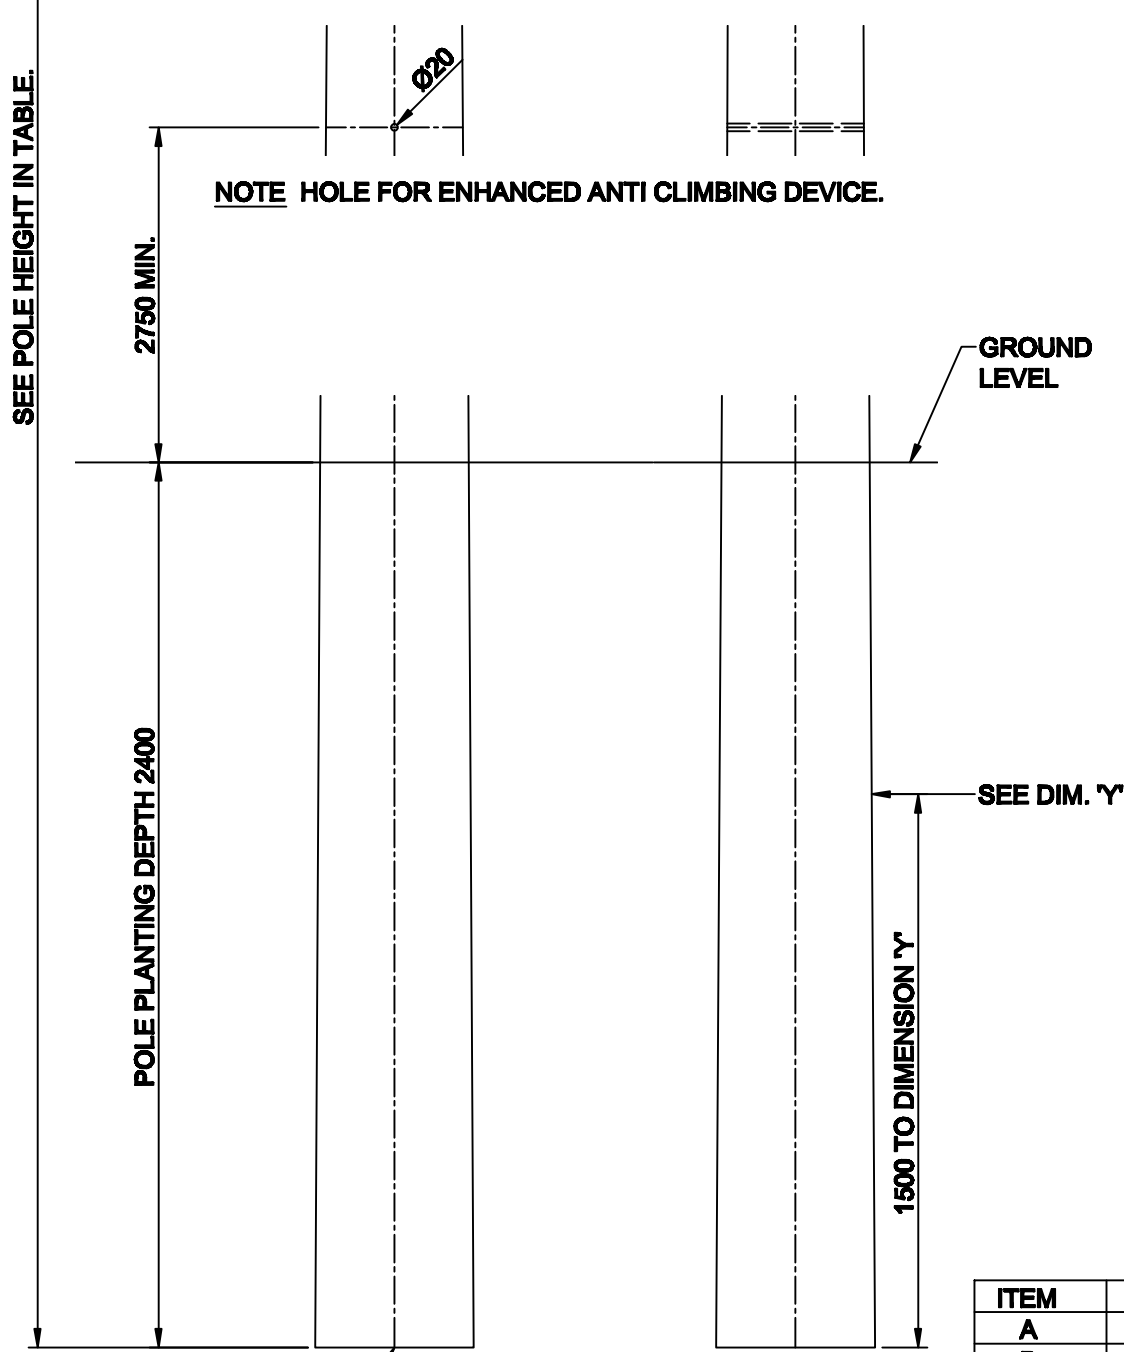


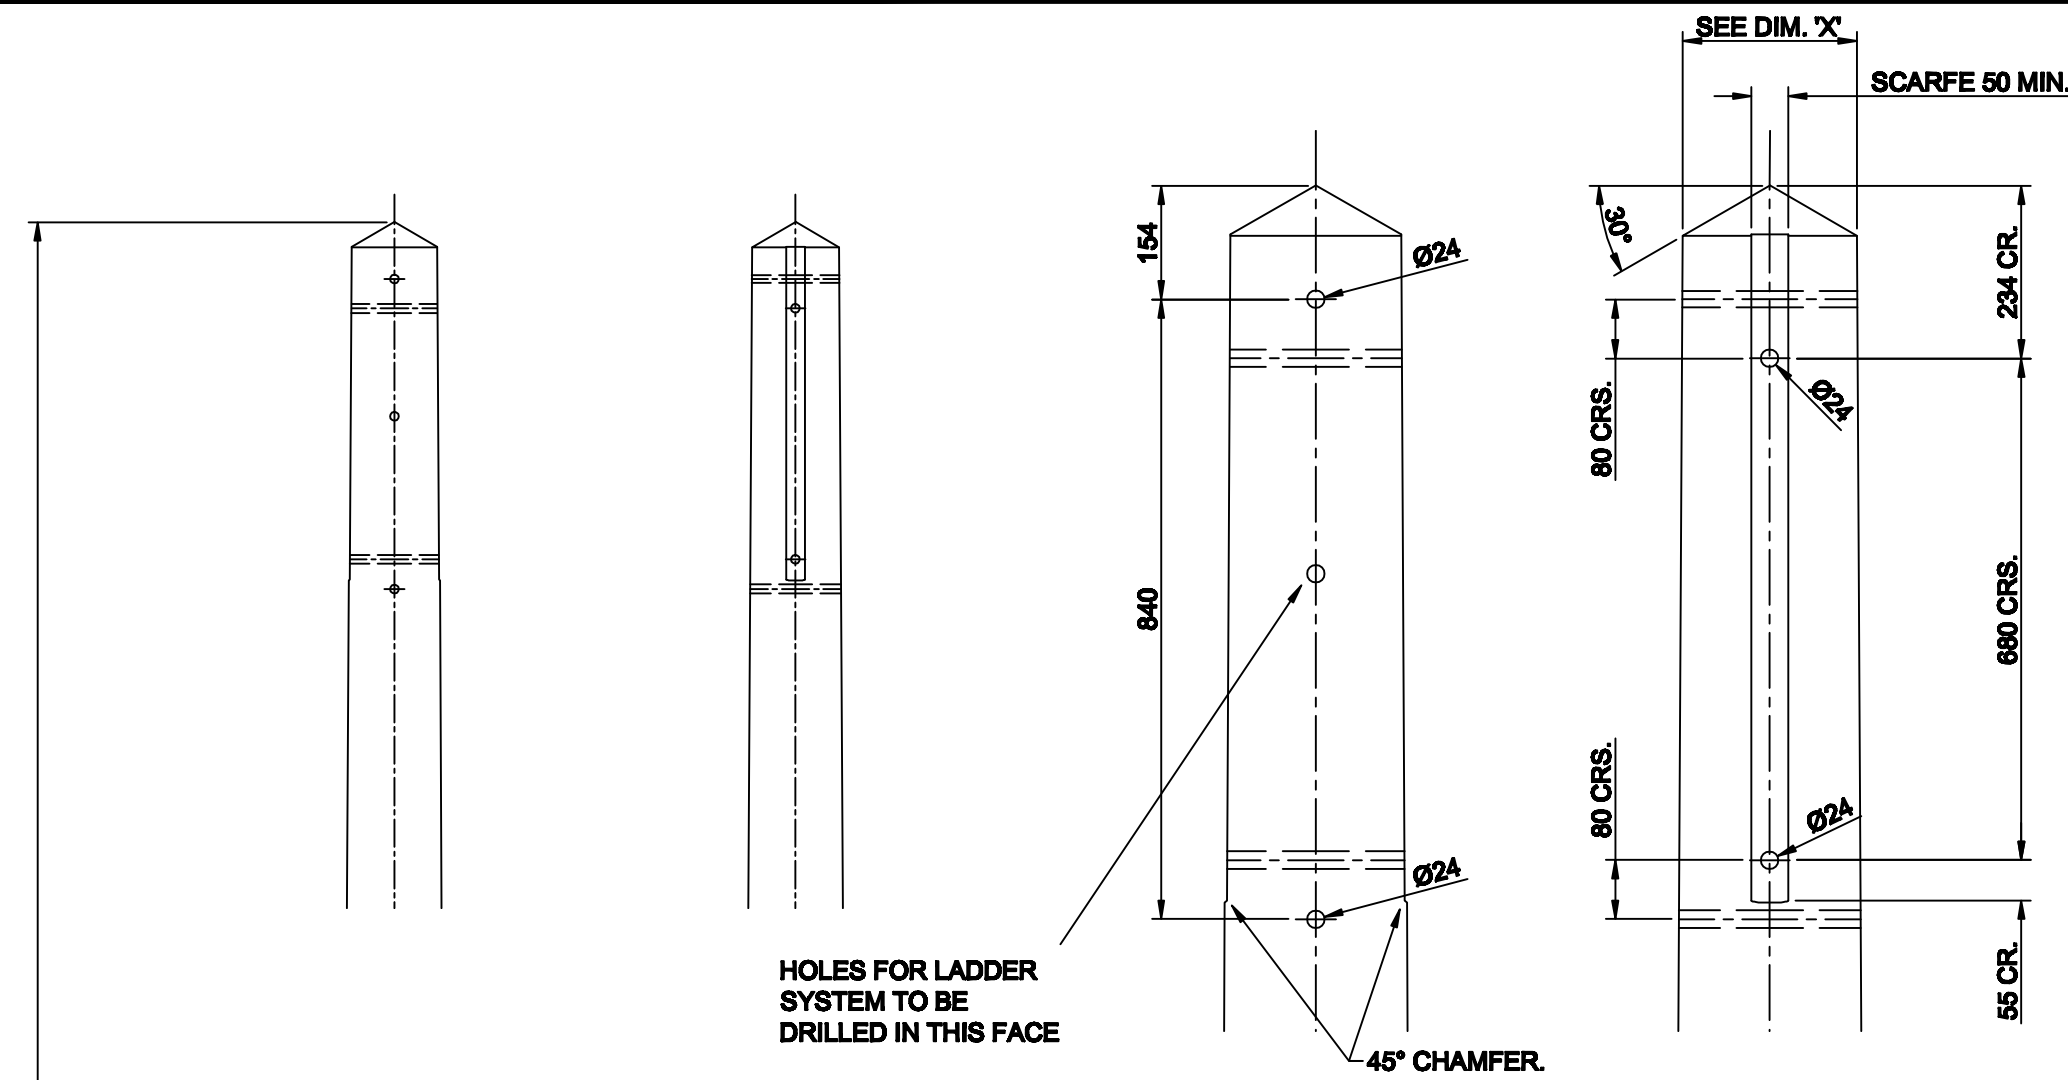

ENLARGED VIEWS OF POLE APEX SCALE 1:10

IMPORTANT NOTE

THE SCARFE IS PARALLEL TO THE POLE EDGE & NOT THE POLE CENTRELINE.

SCARFING TO BE CUT TO GIVE A 50mm WIDE FLAT ON TWO DIAMETRICALLY OPPOSITE FACES WITH ENDS CHAMFERED AS SHOWN.

NOTES

1. CLASS OF POLE TO BE EXTRA STOUT IN ACCORDANCE WITH 1.09.101.0238
2. POLE BUTT TO BE CUT AT RIGHT ANGLES TO AXIS OF POLE.
3. ALL HOLES EXCEPT WHERE STATED OTHERWISE TO BE 24mm DIA. DRILLED AT RIGHT ANGLES TO VERTICAL CENTRELINE OF POLE. ALL DRILLING & CUTTING TO BE DONE STRICTLY TO TEMPLATE PRIOR TO CREOSOTING.
4. BS 1990 TABULATED MIN VALUES HAVE BEEN AMENDED TO REFLECT CALCULATED MEAN VALUES

ITEM	POLE HEIGHT	DIMENSION 'X' (Min/ Max)	DIMENSION 'Y' (Min/ Max)
A	12000 mm	Ø242 mm - Ø260 mm	Ø333 mm - Ø370 mm
B	13000 mm	Ø247 mm - Ø265 mm	Ø371 mm - Ø390 mm
C	14000 mm	Ø247 mm - Ø265 mm	Ø384 mm - Ø400 mm
D	15000 mm	Ø247 mm - Ø265 mm	Ø394 mm - Ø420 mm
E	16000 mm	Ø253 mm - Ø270 mm	Ø418 mm - Ø435 mm
F	17000 mm	Ø253 mm - Ø270 mm	Ø431 mm - Ø450 mm

POLE LENGTH/ CLASS TO BE IMPRESSED ON POLE BUTT.

THIS VIEW SHOWS THE POLE FACE (NATURAL LIE OF POLE).

		Lloyds Court, 78 Grey Street, Newcastle Upon Tyne, NE1 6AF	
Manufacturer Details		132KV OVERHEAD LINES DRILLING, SCARFING AND MARKINGS FOR SINGLE ANGLE POLE ARRANGEMENT	
Sheet No. 2	Scale AS SHOWN	Type OVERHEAD	DOCUMENT_SUB_CLASS
Prepared By Janis.Webb	Grid Reference	Ref No. C949737	Historic Drg.No. 1091390003
Revised 14/08/07	Checked By G HAMMEL	Revision D	Notes
Date Issued 02/07/07			