
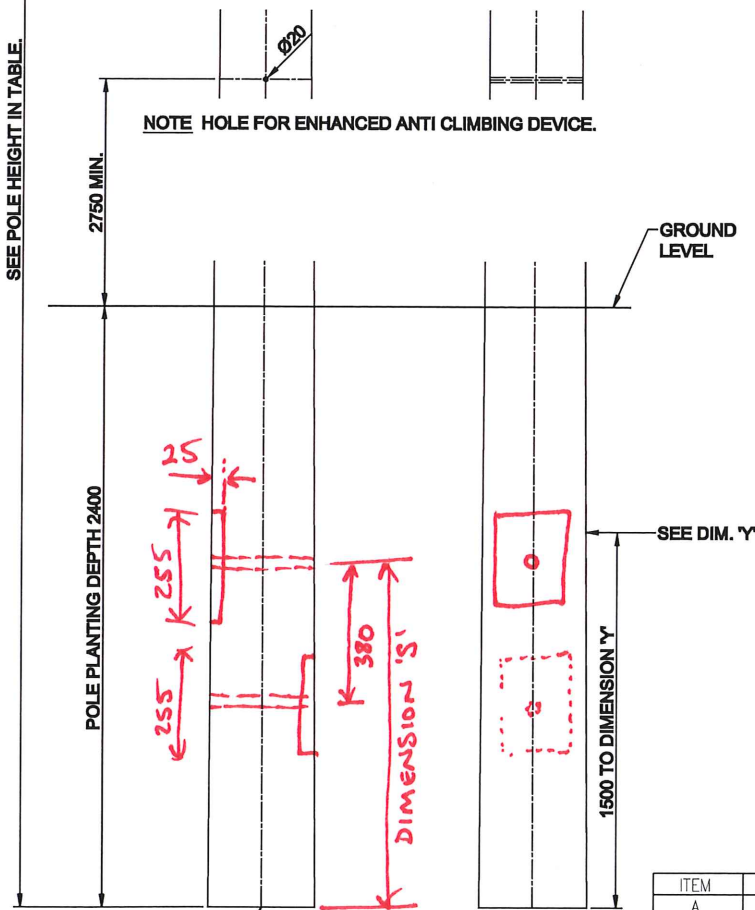


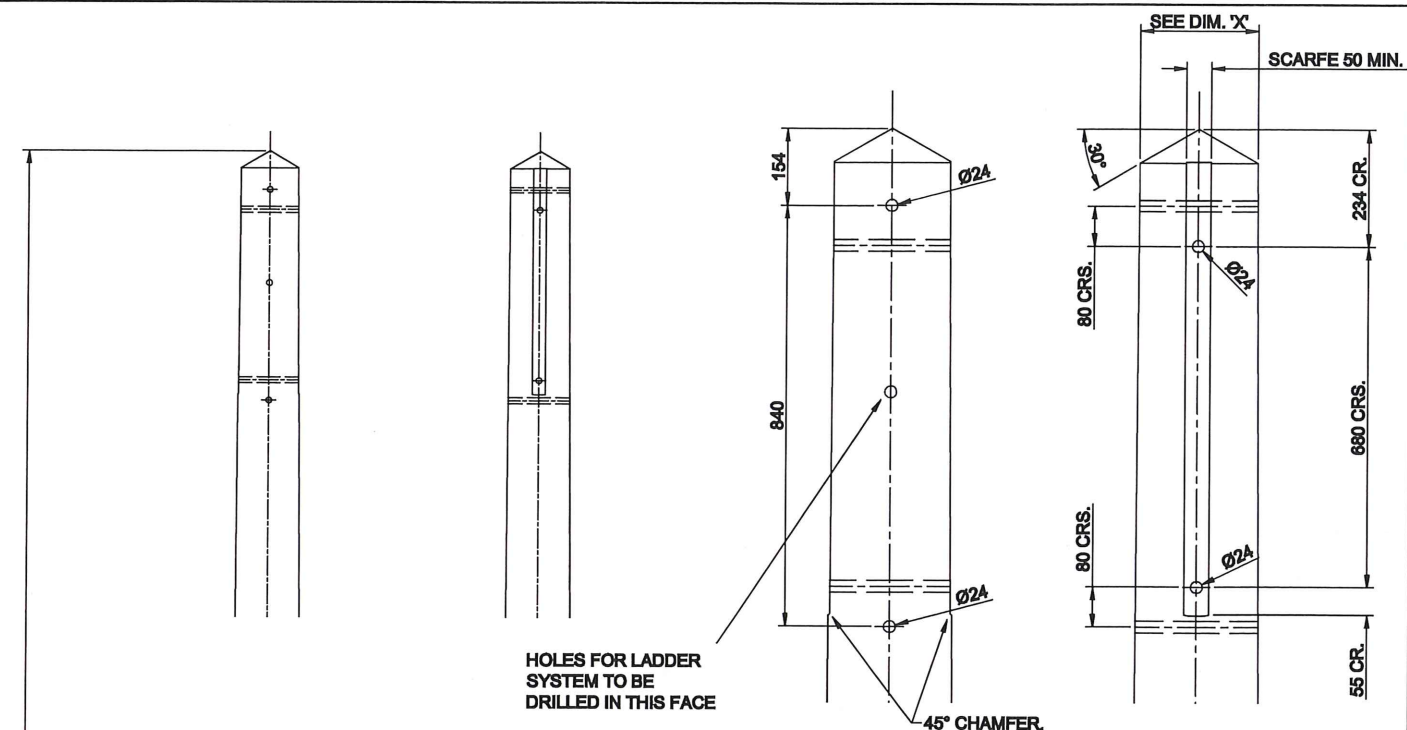

ENLARGED VIEWS OF POLE APEX SCALE 1:10

IMPORTANT NOTE

THE SCARFE IS PARALLEL TO THE POLE EDGE & NOT THE POLE CENTRELINE.

SCARFING TO BE CUT TO GIVE A 50mm WIDE FLAT ON TWO DIAMETRICALLY OPPOSITE FACES WITH ENDS CHAMFERED AS SHOWN.

NOTES

1. CLASS OF POLE TO BE EXTRA STOUT IN ACCORDANCE WITH 1.09.101.0238
2. POLE BUTT TO BE CUT AT RIGHT ANGLES TO AXIS OF POLE.
3. ALL HOLES EXCEPT WHERE STATED OTHERWISE TO BE 24mm DIA. DRILLED AT RIGHT ANGLES TO VERTICAL CENTRELINE OF POLE. ALL DRILLING & CUTTING TO BE DONE STRICTLY TO TEMPLATE PRIOR TO CREOSOTING.
4. BS 1990 TABULATED MIN VALUES HAVE BEEN AMENDED TO REFLECT CALCULATED MEAN VALUES

POLE LENGTH	DIM. 'S'
13.0 - 15.0M INC.	2.1
16.0 - 18.0M INC.	2.1
20.0 - 24.0M INC.	2.5

ITEM	POLE HEIGHT	DIMENSION 'X' (MIN/MAX)	DIMENSION 'Y' (MIN/MAX)
A	12000mm	245	335
B	13000mm	245	350
C	14000mm	245	365
D	15000mm	245	375
E	16000mm	250	390
F	17000mm	250	415

SCALE:- 1:20

POLE LENGTH/ CLASS TO BE IMPRESSED ON POLE BUTT.

THIS VIEW SHOWS THE POLE FACE (NATURAL LIE OF POLE).

NORTHERN POWERGRID

Manufacturer Details

Sheet No. 2

Scale AS SHOWN

Prepared By Joan Oakley

Revised 19/11/13

Date Issued 02/07/07

Grid Reference

Checked By G HAMMEL

Lloyds Court, 78 Grey Street, Newcastle Upon Tyne, NE1 6AF

132KV OVERHEAD LINES
DRILLING, SCARFING AND MARKINGS
FOR SINGLE ANGLE POLE ARRANGEMENT

Type OVERHEAD

Ref No. C949737

Revision F

Notes

DOCUMENT SUB CLASS

Historic Drg.No. 1091390003 MOD