



SEE POLE HEIGHT IN TABLE.

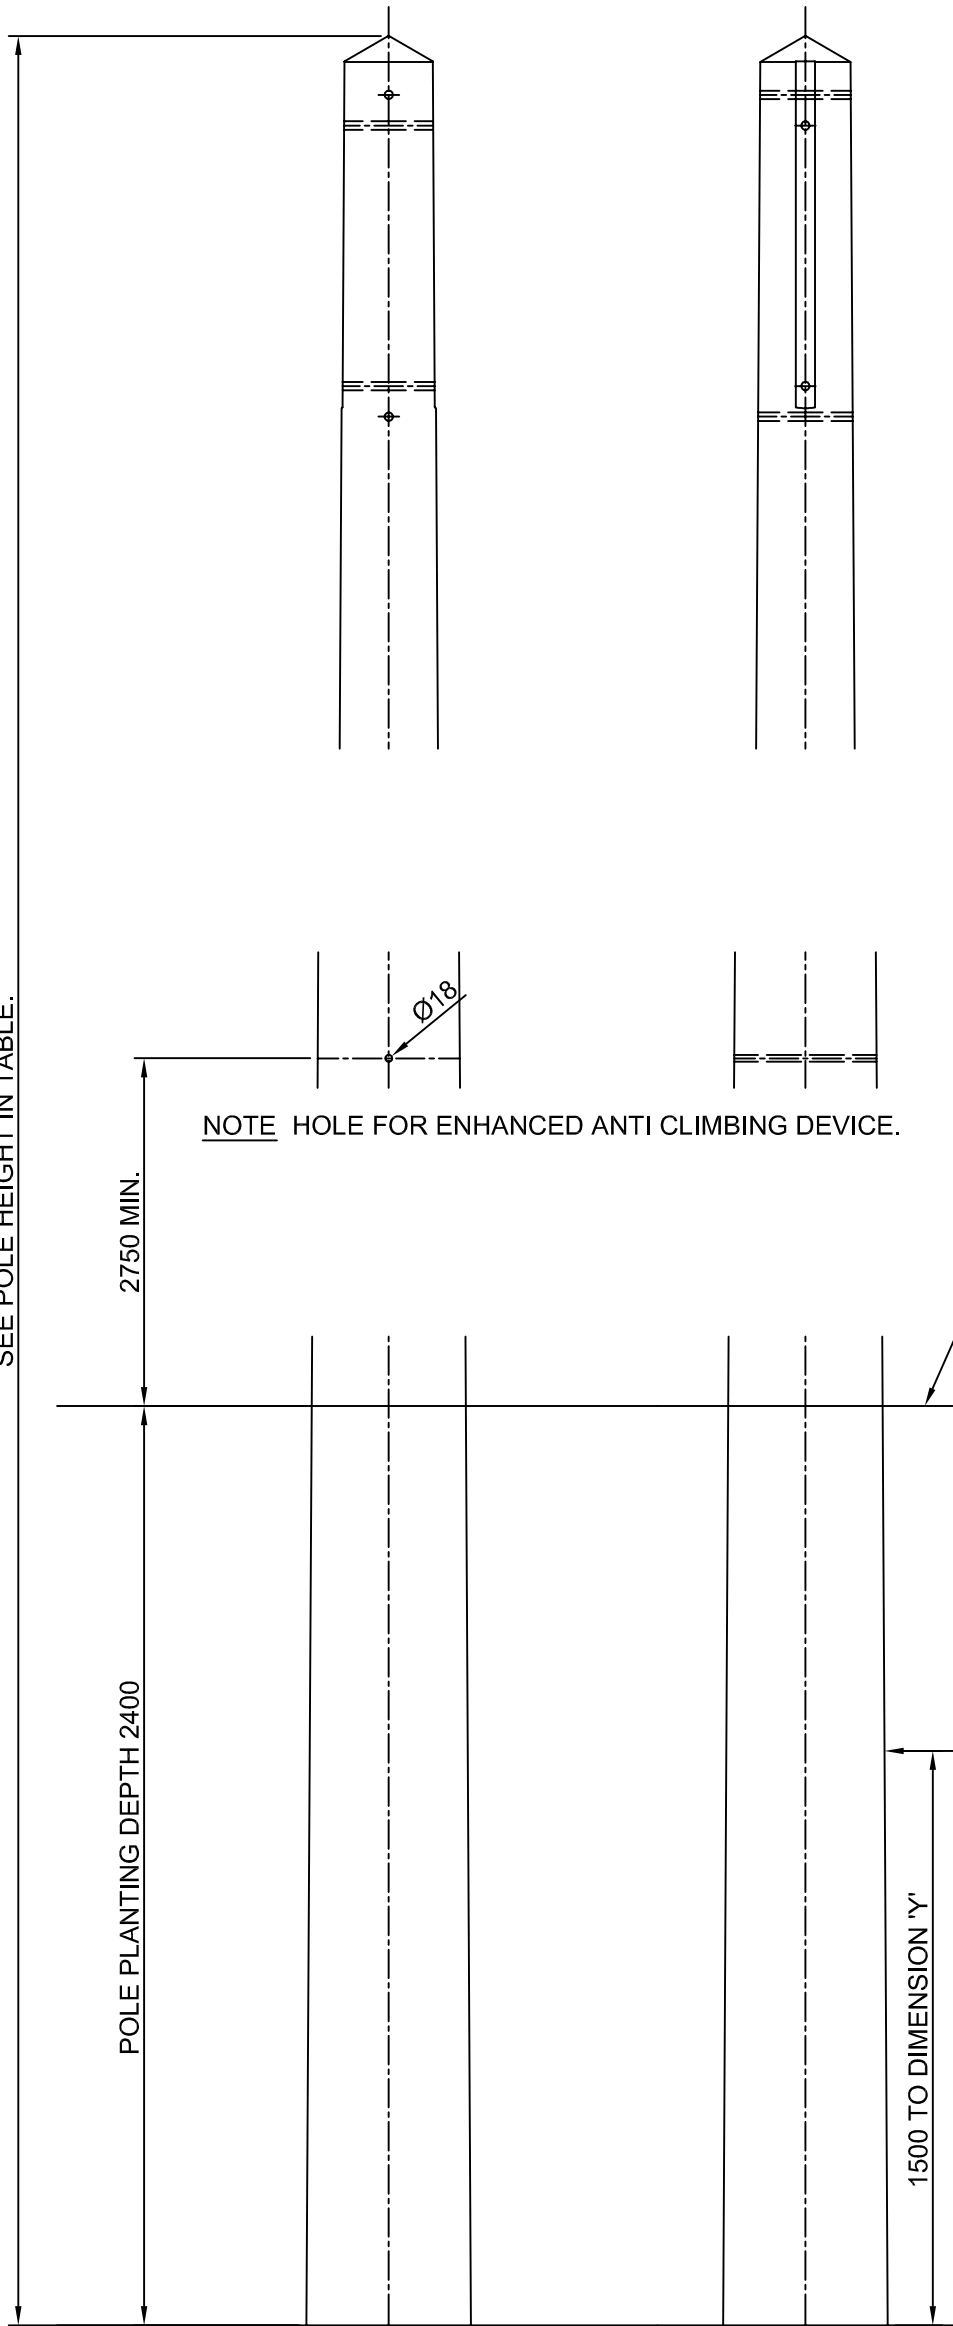

SCALE:- 1:20

POLE LENGTH/ CLASS TO BE IMPRESSED ON POLE BUTT.

THIS VIEW SHOWS THE POLE FACE (NATURAL LIE OF POLE).

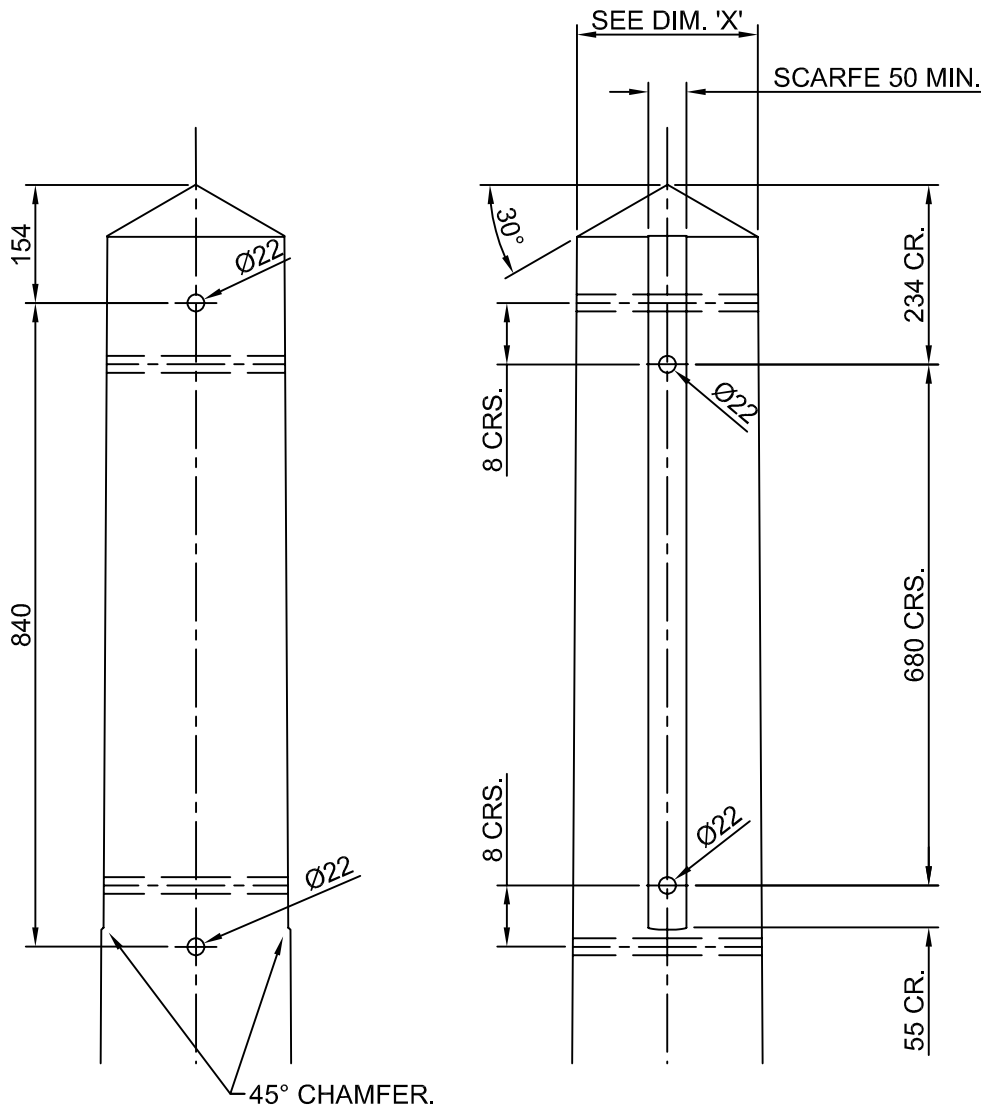

ENLARGED VIEWS OF POLE APEX SCALE 1:10

IMPORTANT NOTE

THE SCARFE IS PARALLEL TO THE POLE EDGE & NOT THE POLE CENTRELINE.

SCARFING TO BE CUT TO GIVE A 50mm WIDE FLAT ON TWO DIAMETRICALLY OPPOSITE FACES WITH ENDS CHAMFERED AS SHOWN.

NOTES

1. CLASS OF POLE TO BE EXTRA STOUT IN ACCORDANCE WITH 1.09.101.0238
2. POLE BUTT TO BE CUT AT RIGHT ANGLES TO AXIS OF POLE.
3. ALL HOLES EXCEPT WHERE STATED OTHERWISE TO BE 22mm DIA. DRILLED AT RIGHT ANGLES TO VERTICAL CENTRELINE OF POLE. ALL DRILLING & CUTTING TO BE DONE STRICTLY TO TEMPLATE PRIOR TO CREOSOTING.

ITEM	POLE HEIGHT	DIMENSION 'X' (Min/ Max)	DIMENSION 'Y' (Min/ Max)
A	12000 mm	Ø224 mm - Ø260 mm	Ø337 mm - Ø370 mm
B	13000 mm	Ø230 mm - Ø265 mm	Ø353 mm - Ø390 mm
C	14000 mm	Ø230 mm - Ø265 mm	Ø368 mm - Ø400 mm
D	15000 mm	Ø230 mm - Ø265 mm	Ø386 mm - Ø420 mm
E	16000 mm	Ø236 mm - Ø270 mm	Ø402 mm - Ø435 mm
F	17000 mm	Ø236 mm - Ø270 mm	Ø412 mm - Ø450 mm



CE Electric UK

Manufacturer Details

Sheet No.
2

Scale
1:20 & 1:10

Prepared By
TREVOR R. WILKIN

Revised

Grid Reference

Date Issued
17/02/06

Checked By

Lloyds Court, 78 Grey Street, Newcastle Upon Tyne, NE1 6AF

**132kV OVERHEAD LINES
DRILLING, SCARFING & MARKINGS
FOR SINGLE ANGLE POLE ARRANGEMENT**

Type
OVERHEAD

DOCUMENT_SUB_CLASS

Ref No. 62470A

Historic
Drg.No.

1 09 139 0003

Revision Notes