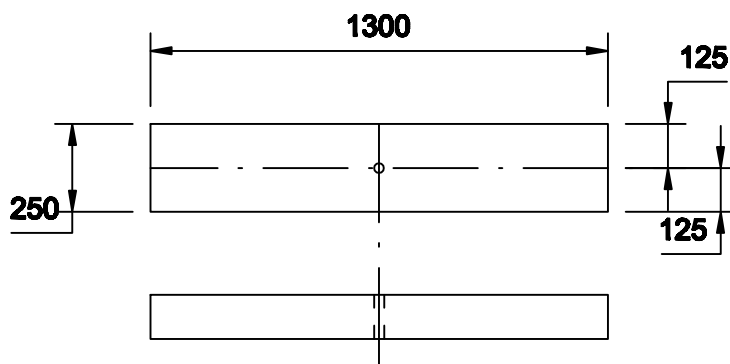
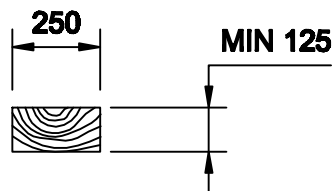
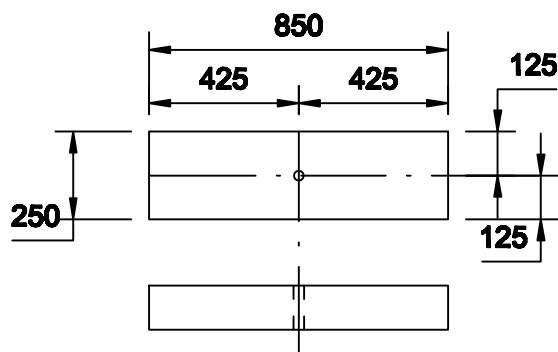


N.E. CAT NO

TYPE 1 235139

TYPE 2 235124

NOTES:

1. TIMBER TO BE BALTIC REDWOOD, SCOTS PINE (PINUS SYLVESTRIS)
OR FRENCH MARITIME PINE, GENERALLY IN ACCORDANCE WITH BS 1990
2. BLOCKS TO BE CUT FROM SWAN TIMBER OF FROM THE ROUND TO PRODUCE
RECTANGULAR SECTIONS.
3. THE LONGDITUDINALLY CUT SURFACES OF BLOCKS SHALL BE STRAIGHT AND
CLEAN CUT AND THE ANNULAR RINGS SHALL BE APPROX. PARALLEL TO THE
WIDE FACE. PLANING IS NOT REQUIRED. WANE IS PERMISSIBLE ON ONE FACE.
4. BLOCKS SHALL BE TREATED WITH A) CREOSOTE TO BS913 (RUEPING PROCESS)
OR B) WATER - BOURNE SALTS (TANALITH C) TO BS 4072

ALL DIMENSIONS SHOWN ARE IN MILLIMETRES UNLESS OTHERWISE STATED



Lloyds Court, 78, Grey Street, Newcastle Upon Tyne NE1 6AF

**OVERHEAD LINES
WOOD BLOCKS (STAY AND FOUNDATIONS)**

Prepared By
J.L.W.

Checked
G.H.

Date issued
JUNE '79

Drg.No.

1 00 043 9103

Mod.

A B C D E

Sheet No. 1

Revised. 23.2.2005

Scale 1:20