


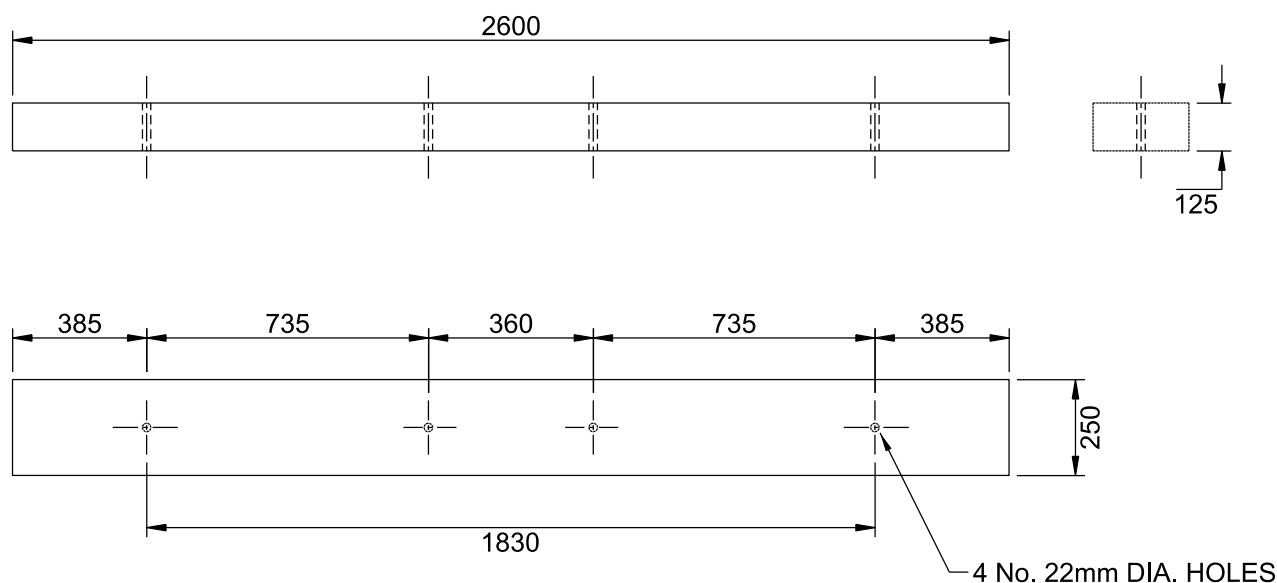

- NOTES:
- 1. TIMBER TO BE BALTIC REDWOOD SCOTS PINE (PINUS SYLVESTRIS) OR FRENCH MARITIME PINE, GENERALLY IN ACCORDANCE WITH B.S.1990.
 - 2. BLOCKS TO BE CUT FROM SAWN TIMBER.
 - 3. THE LONGITUDINALLY CUT SURFACES OF BLOCKS SHALL BE STRAIGHT AND CLEAN CUT AND THE ANNULAR RINGS SHALL BE APPROX. PARALLEL TO THE WIDE FACE. PLANING IS NOT REQUIRED. WANE IS PERMISSIBLE ON ONE FACE.
 - 4. BLOCKS SHALL BE TREATED AFTER FABRICATION WITH A
 - a) CREOSOTE TO B.S.913 (RUEPING PROCESS) OR
 - b) WATER - BORNE SALTS (TANALITH 'C') TO B.S.4072.
 - 5. THIS DRAWING SUPERSEDES ITEM 2 OF Drg. 1.09.101.0542.



Manufacturer Details	
Sheet No. 1	Scale 1:20
Prepared By Joan.Oakley	
Revised 13/12/13	Grid Reference
Date Issued 06/12/13	Checked By G HAMMEL

Lloyds Court, 78 Grey Street, Newcastle Upon Tyne, NE1 6AF			
WOOD BRACE BLOCK (250 X 125 SECTION) FOR 'H' POLES 1830MM CENTRES			
Type OVERHEAD		STANDARDS	
Ref No.	C1029724	Historic Drg.No.	1000439112
Revision	Notes		