


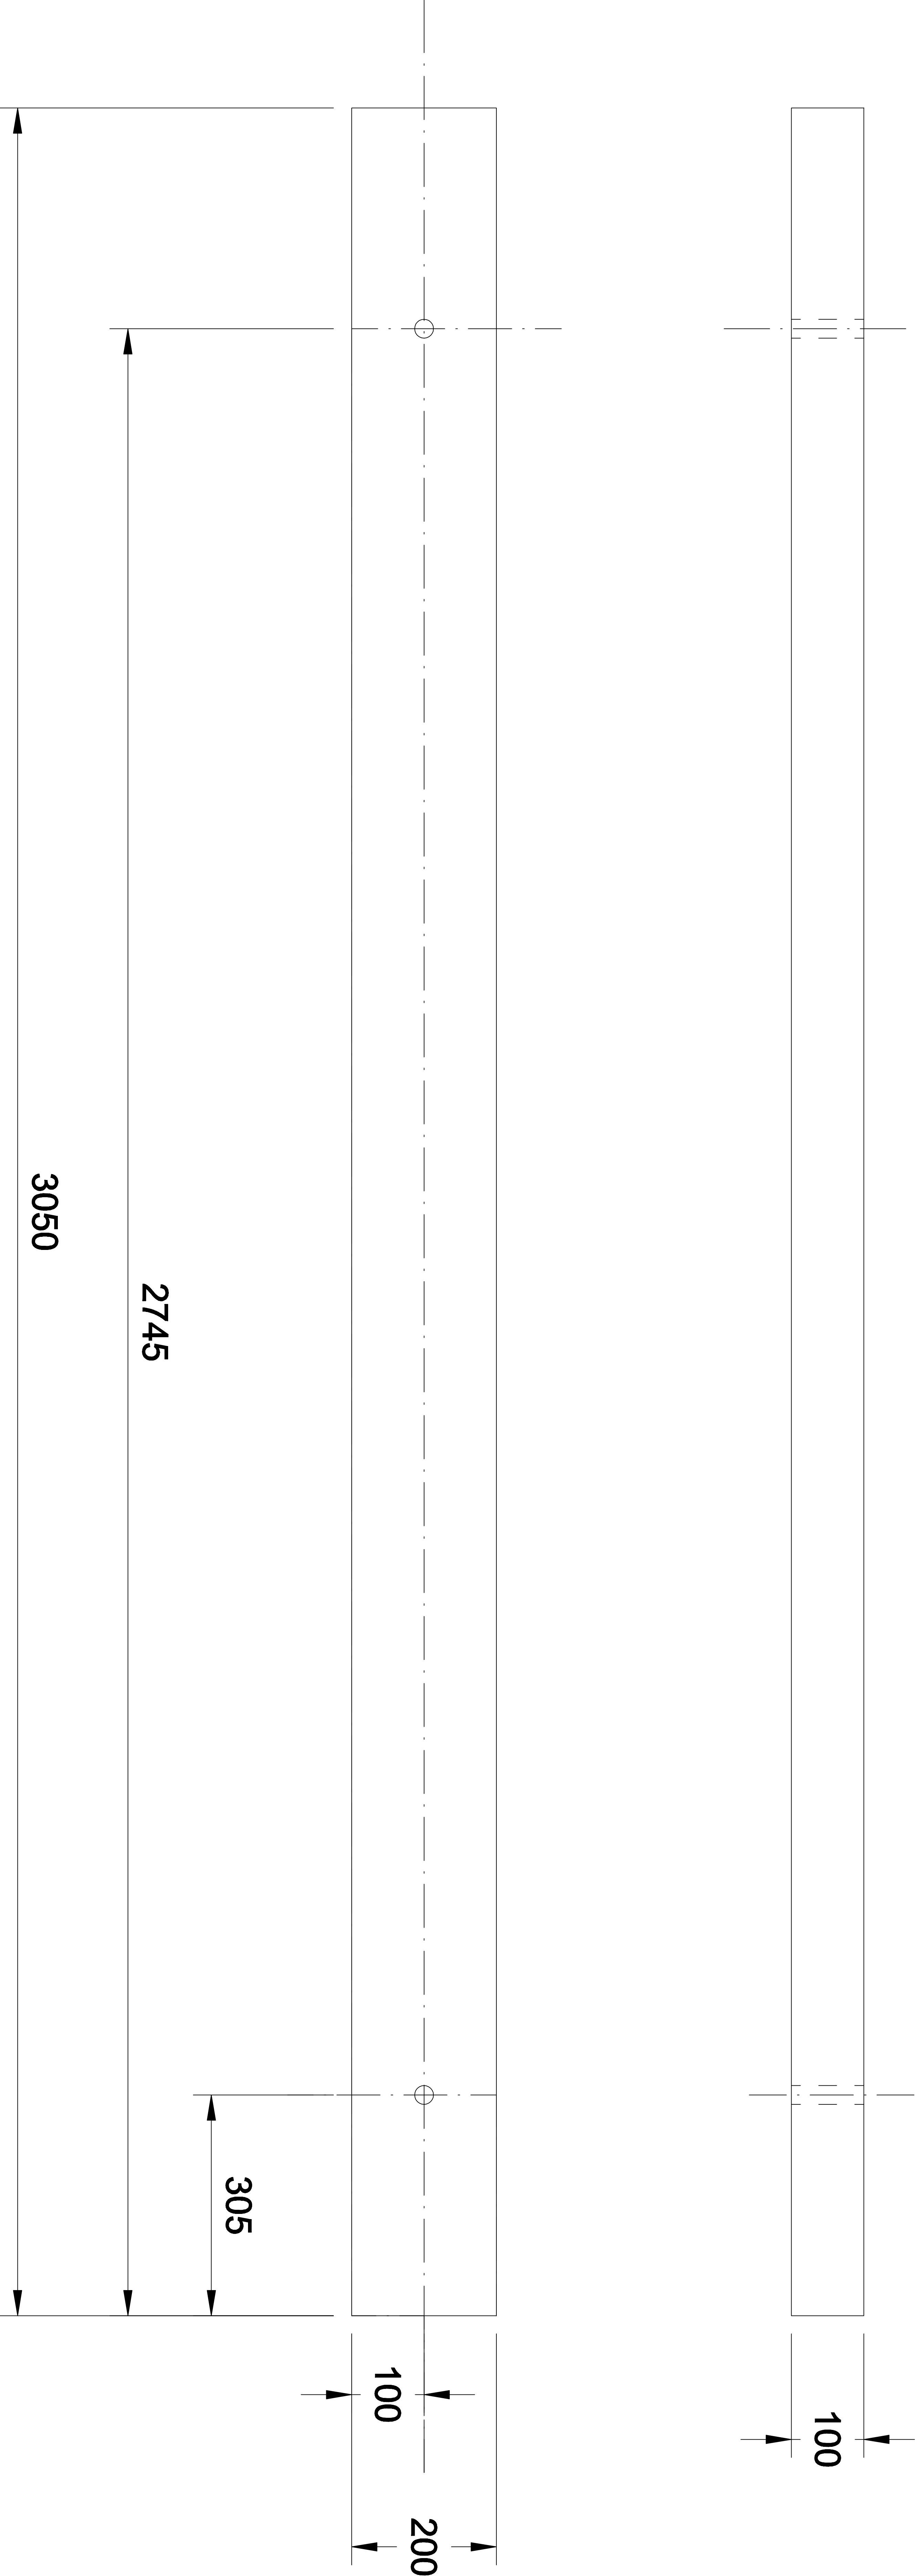

NOTES

1. BAULKS CUT FROM IMPORTED RED FIR.
CREOSOTED TO BS 913 BY RUEPING PROCESS, AFTER FABRICATION
2. ALL HOLES 26mm DIA DRILLED AT RIGHT ANGLES TO CENTRE LINE OF
BAULK

FORMERLY YE DRAWING No Y204L0301

Lloyds Court, 78, Grey Street, Newcastle Upon Tyne, NE1 6AF

BRACE BLOCK

CE/C/37M

Prepared by	J.L.W.	Dwg.No.	1	09	101	0668	Sheet No.	1	
Checked	G.H.	Date Issued	JAN	05				Revised	
							Scale	1:10@A3	

ALL DIMENSIONS SHOWN ARE IN MILLIMETRES UNLESS OTHERWISE STATED