


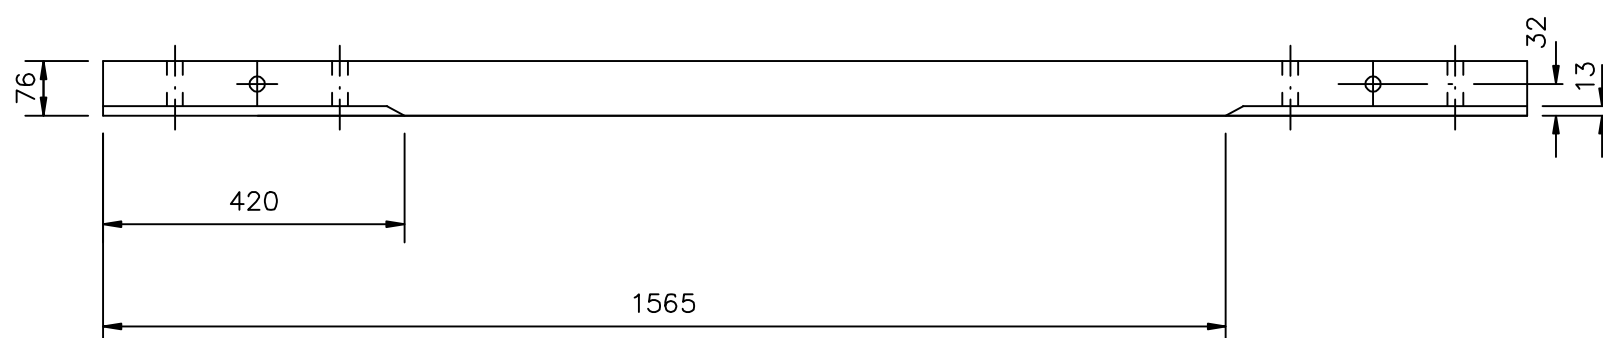

MATERIAL: BEST QUALITY SELECTED PURPLEHEART TIMBER

		Lloyds Court, 78, Grey Street, Newcastle Upon Tyne, NE1 6AF	
		TIMBER INSERT FOR CROSSARMS OVERHEAD LINES SPEC DC1	
Prepared by BFR	Drg.No.	1 09 138 0007	Sheet No. 1
Checked GH	Date Issued FEB'05		Revised
	Mods.		Scale 1:10