


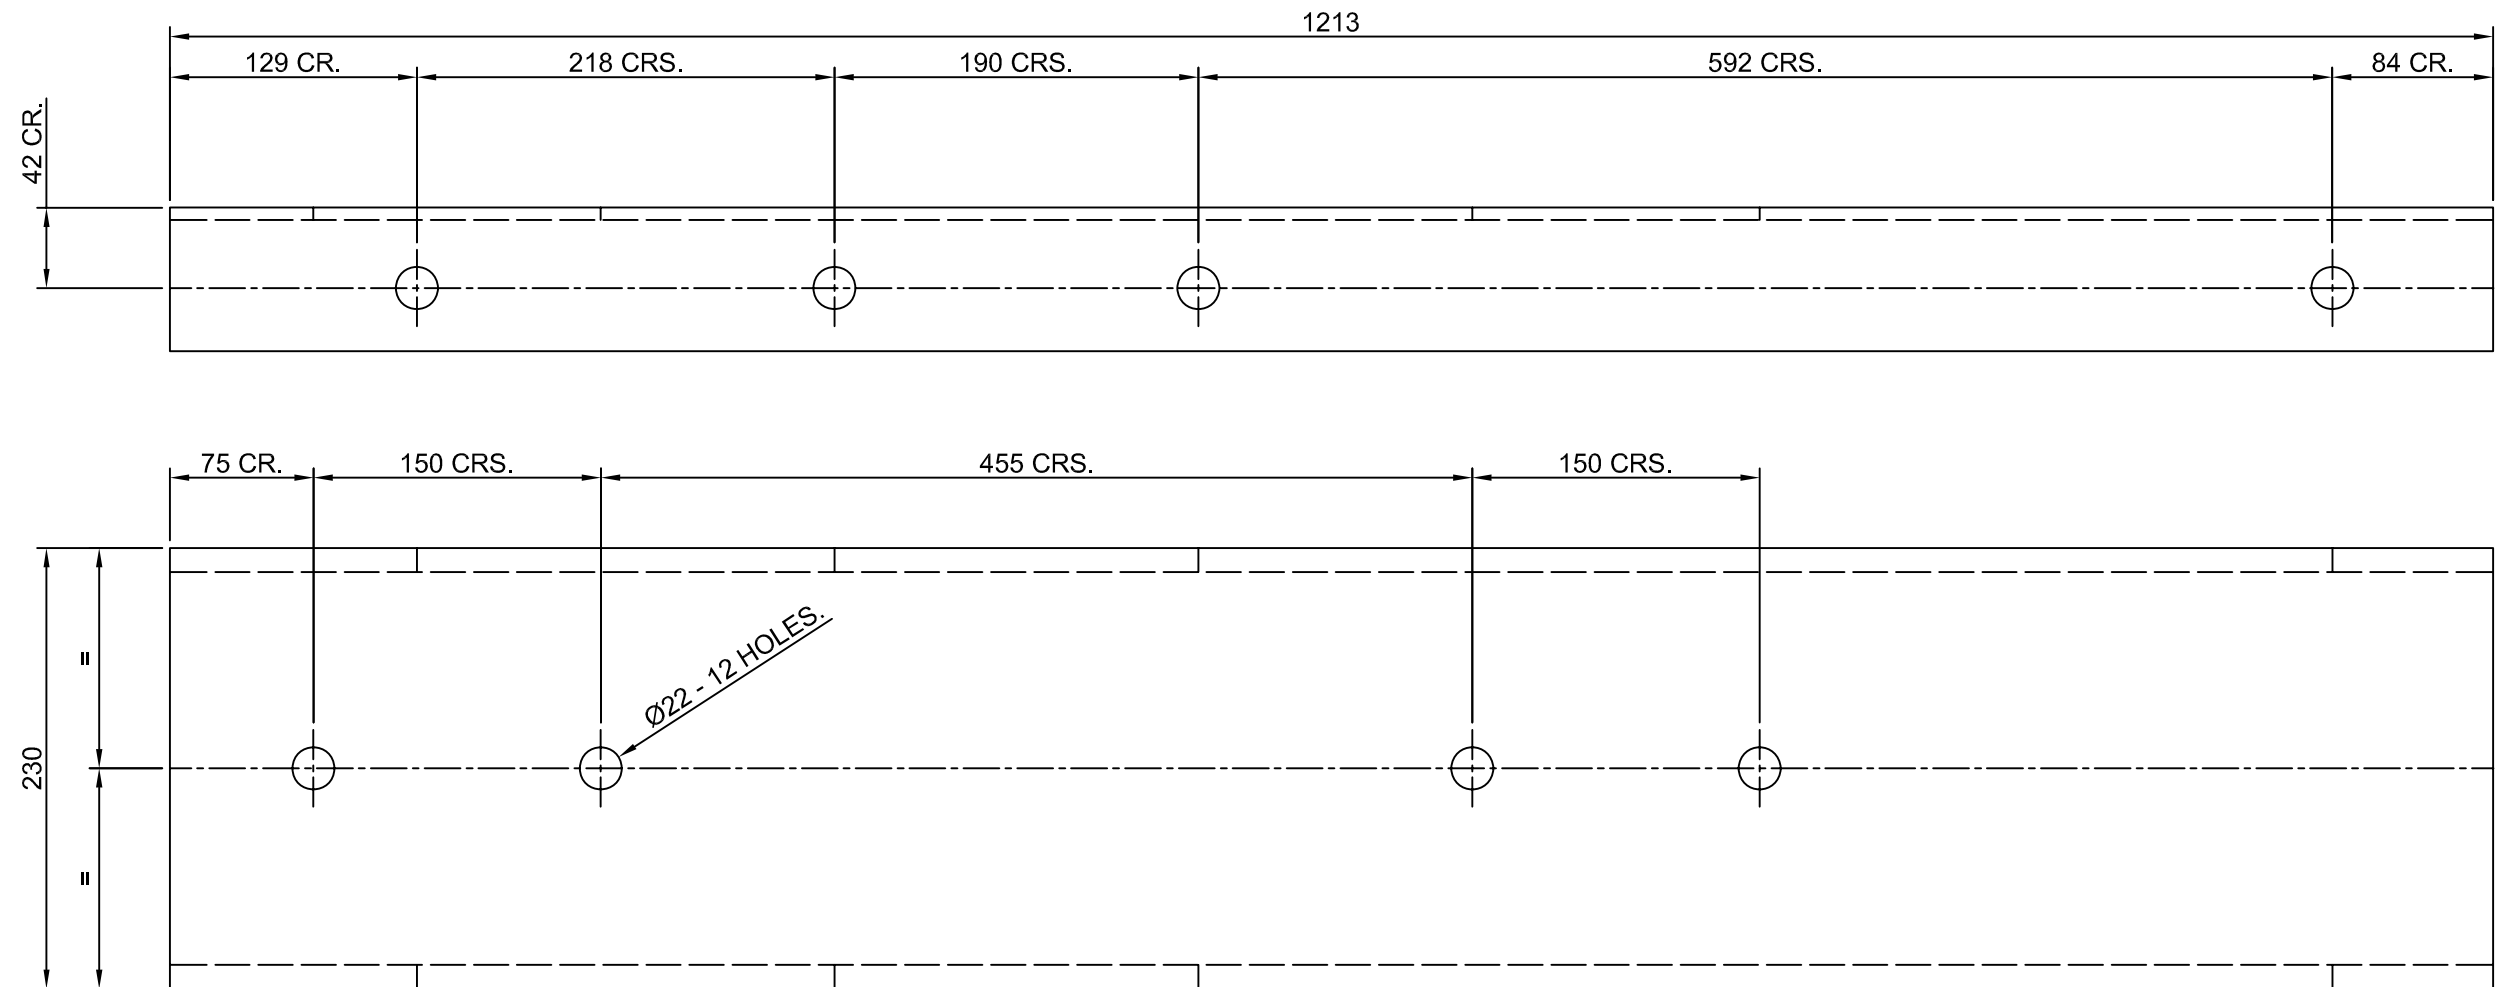

ITEM 10. 1213 LONG x 230 WEB x 75 FLANGE (25.7 kg/m) PARALLEL FLANGE CHANNEL TO B.S. 4 PART 1: 1993.

- NOTES:-
- 1. STEELWORK TO B.S. 4360, GRADE 43A & B.S. 449
 - 2. SECTIONS TO B.S. 4, PART 1, FLATS TO B.S. 6722
 - 3. ALL BURRS TO BE REMOVED.
 - 4. GALVANIZING TO B.S. 729 AFTER FABRICATION.

CE Electric UK		Lloyds Court, 78 Grey Street, Newcastle Upon Tyne, NE1 6AF			
Manufacturer Details		132kV OVERHEAD LINES 125kN TENSION INSULATOR SET SHORT CROSSARM SUPPORT CHANNEL FOR IN-LINE POLES ITEM No.10			
Sheet No. 10	Scale 1:4				
Prepared By TREVOR R. WILKIN					
		Type OVERHEAD	DOCUMENT_SUB_CLASS		
Revised	Grid Reference	Ref No.	62470B	Historic Drg.No.	1 09 101 0675
Date Issued 17/3/2006	Checked By	Revision	Notes		