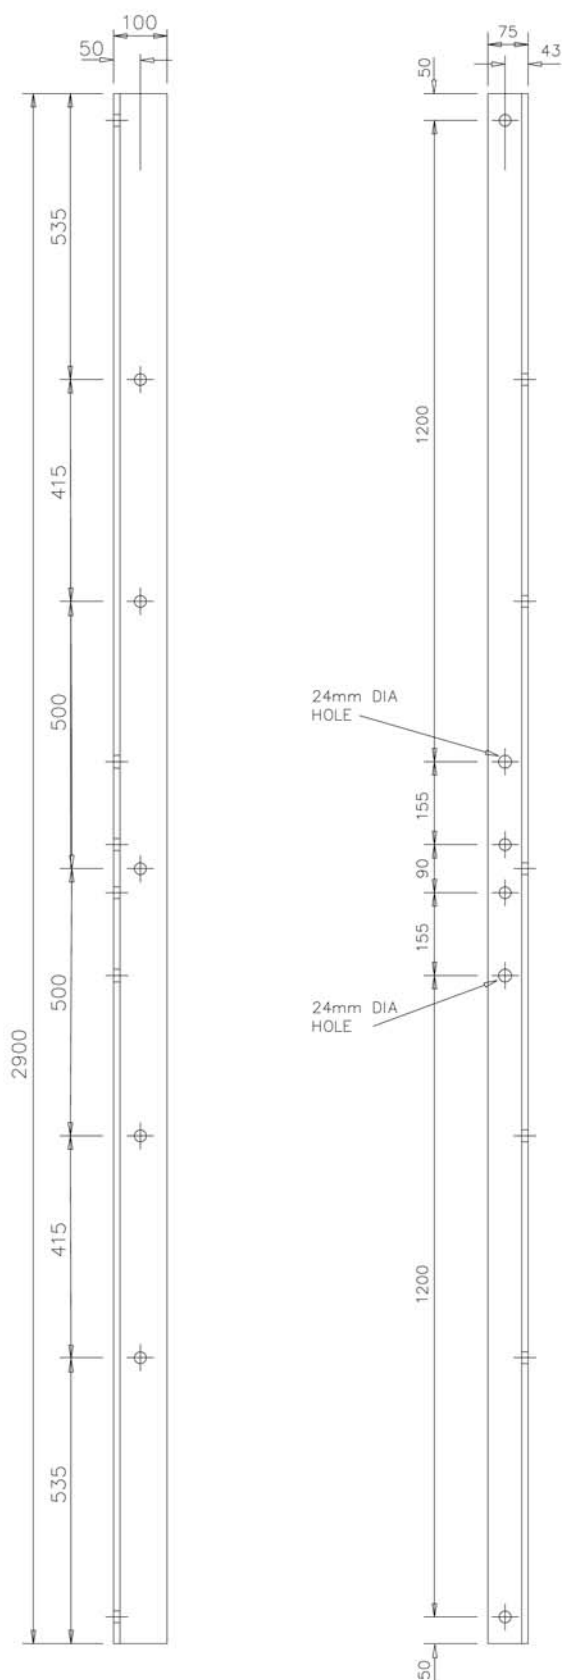



MATERIAL: -

100x75x12 ANGLE 2900 LONG

NOTES: -

1. STEELWORK TO B.S.EN 10025, GRADE Fe 430B
2. UNEQUAL ANGLE SECTIONS SHALL CONFORM TO B.S.4848 PART 4
3. ALL FERROUS MATERIAL SHALL BE HOT DIP GALVANISED IN ACCORDANCE WITH B.S.729 AFTER FABRICATION
4. COMPONENT TO BE MARKED WITH E.S.I. STANDARD DRAWING NUMBER AND NORTHERN ELECTRIC CAT.No.
5. HOLES TO BE 22mm DIA. UNLESS DETAILED OTHERWISE

ALL DIMENSIONS SHOWN ARE IN MILLIMETRES UNLESS OTHERWISE STATED

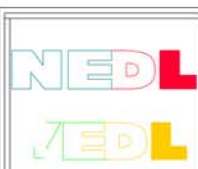

Prepared by JAB
 Checked HAJ Date Issued AUG'81

Lloyds Court, 78, Grey Street, Newcastle Upon Tyne, NE1 6AF

OVERHEAD LINES H.V. CONSTRUCTION
 CROSSARM MEMEBER 2900 LONG

Drg.No.

1 00 043 9520

Mods. C

Sheet No.

1

Revised

30/11/04

Scale

1:10