



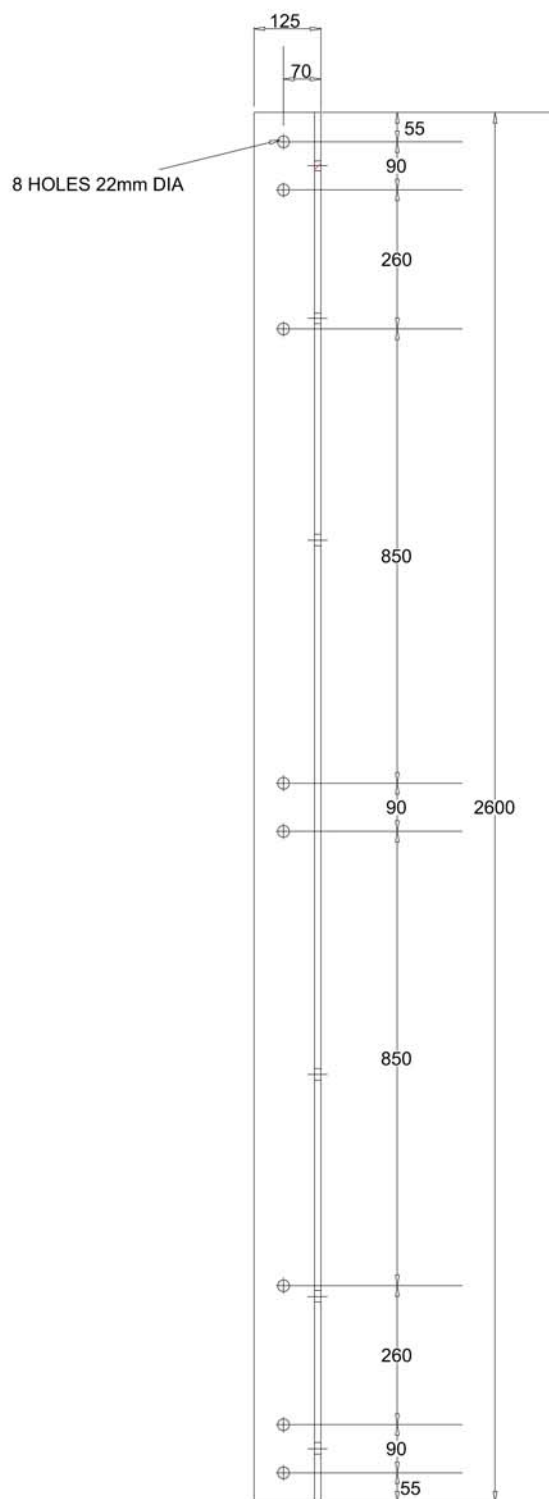

Material:-
125 x 75 x 12 Angle 2600 Long.

NOTES:-

1. Steelwork to B.S. EN10025, Grade Fe430B.
2. Unequal angle sections shall conform to B.S.4848, Part 4.
3. All ferrous material shall be hot dip galvanised in accordance with B.S.723 after fabrication.
4. Component to be marked with E.S.I. standard drawing number and Northern Electric Cat. No.

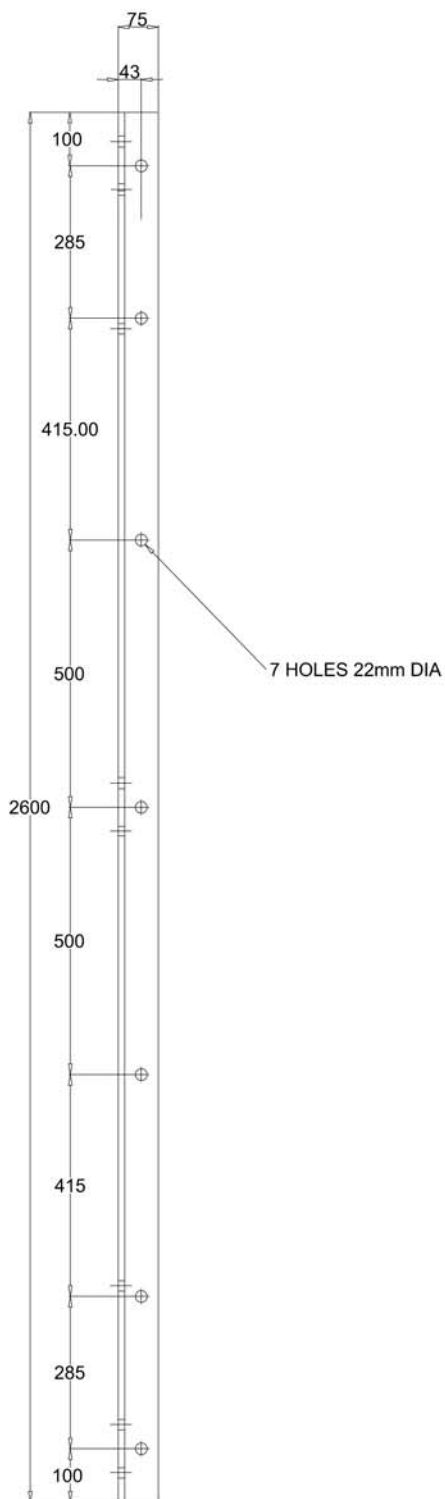

Prepared by J.L.W.
Checked G.H. Date Issued JULY 81

Lloyds Court, 78, Grey Street, Newcastle Upon Tyne, NE1 6AF

**OVERHEAD LINES. HV CONSTRUCTION
CROSSARM STEELWORK**

Drg.No. 1 00 043 9522

Mods. A B C

Sheet No. 1
Revised 26.11.04
Scale 1:10@A3

All dimensions shown are
in millimetres unless
otherwise stated.