


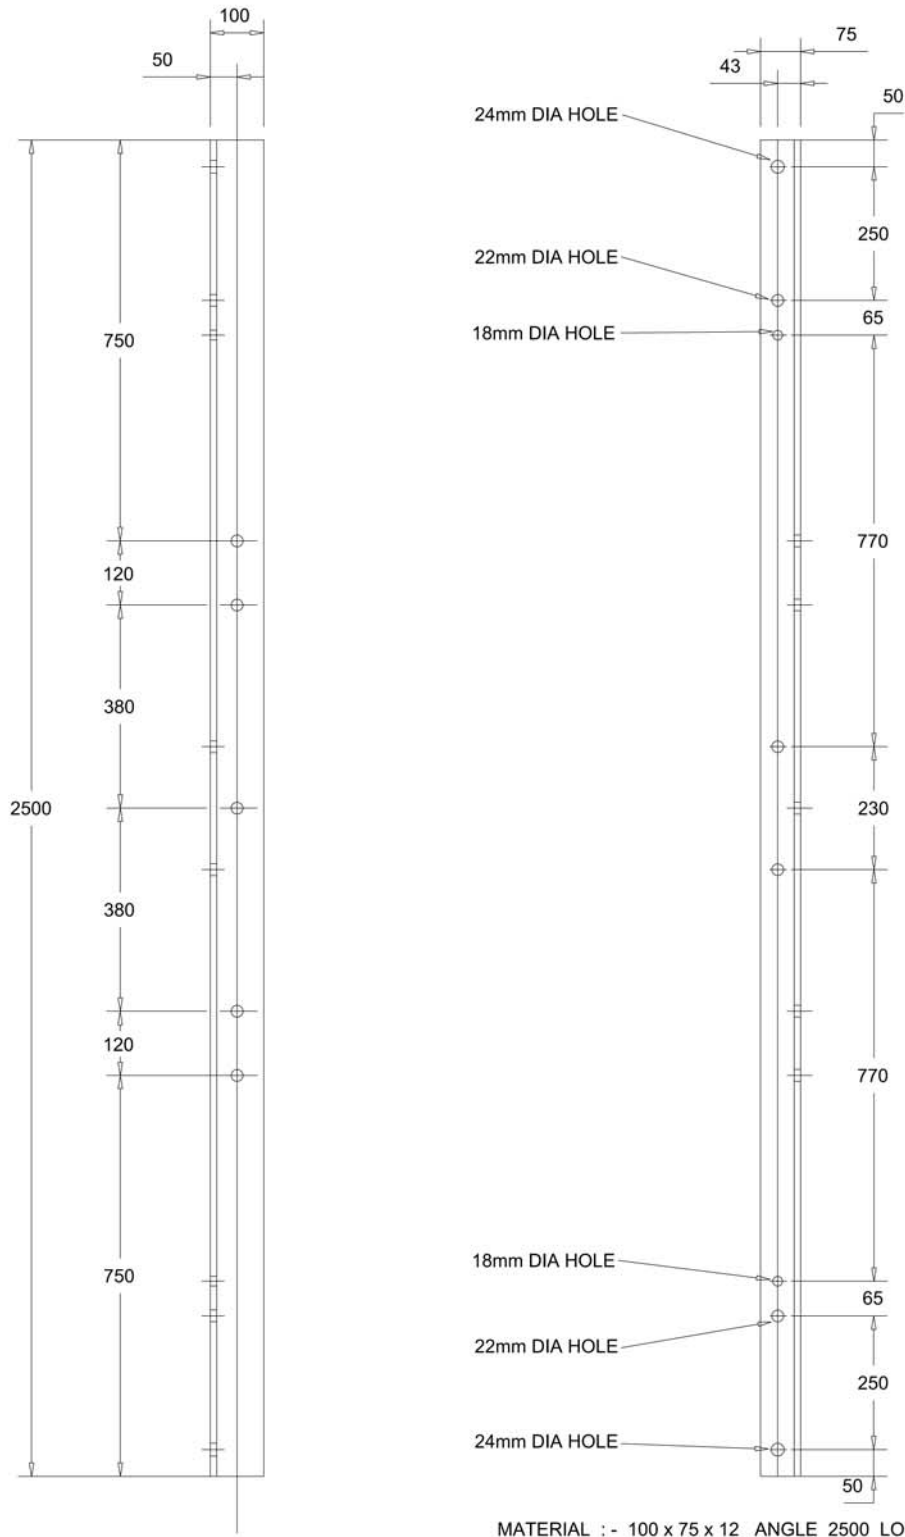

MATERIAL :- 100 x 75 x 12 ANGLE 2500 LONG

NOTES

1. STEELWORK TO B.S. EN 10025, GRADE Fe 430B
2. UNEQUAL ANGLE SECTIONS SHALL CONFORM TO B.S. 4848, PART 4
3. ALL HOLES TO BE 22mm DIA UNLESS DETAILED OTHERWISE
4. ALL FERROUS MATERIAL SHALL BE HOT DIP GALVANISED IN ACCORDANCE WITH B.S. 729 AFTER FABRICATION
5. COMPONENT TO BE MARKED WITH ESI STANDARD DRAWING NUMBER AND NEDL STOCK CAT. No.

ALL DIMENSIONS SHOWN ARE IN MILLIMETRES UNLESS OTHERWISE STATED

		Lloyds Court, 78, Grey Street, Newcastle Upon Tyne NE1 6AF										
		CROSSARM FOR SINGLE POLE H.V. LINES (APPLICATION GENERAL)										
Prepared by	J.L.W.	Drg.No.	1 00 043 9557							Sheet No.	1	
Checked	H.S.M.	Date Issued	DEC '87							Revised	JUNE 03	
		Mods.	A	B	C						Scale	1 : 10