


N.E. CAT. No	
ITEM 41	245287
ITEM 42	245291

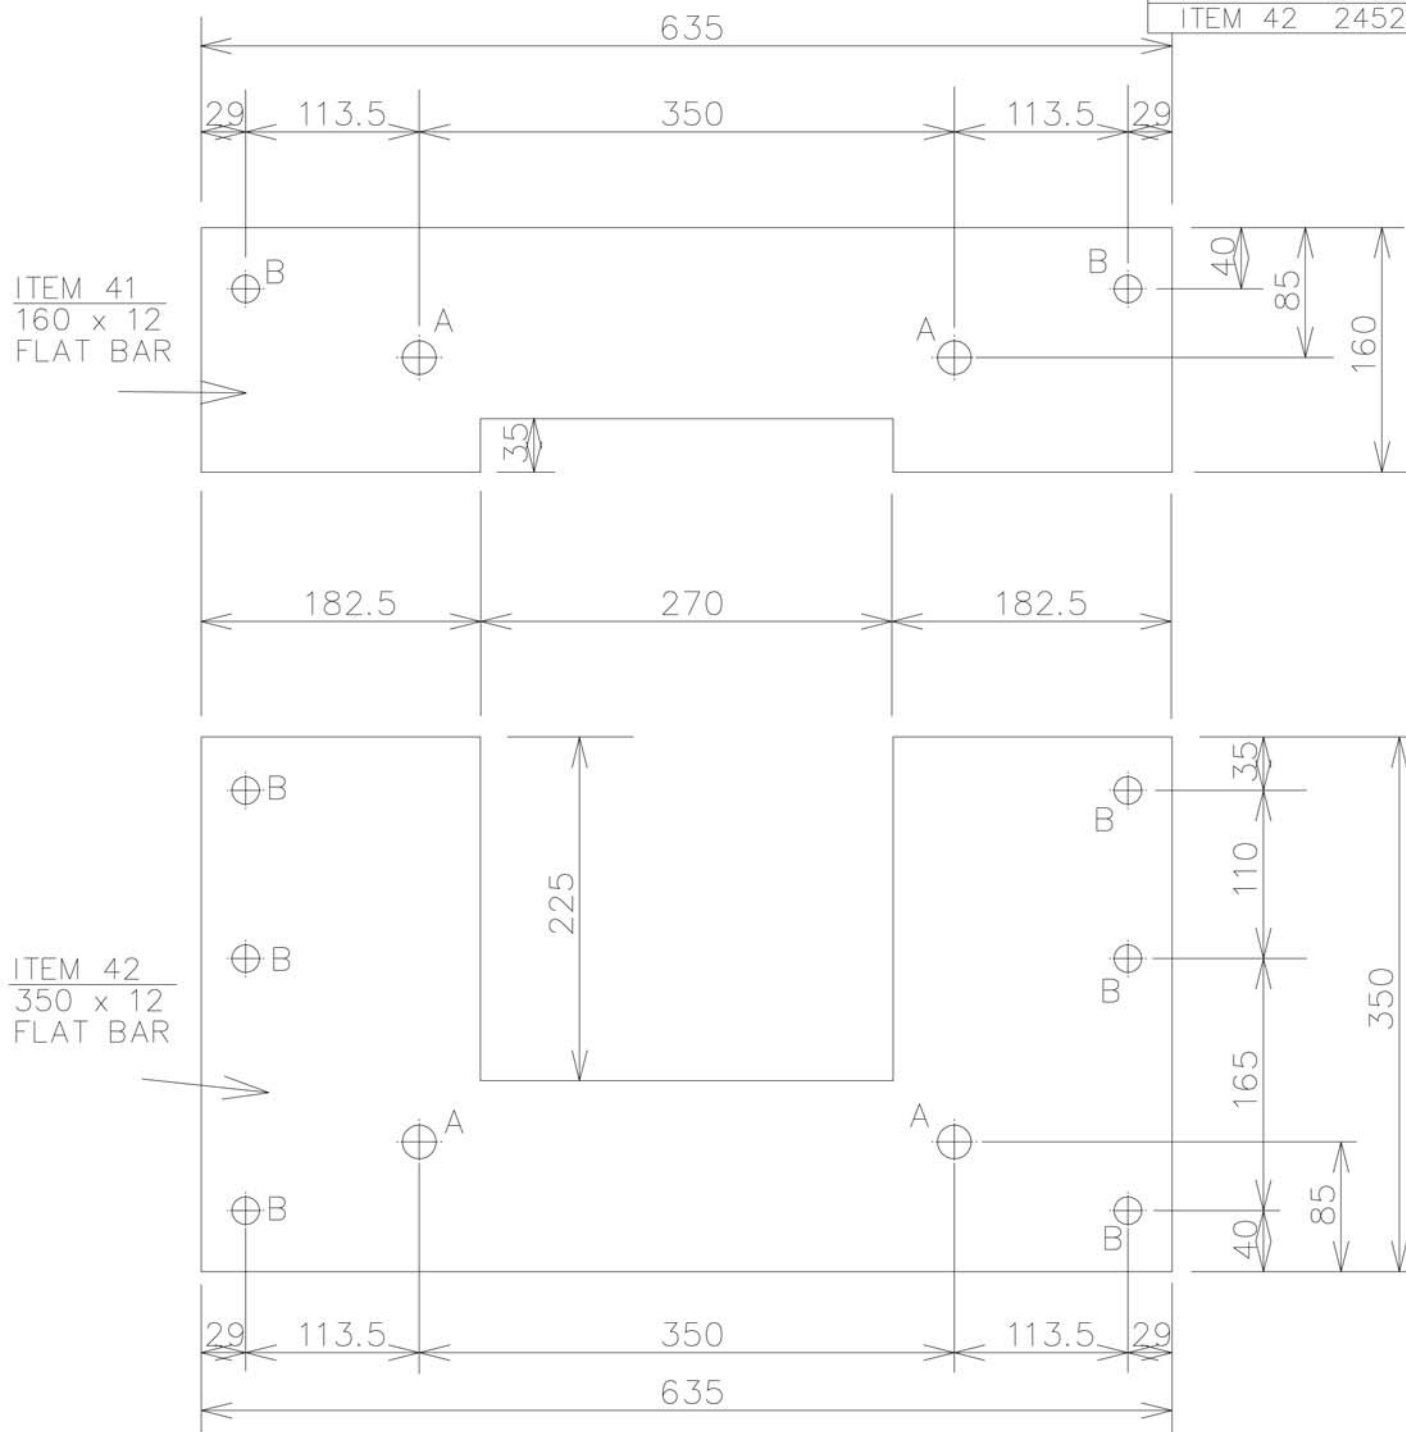

NOTES

STEELWORK TO BS EN 10025, GRADE Fe430B GALVANISED TO BS 729 AFTER FABRICATON

ALL DIMENSION SHOWN ARE IN MILLIMETRES UNLESS OTHERWISE STATED

 NORTHERN ELECTRIC DISTRIBUTION	Northern Electric Distribution Limited, Carlisle House, Newcastle Upon Tyne									
	66kV SINGLE CIRCUIT OVERHEAD LINES SUPPORT PLATES FOR SEALING END APEB ON IRONWORK TO DRAWING 1.09.123.1172									
	Drg.No.	1 09 101 0308								
	Sheet No.	7								
Prepared By JLW	Checked SW	Date Issued JUNE 80	Mod.	A	B	C				
			Revised.	JULY 99						
			Scale	1:5						