



ITEM 1.

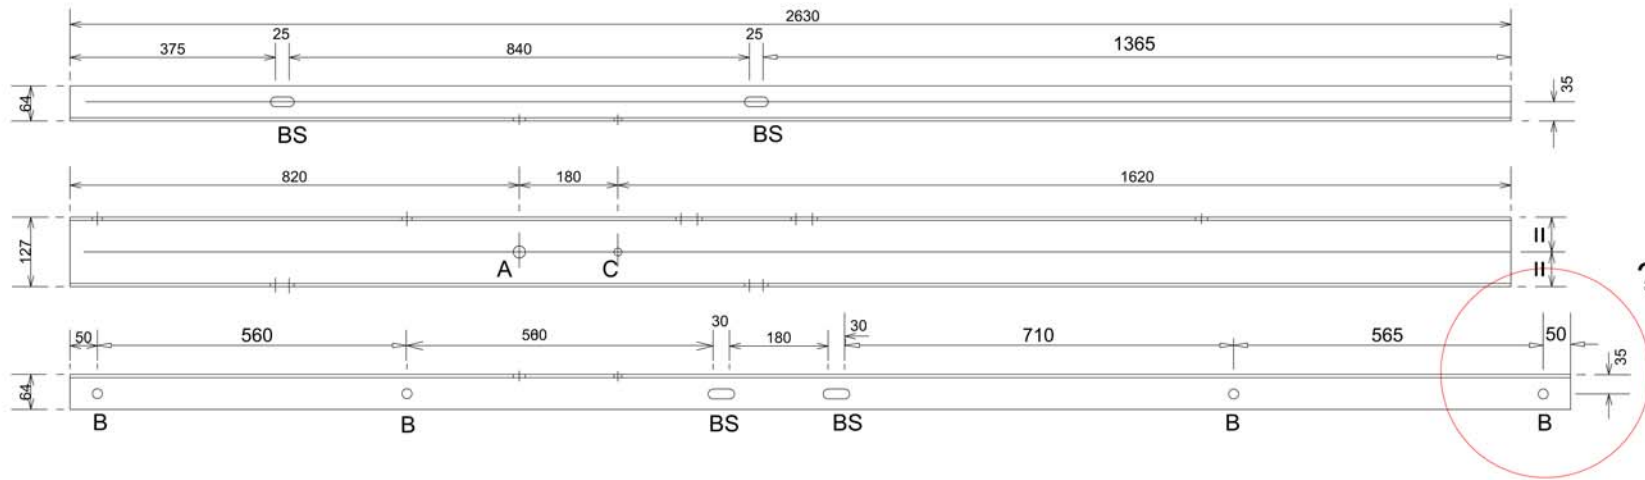

ITEM 2.

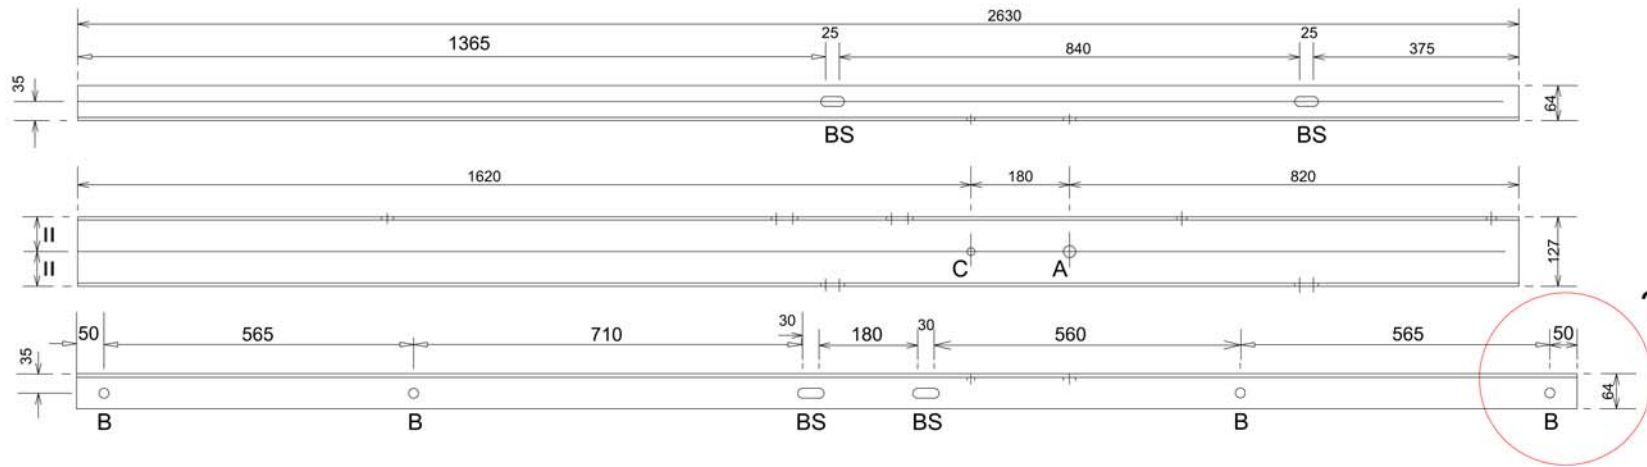

NOTES:-

1. STEELWORK TO BS EN 10025, GRADE Fe430B.
2. GALVANISING TO BS EN 1461 AFTER FABRICATION.

HOLE DIAMETERS	
A	22mm
B	18mm
C	14mm
BS	18mm SLOT

		Lloyds Court, 78 Grey Street, Newcastle Upon Tyne, NE1 6AF	
Manufacturer Details		SUPPORT SET FOR 66KV DOUBLE CIRCUIT ARRANGEMENT WITH SURGE ARRESTERS	
Sheet No. 6	Scale 1:10		
Prepared By Barbara Gordon		Type OVERHEAD	LINES
Revised 15/07/09	Grid Reference	Ref No. C977290	Historic Drg.No. 1091010551
Date Issued 15/07/09	Checked By M WILSON	Revision	Notes