




ITEM	CATALOGUE No
8	234507
9	240315
10	244208

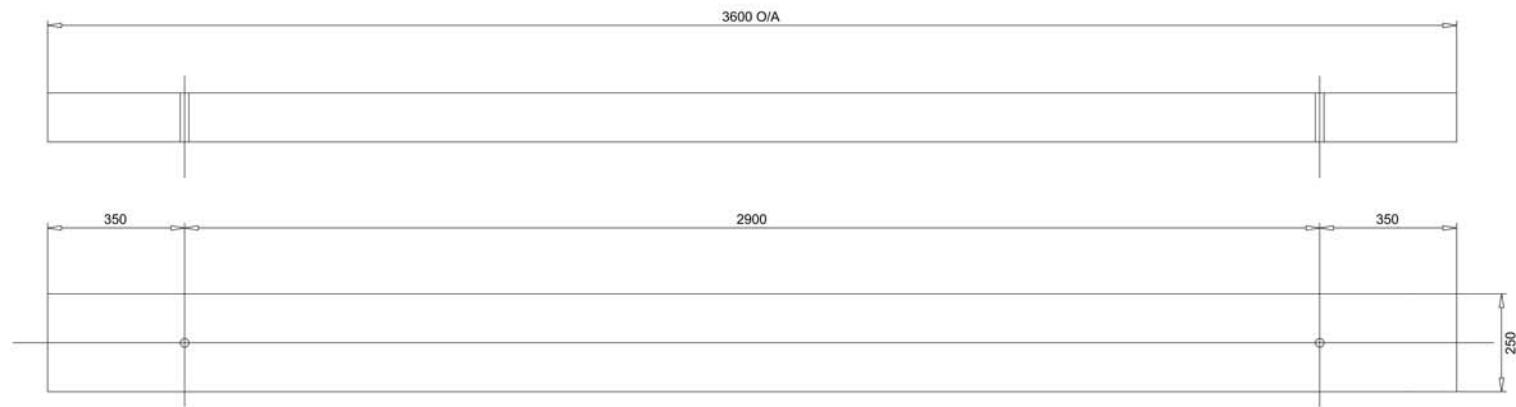

ITEM 8 3600 x 250 x 125 WOOD BAULK
SCALE :- 1 : 10

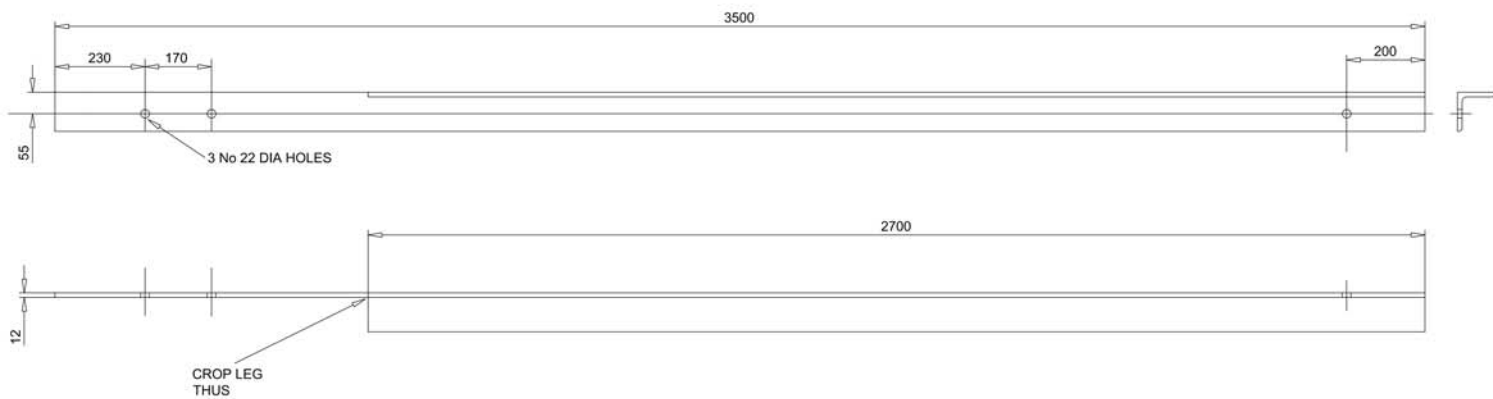

ITEM 9 100 x 100 x 12 ANGLE - 3500 LONG
SCALE 1 : 10

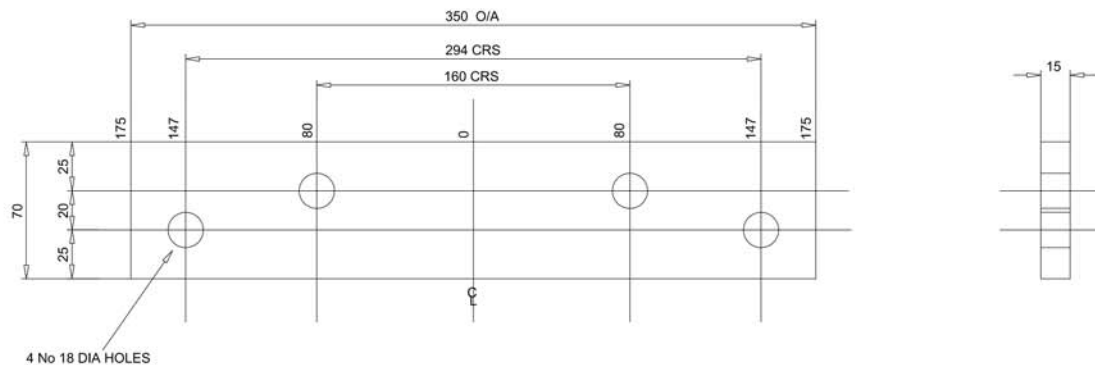

ITEM 10 70 x 15 x 350 LONG - FLAT BAR
SCALE 1 : 2

NOTES

1. TIMBER TO BE BALTIC REDWOOD, SCOTS PINE (PINUS SYLVESTRIS) OR FRENCH MARITIME PINE GENERALLY IN ACCORDANCE WITH BS 1990 PART 1
2. BAULKS TO BE CUT FROM SAWN TIMBER TO PRODUCE RECTANGULAR SECTIONS
3. THE LONGITUDINALLY CUT SURFACES OF BAULKS SHALL BE STRAIGHT AND CLEAN CUT AND THE ANNULAR RINGS SHALL BE APPROX PARALLEL TO WIDE FACE. PLANNING IS NOT REQUIRED
4. BAULKS SHALL BE TREATED AFTER FABRICATION WITH CEOSOTE TO BS 913 (RUEPING PROCESS) OR WATERBOURNE SALTS (TANALITH) TO 4072
5. STEELWORK TO BS4360, GRADE 43A AND BS449
6. FLATS TO BS6722 ANGLES TO BS4848 PART 4
7. GALVANISING TO BS729 AFTER FABRICATION

ALL DIMENSIONS SHOWN ARE IN MILLIMETRES UNLESS OTHERWISE STATED

		Lloyds Court, 78 Grey Street, Newcastle Upon Tyne, NE1 6AF	
Manufacturer Details Sheet No. 3 Scale AS SHOWN Prepared By Caralyn Palmer Revised 25/06/07 Date Issued 25/06/07 Grid Reference Checked By G HAMMEL		66KV OVERHEAD LINES PORTAL TYPE CROSSARM AND SPECIAL FOUNDATION COMPONENTS Type OVERHEAD POLES Ref No. C949500 Historic Drg. No. 1091010650 Revision F Notes	