




ITEM 11 102 x 51 x 5300mm LONG CABLE TERMINATION SUPPORT CHANNEL

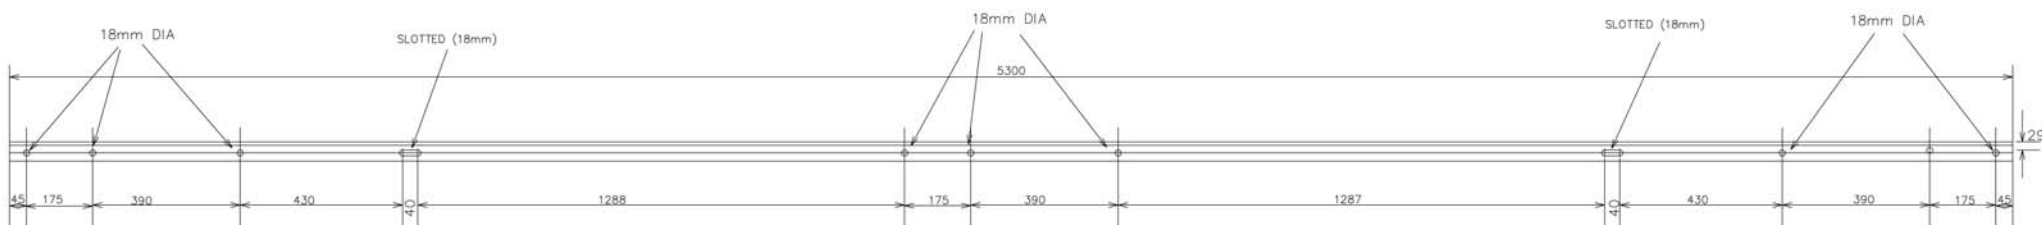

ITEM 12 102 x 51 x 5300mm LONG SURGE ARRESTOR SUPPORT CHANNEL

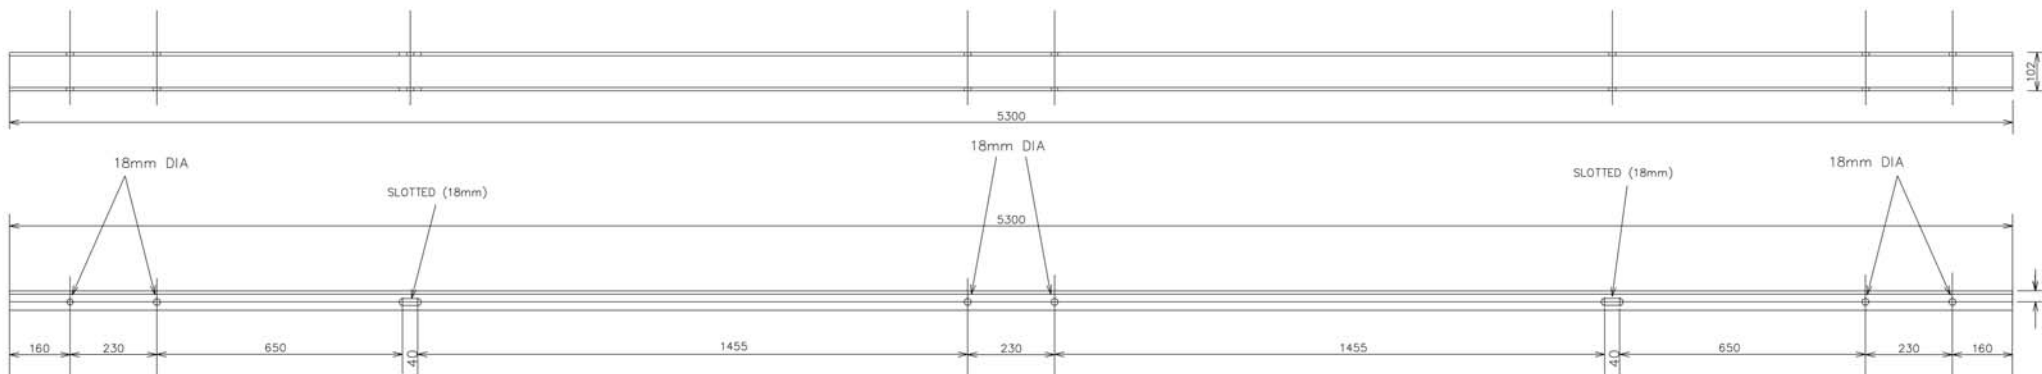

ITEM 13 127 x 64 x 3000mm LONG CABLE SUPPORT CHANNEL

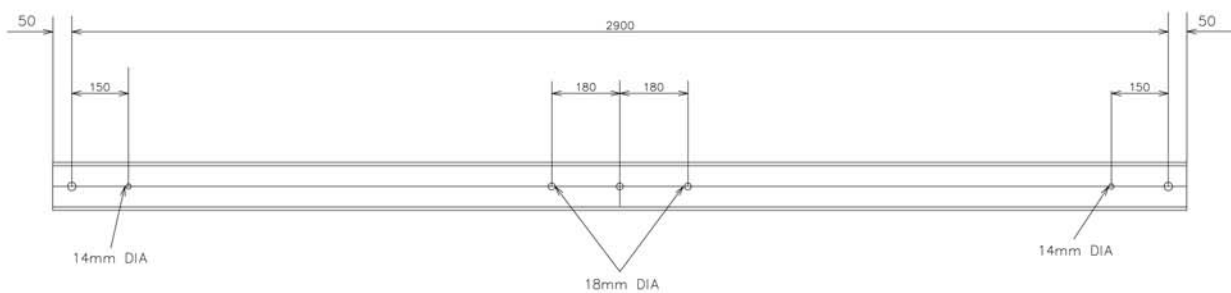

ITEM 14
60 x 8 AND 50 x 6 FLAT BAR
TO UTILISE WOOD BLOCK TO 0309/1

NOTES

1. ALL HOLES 22mm DIA UNLESS SHOWN OTHERWISE
2. STEELWORK TO BS EN 100025, GRADE FE 430B
3. GALVANISING TO BS 729 AFTER FABRICATION

ITEM	CAT No
11	240508
12	240512
13	240298
14	N/A

ALL DIMENSIONS SHOWN ARE IN MILLIMETRES UNLESS OTHERWISE STATED



Prepared by
J.L.W.
Checked
M.W.

Date Issued
JULY 96

NEDL, Manor House, Station Road, Houghton le Spring, DH4 7LA.									
66kV OVERHEAD LINES									
SURGE ARRESTOR & CABLE SUPPORT STEELWORK									
NEW CONSTRUCTION 2900 CENTRES									
Drq.No.	1	09	101	0650	Sheet No. 4				
Revised					13.3.98				
Scale					1:10				