
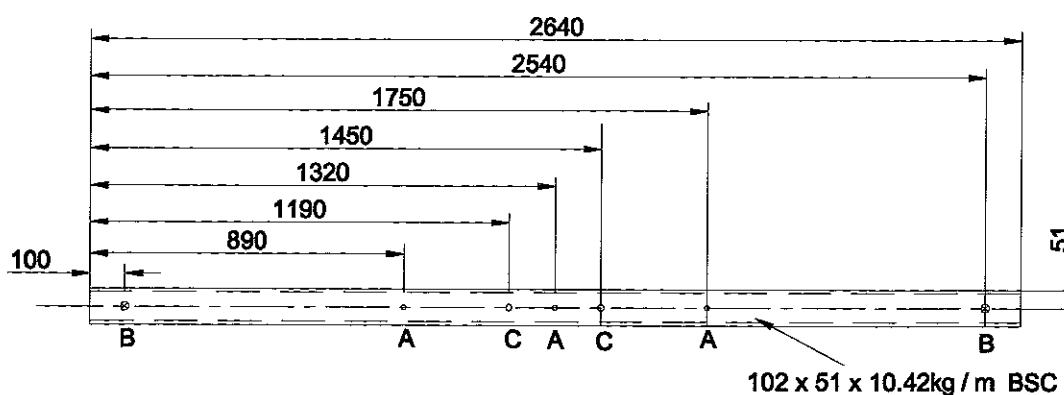
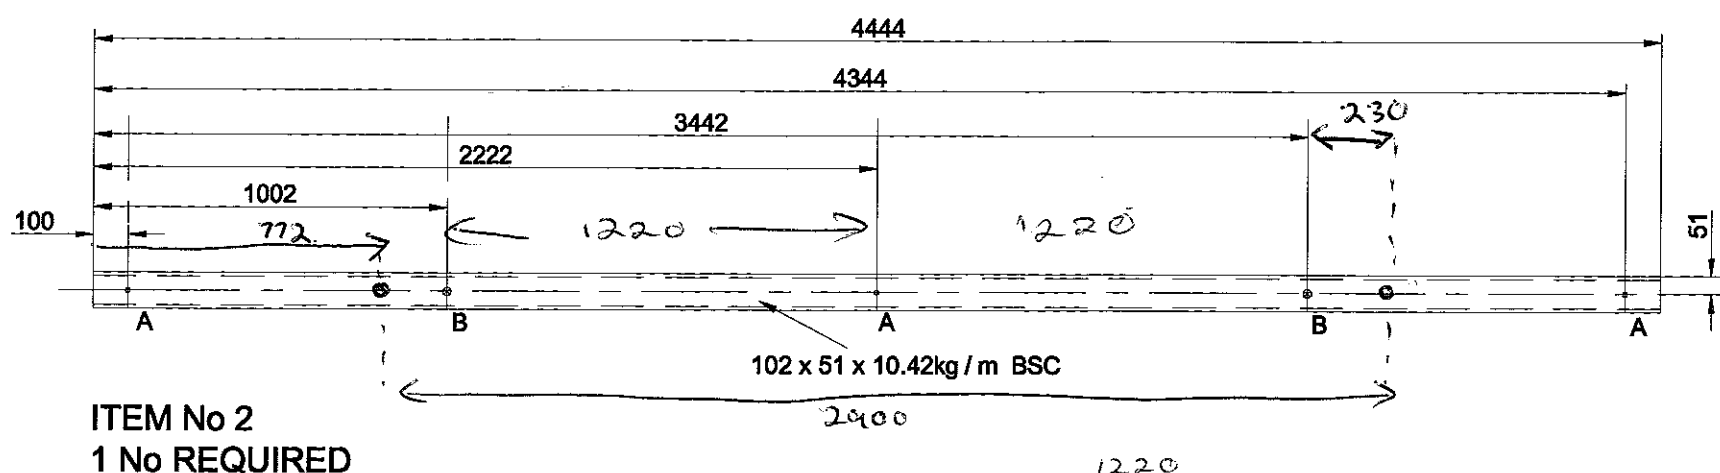


|        |        |
|--------|--------|
| Item 1 | 240280 |
| Item 2 | 240281 |
| Item 3 | NA     |

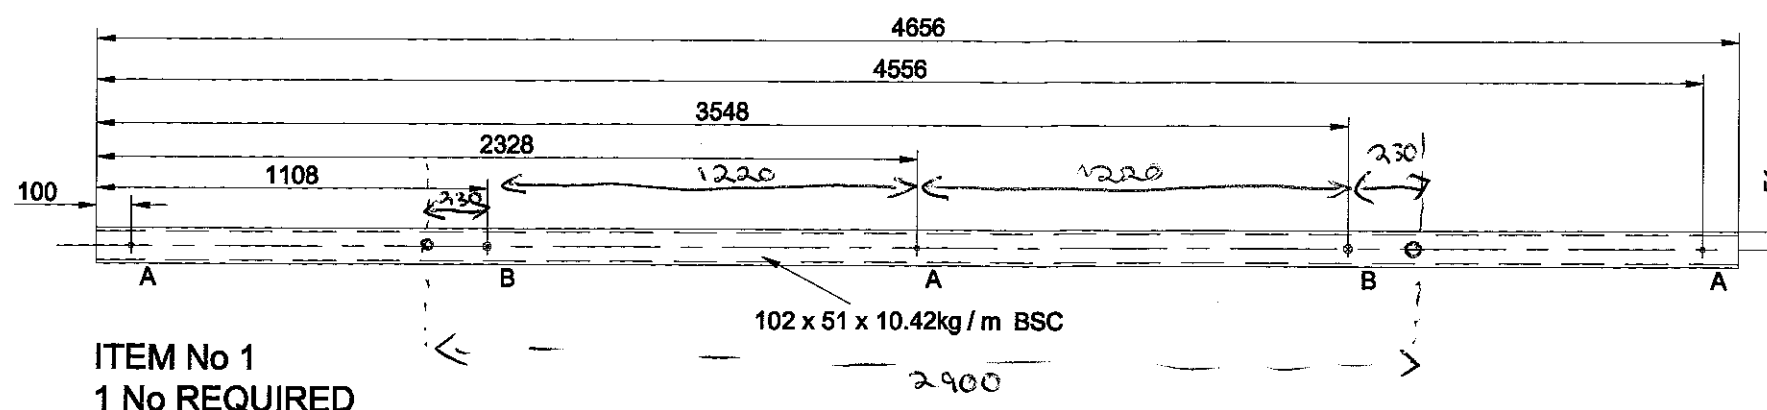

#### NOTES

1. HOLES MARKED 'A' 14 mm DIA
2. SLOTS MARKED 'B' 22 x 23mm CENTRES
3. HOLES MARKED 'C' 18mm DIA
4. ALL STEELWORK TO BS 4848 PART 4 & BS 4360 GRADE 43A
5. ALL GALVANISED IN ACCORDANCE WITH BS729

ALL DIMENSIONS SHOWN ARE IN MILLIMETRES UNLESS OTHERWISE STATED

|                        |                |   |                                   |
|------------------------|----------------|---|-----------------------------------|
| <b>CE Electric UK</b>  |                | Lloyds Court, 78 Grey Street, Newcastle Upon Tyne, NE1 6AF                                                                   |                                   |
| Manufacturer Details   |                | CABLE SUPPORT STEELWORK FOR 33 AND 66KV<br>POLYMERIC CABLE TERMINATION<br>CE / C / 37 - CE / OM / DC1 &<br>1091231173 sht 9. |                                   |
| Sheet No. <b>3</b>     | Scale 1:20     | Type OVERHEAD   | LINES                             |
| Prepared By Janis Webb | Grid Reference | Ref No. <del>240280</del>   | Historic Drg.No. <b>Y20410917</b> |
| Revised 15/05/07       | Checked By     | Revision <b>1</b>   | Notes <b>1091010650</b>           |