



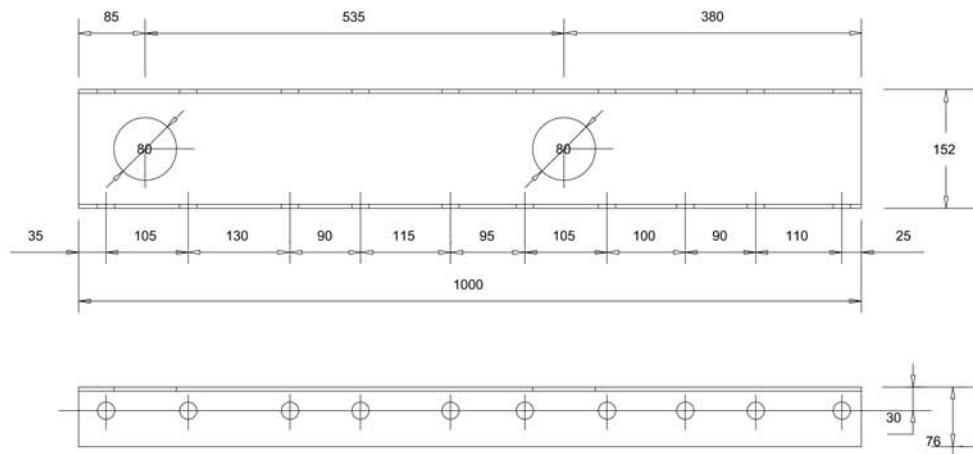

ITEM 1 VERTICAL CHANNELS
152 x 76 x 17.6kg /M 1000 LONG


SCALE 1 : 5

ITEM	CAT. No.
1	252685
2	252702
3	252717
4	252721
5	252736
6	252740
7	252755

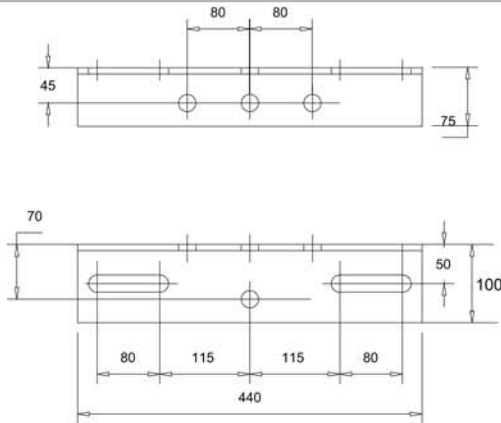


ITEM 2 POST ANGLE
100 x 75 x 8 ANGLE 440 LONG

SCALE 1 : 5

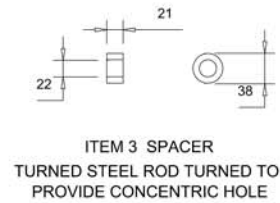


ITEM 3 SPACER
TURNED STEEL ROD TURNED TO
PROVIDE CONCENTRIC HOLE

SCALE 1 : 5

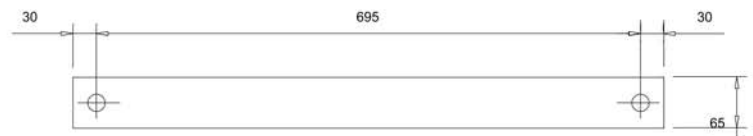


ITEM 4 TIE STRAP
65 x 8 FLAT BAR 755 LONG

SCALE 1 : 5

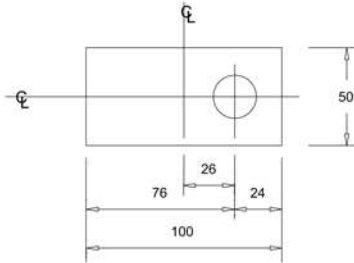


ITEM 5 SPACER
100 x 50 x 20 FLAT
MACHINE CUT SQUARE
NOT CROPPED

SCALE 1 : 2

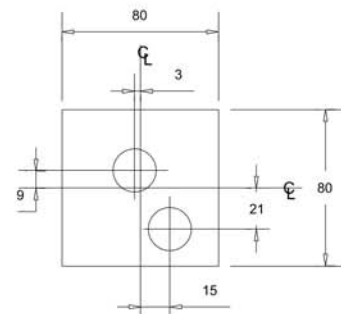

ITEM 6 VERTICAL LOCK
80 x 80 x 20 FLAT
MACHINE CUT SQUARE
NOT CROPPED

SCALE 1 : 2

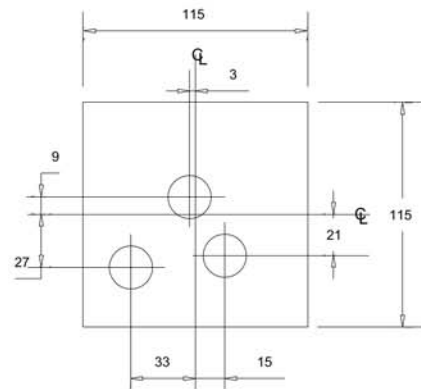

ITEM 7 HORIZONTAL LOCK
115 x 115 x 10 FLAT
MACHINE CUT SQUARE
NOT CROPPED

SCALE 1 : 2

NOTES

1. STEELWORK TO B.S. EN 10025 GRADE Fe 430B
2. UNEQUAL ANGLE SETCTIONS TO B.S. 4848 PART 4
3. ALL FERROUS MATERIALS TO BE GALVANISED TO B.S. 729 AFTER FABRICATION
4. COMPONENTS TO BE MARKED WITH DRAWING ITEM NUMBERS AND NORTHERN ELECTRIC STOCK CAT.No.
5. HOLES TO BE 22 DIA EXCEPT WHERE INDICATED OTHERWISE
6. SLOTS TO HAVE SMOOTH PARALLEL SIDES
7. ALL TOLERANCES TO BE AS SPECIFIED IN ESI 43-95



Manufacturer Details

Sheet No. 1 Scale AS SHOWN

Prepared By Barbara Gordon

Revised 12/05/10 Grid Reference

Date Issued 12/05/10 Checked By G HAMMEL

Lloyds Court, 78 Grey Street, Newcastle Upon Tyne, NE1 6AF

66/132KV SINGLE CIRCUIT LINES
TOP HAMPER STEELWORK DETAILS
SINGLE & 'A' POLES

Type OVERHEAD STANDARDS

Ref No. C986997 Historic Drg.No. 1091010652

Revision M Notes